


BASE THBS - LOCAÇÃO ESTACAS
ESCALA 1:25

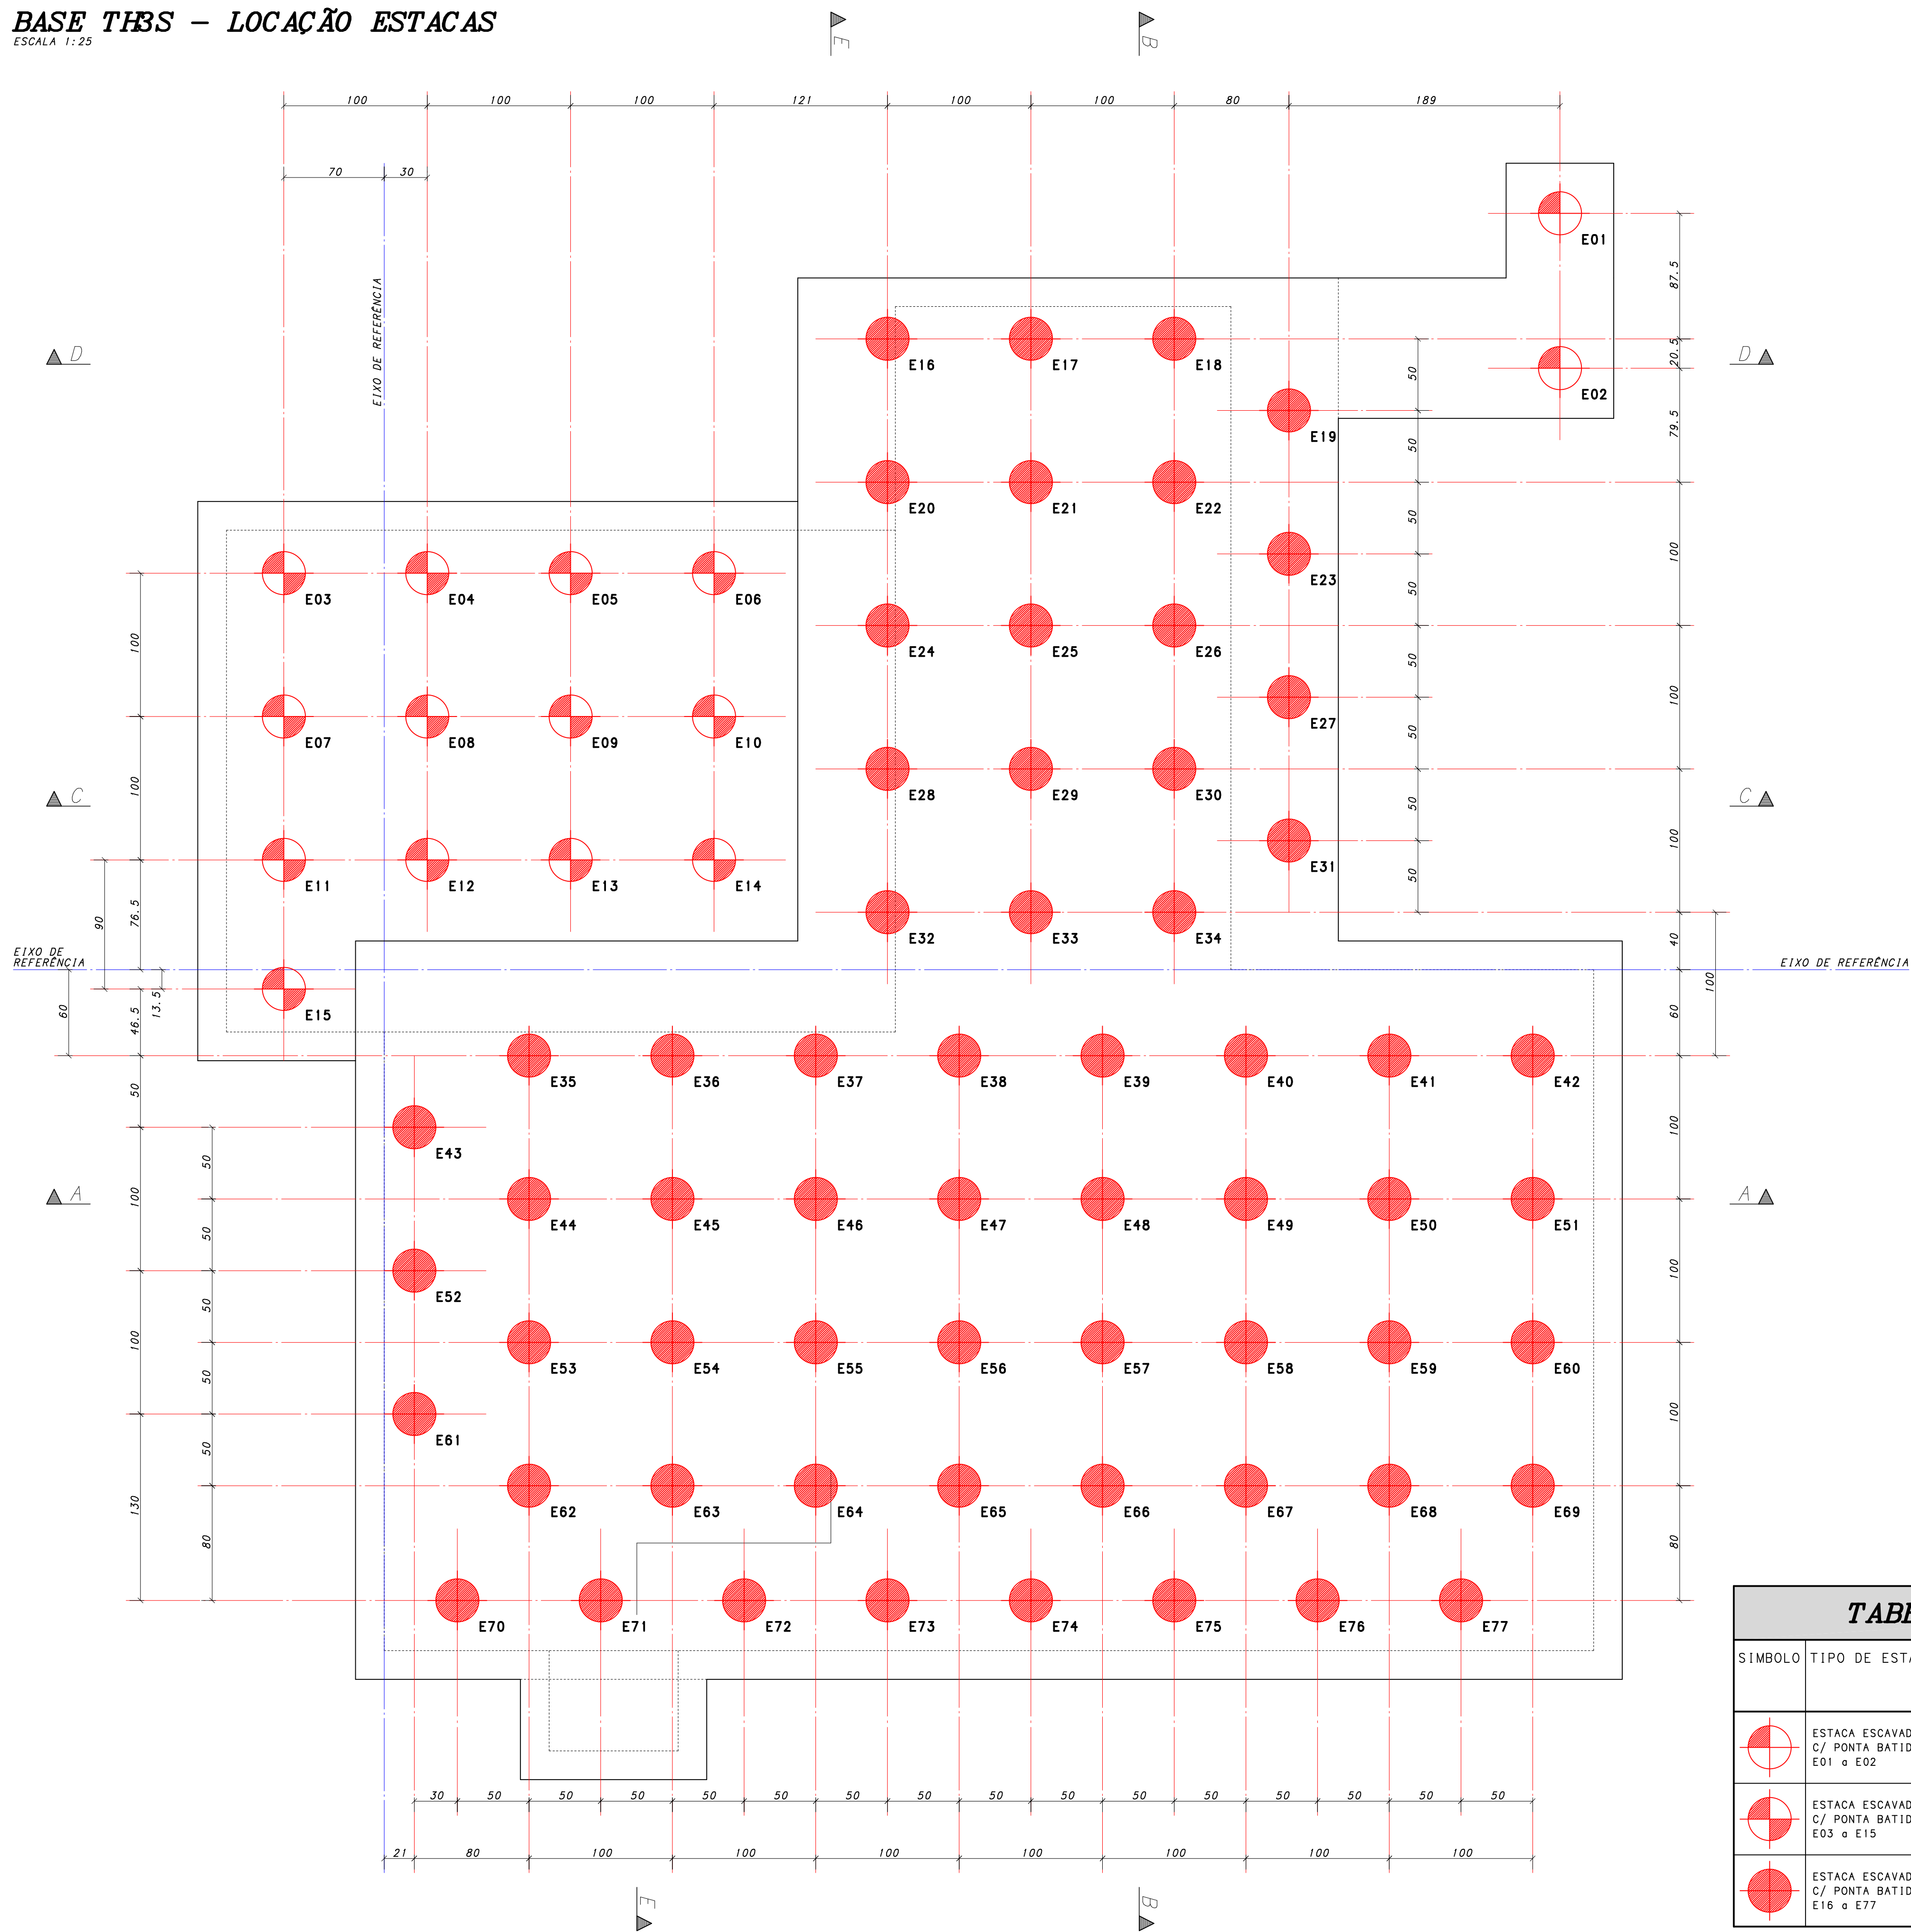


POS	BIT (mm)	QUANT	COMPRIMENTO	
			UNIT (cm)	TOTAL (cm)
ESTACA Ø40 (X77)				
1	12.5	462	600	277200
2	5	2079	132	274428

RESUMO AÇO CA 50-60			
AÇO	BIT (mm)	COMPR (m)	PESO (kgf)
60B	5	2744	423
50A	12.5	2772	2669
Peso Total		60B =	423 kg
Peso Total		50A =	2669 kg

QUANTITATIVO

ESTACA Ø40	
COMPRIMENTO DE ESCAVAÇÃO:	860 m
VOLUME DE ESCAVAÇÃO:	110 m³
VOLUME DE CONCRETO C-25:	120 m³

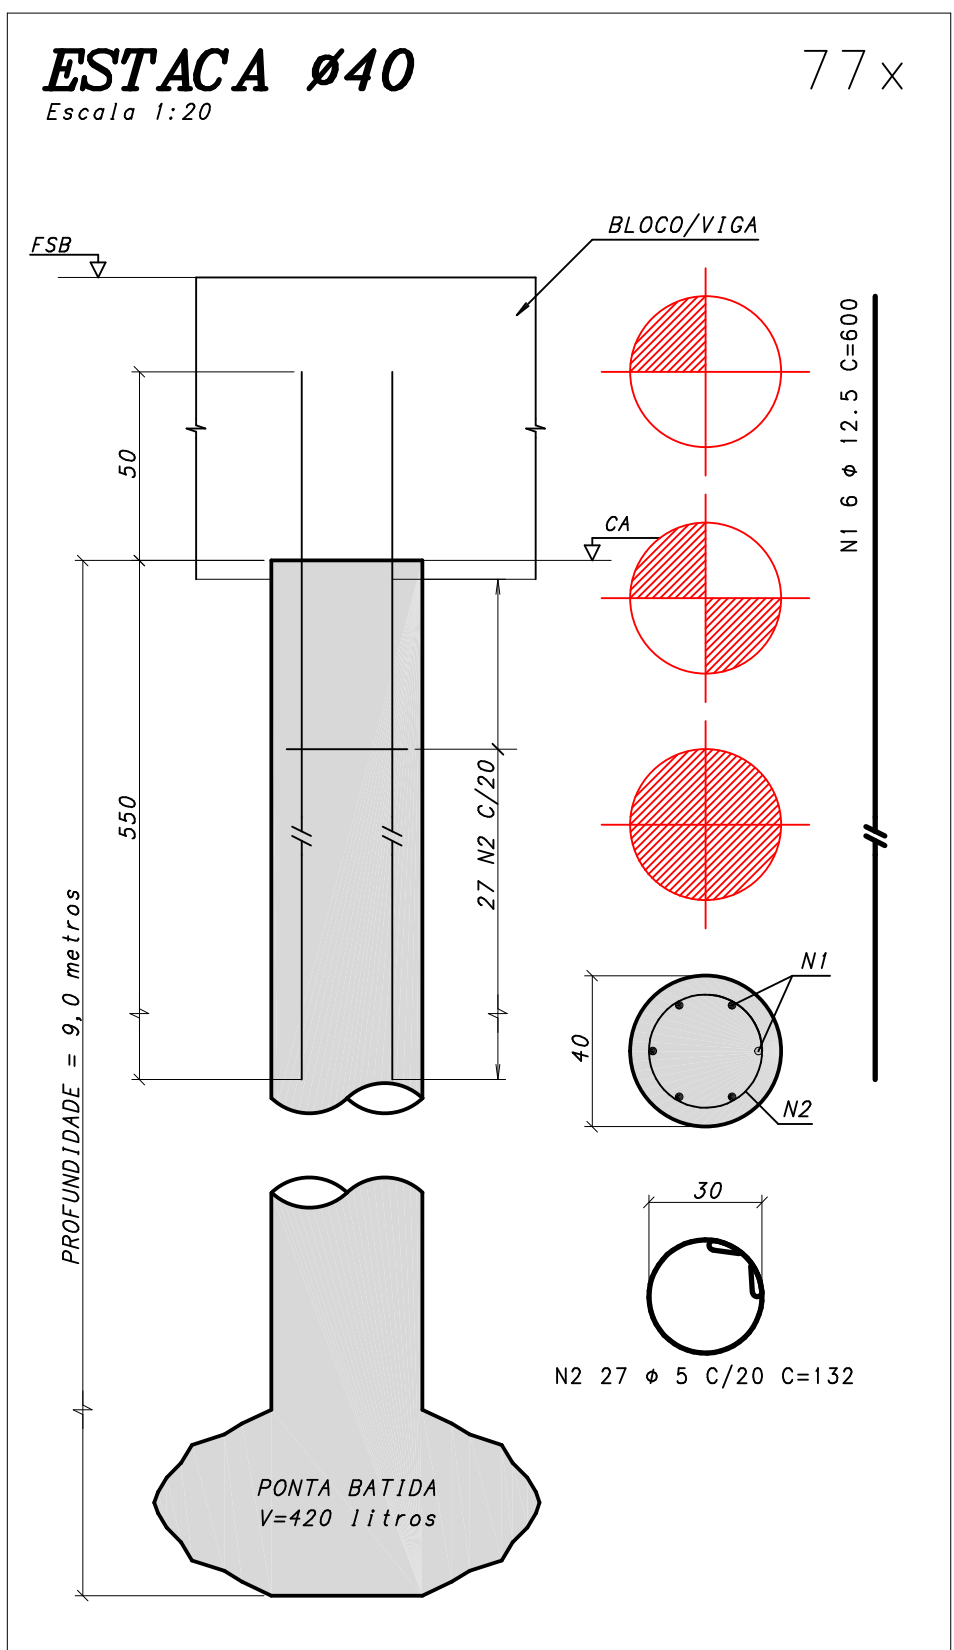


DOCUMENTOS DE REFERÊNCIA

JUARISTI - 10.TH3S.2

- 10-TH3S-2 1-4 [A1]. dwg
10-TH3S-2 2-4 [A1]. dwg
10-TH3S-2 3-4 [A1]. dwg
10-TH3S-2 4-4 [A1]. dwg
LOADS DIAGRAM (649). pdf

SONDOBASE

10199-25 Sondagem ago-2025.pdf
Ponto de Sondagem: SP-02

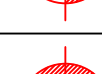TABELA RESUMO DE ESTACAS						
SÍMBOLO	TIPO DE ESTACA	DIÂMETRO (cm)	QUANTIDADE	CARGA NOMINAL COMPRESSÃO	COTA ARRASAMENTO C. A.	OBSERVAÇÃO
	ESTACA ESCAVADA C/ PONTA BATIDA E01 a E02	Ø 40	2 x	25 tf	-0,65	Profundidade 9,0 metros
	ESTACA ESCAVADA C/ PONTA BATIDA E03 a E15	Ø 40	13 x	25 tf	-1,55	Profundidade 9,0 metros
	ESTACA ESCAVADA C/ PONTA BATIDA E16 a E77	Ø 40	62 x	25 tf	-2,35	Profundidade 9,0 metros

8- O NÍVEL, 0,00 CORRESPONDE AO NÍVEL DO PISO INTERNO ACABADO.	
9- NAS ESTACAS, O COMPROMENTO DE 9,0 metros É UTILIZADO E DEVE SER CONSIDERADO A PARTIR DA COTA DE ARRASAMENTO (CA).	
10- TODO MATERIAL USADO NA ESTRUTURA DEVEVA TER CONTROLE DE QUALIDADE CONFORME ABNT	
11- LIDE DO CONCRETO PARA CARGAS DE 28 DIAS	
12- FIJO NAS PEGAS DE CONCRETO SO O INDICADO	
CONCRETO:	
ESTACAS:	
DEMAIS PEGAS:	
MÓDULO ELAST. CONCRETO:	
BR-31 CFS	

REV	DATA	DESCRIÇÃO
C	22/12/2025	QUANTIDADE DE ESTACAS
B	21/12/2025	EMIÇÃO FINAL
A	15/12/2025	EMIÇÃO INICIAL

CONTRATO	E5377
DATA INICIAL	15/DEZ/2025
ESCALA	INDICADO
DESENHO	
SALVADOR NOB0A	
APROVADO	

CLIENTE	
CORRETADEIRA	
TÍTULO DESEJADO	FUNDAÇÃO LOCACÃO E ARMADURA DAS ESTACAS
LOCAL	CRAVINHOS - SP

ETEC ENGENHARIA CIVIL
 Rua W. Joaquim Romel, 397 - Ribeirão Preto/SP
 Fone: (16) 3655-8989
 Fax: (16) 3655-8989
 e-mail: etec@etec.com.br

RESPONSABILIDADE TÉCNICA
PROJETO DE CONCRETO ARMADO

EDSON SEIXAS FORNI
ENG. CIVIL, EPPR/76
CREA: 9806-55.564-3

NUMERO DA FOLHA
C-01

REVISÃO: C