
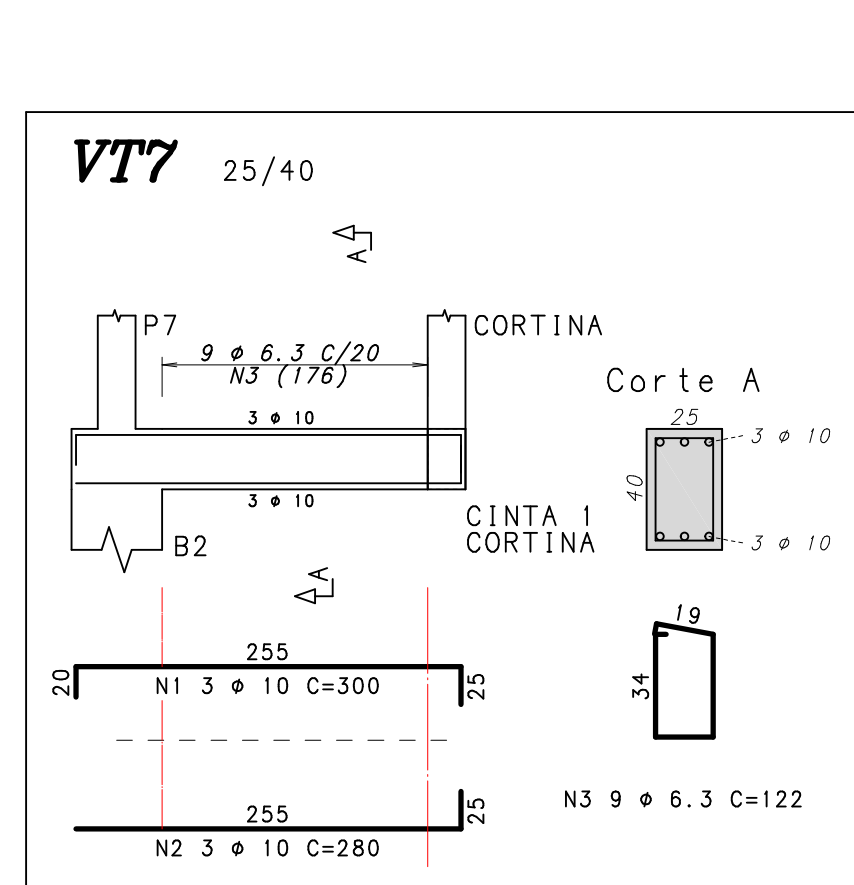
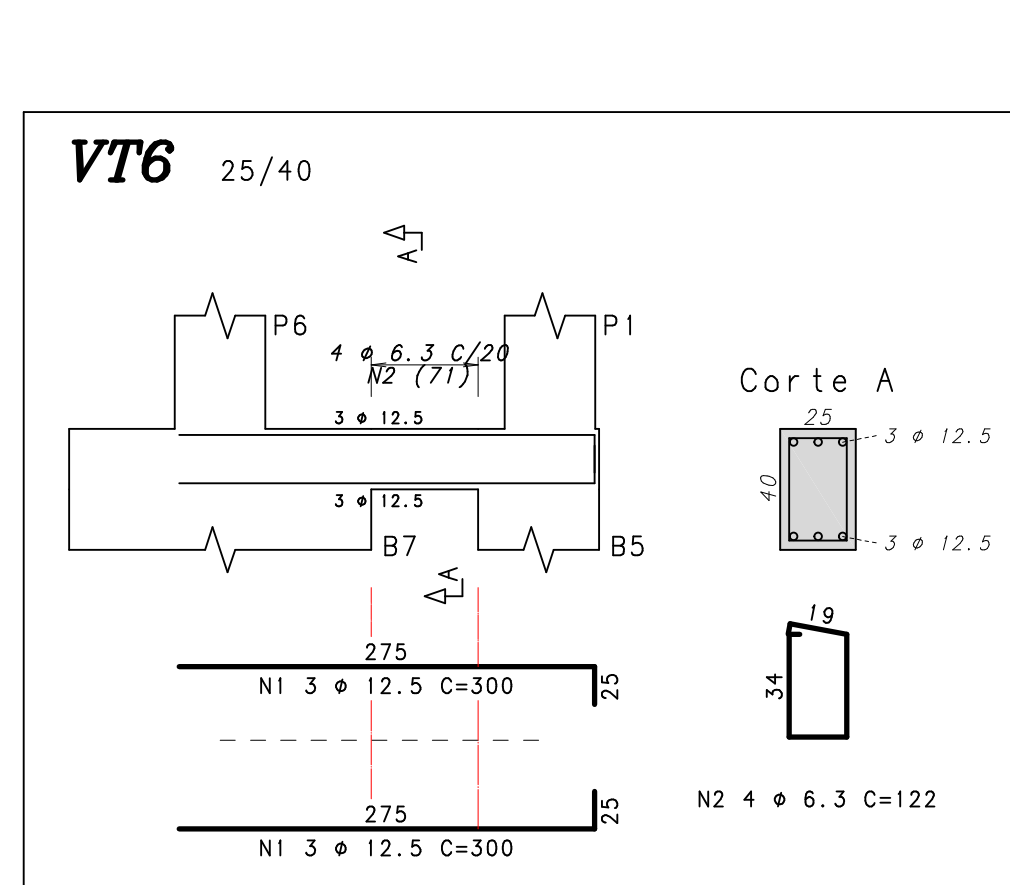
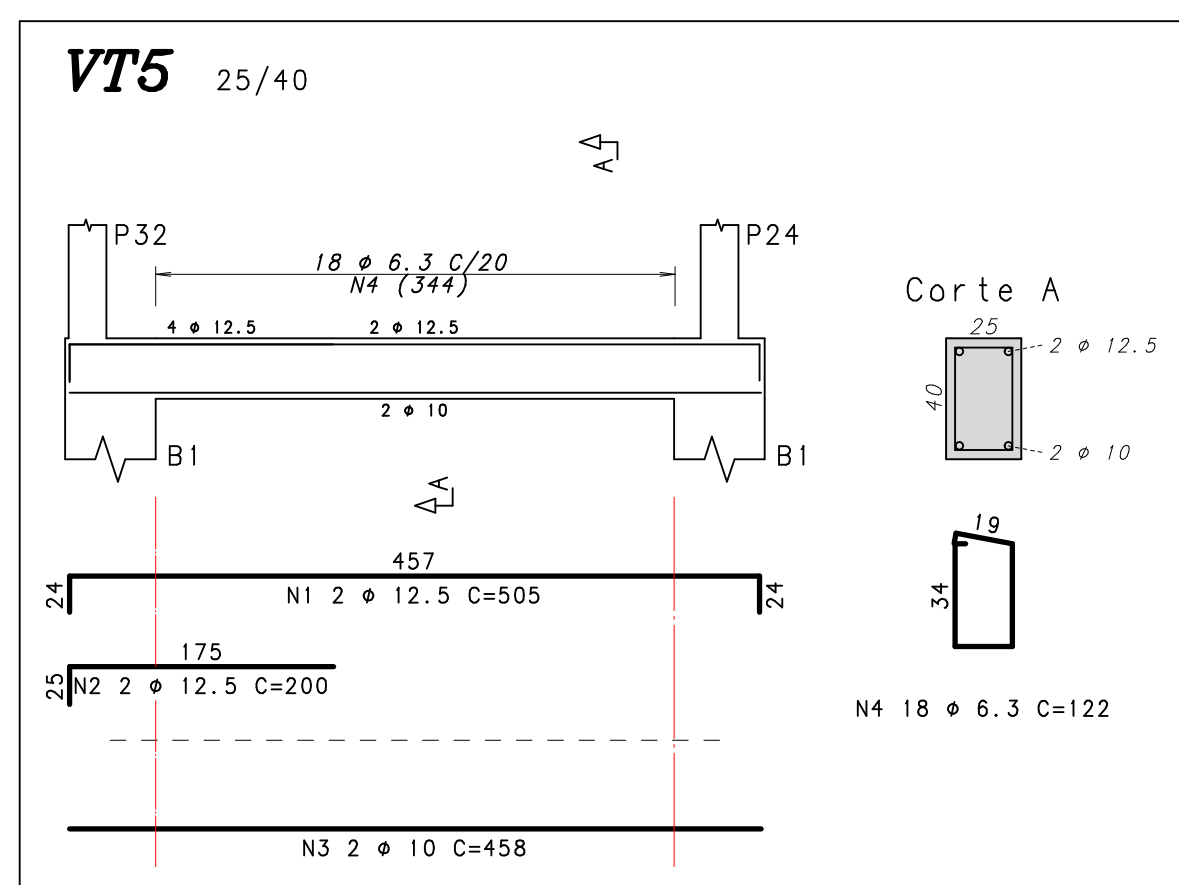
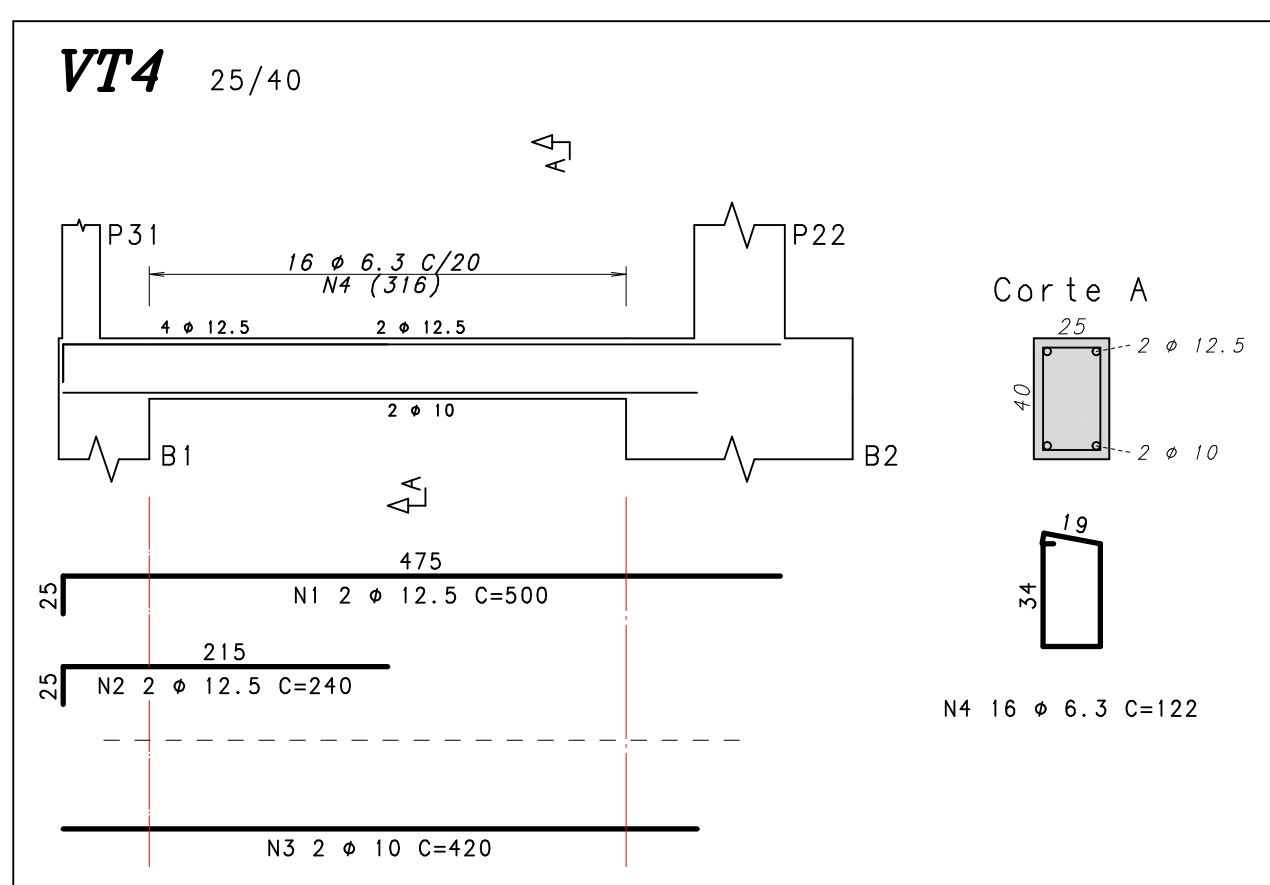
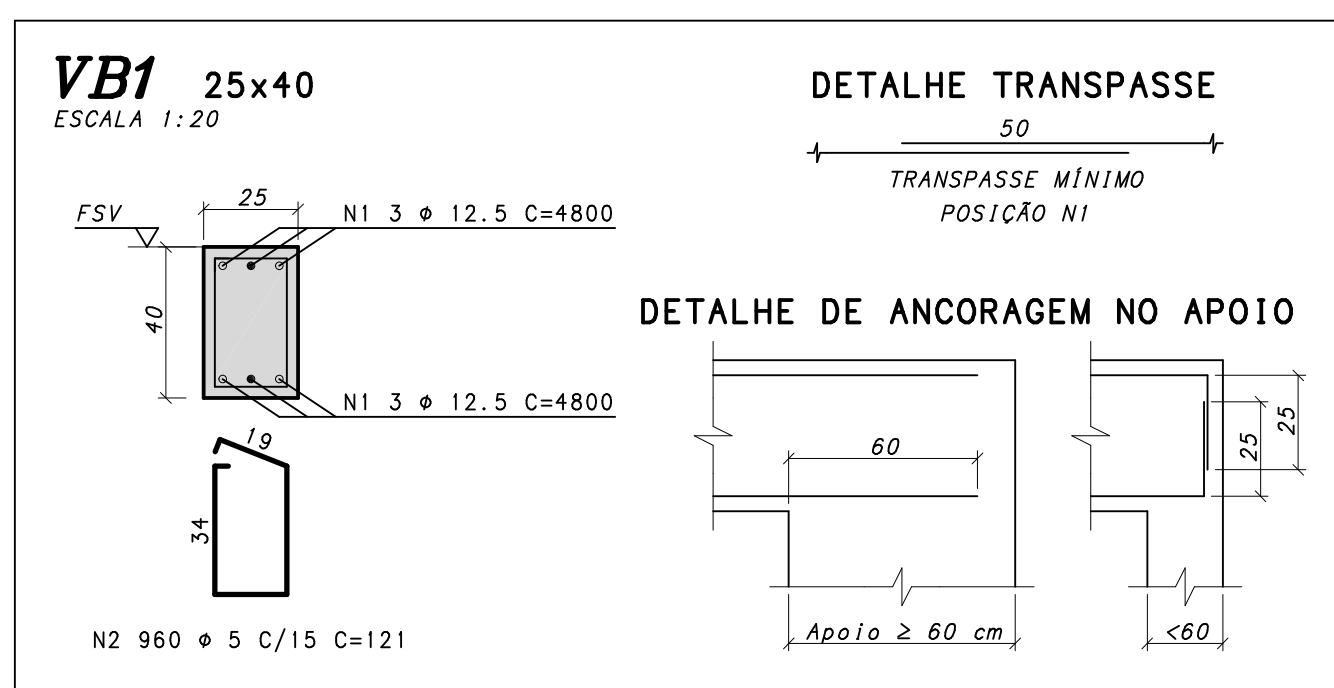
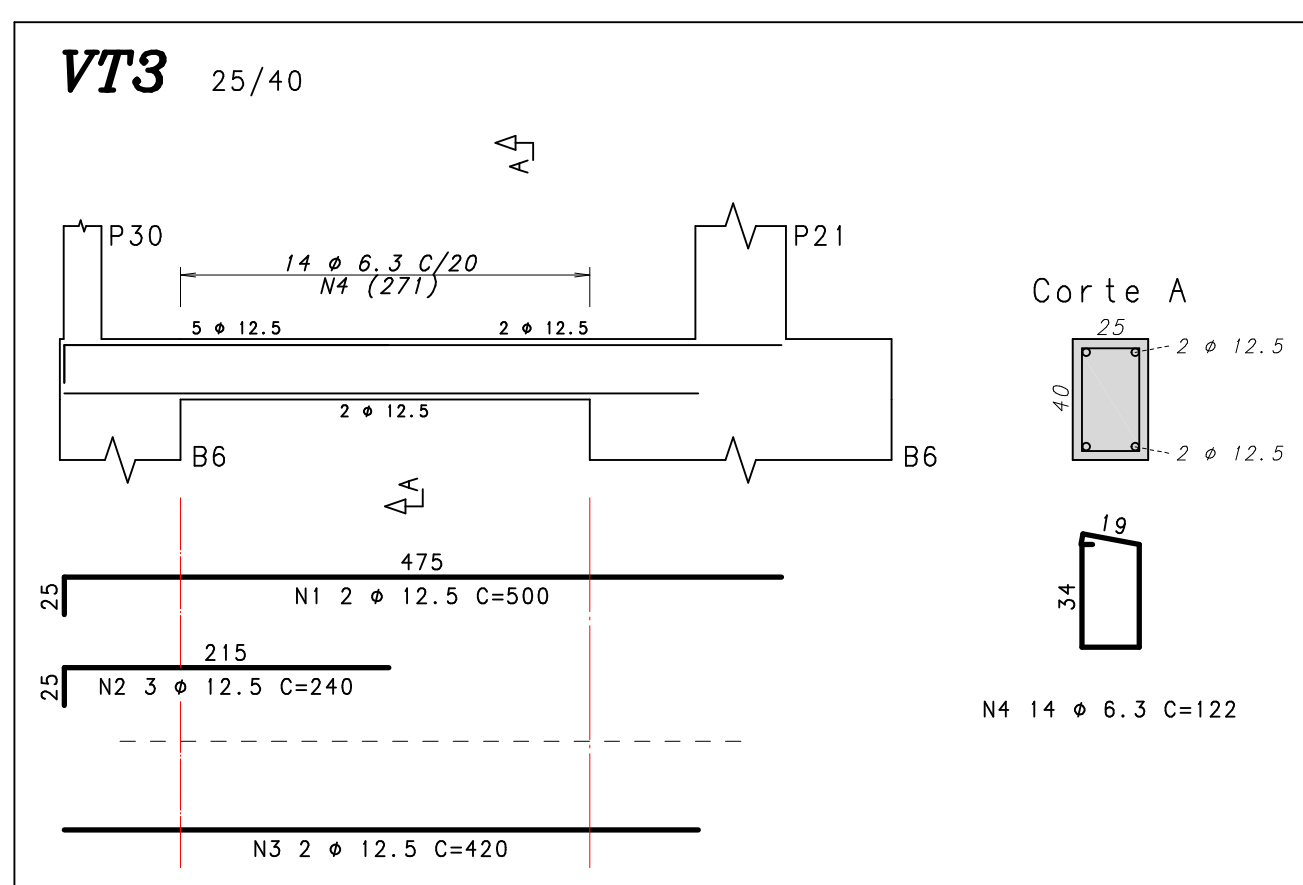
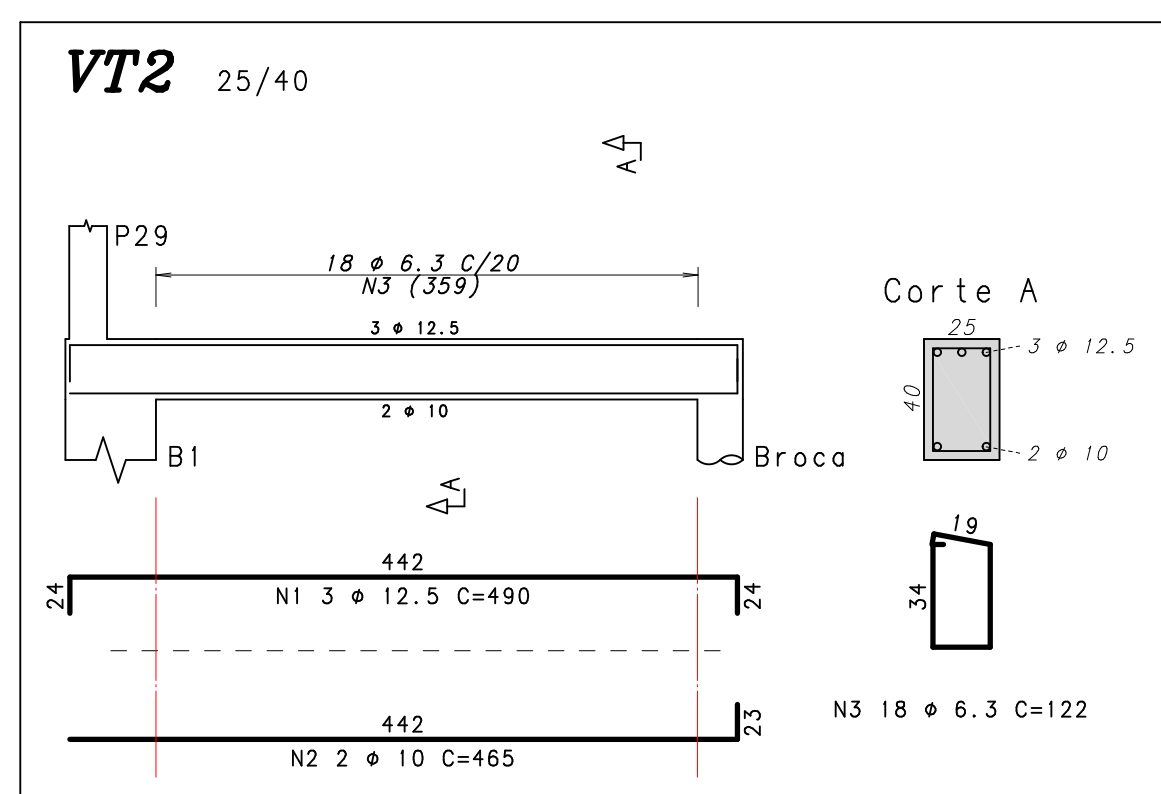
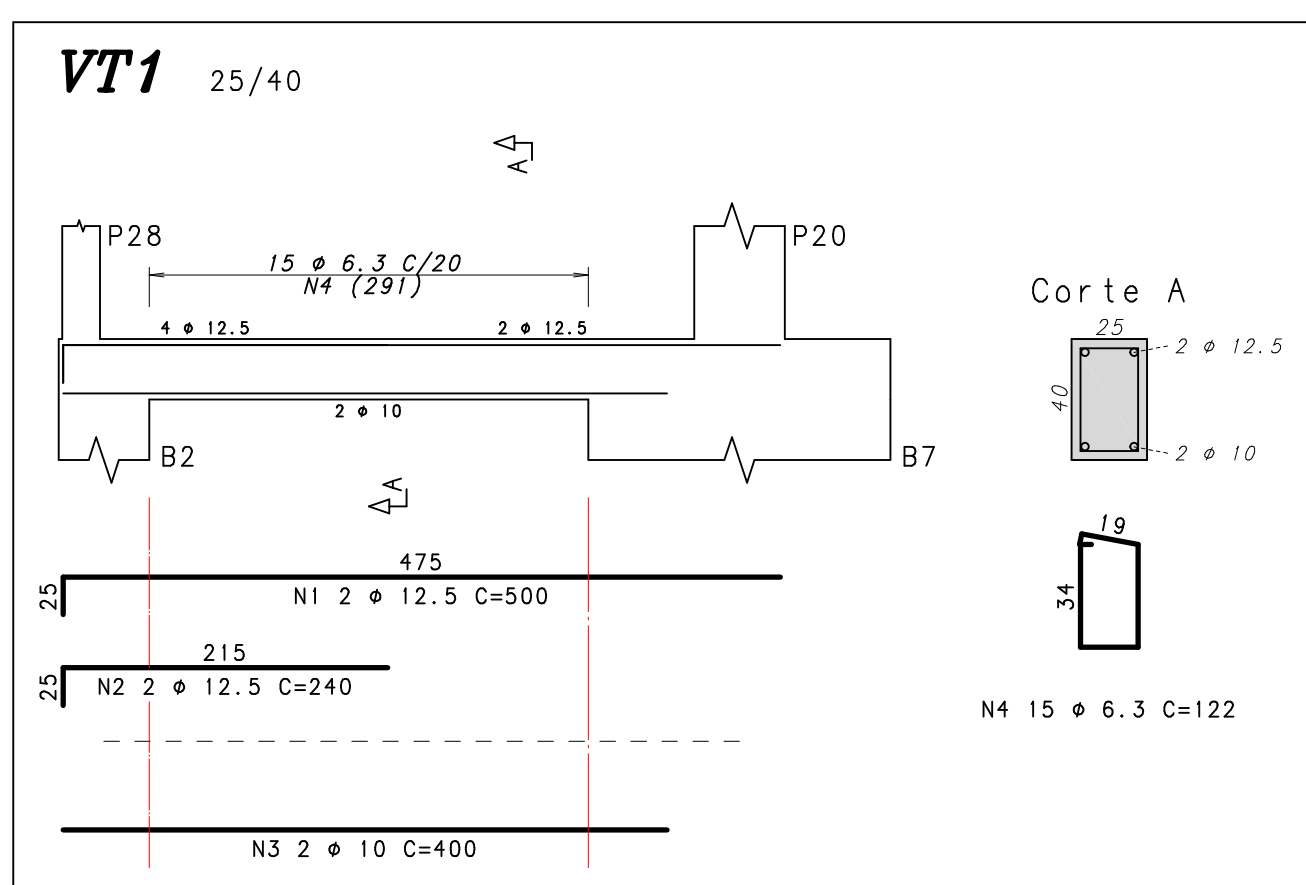
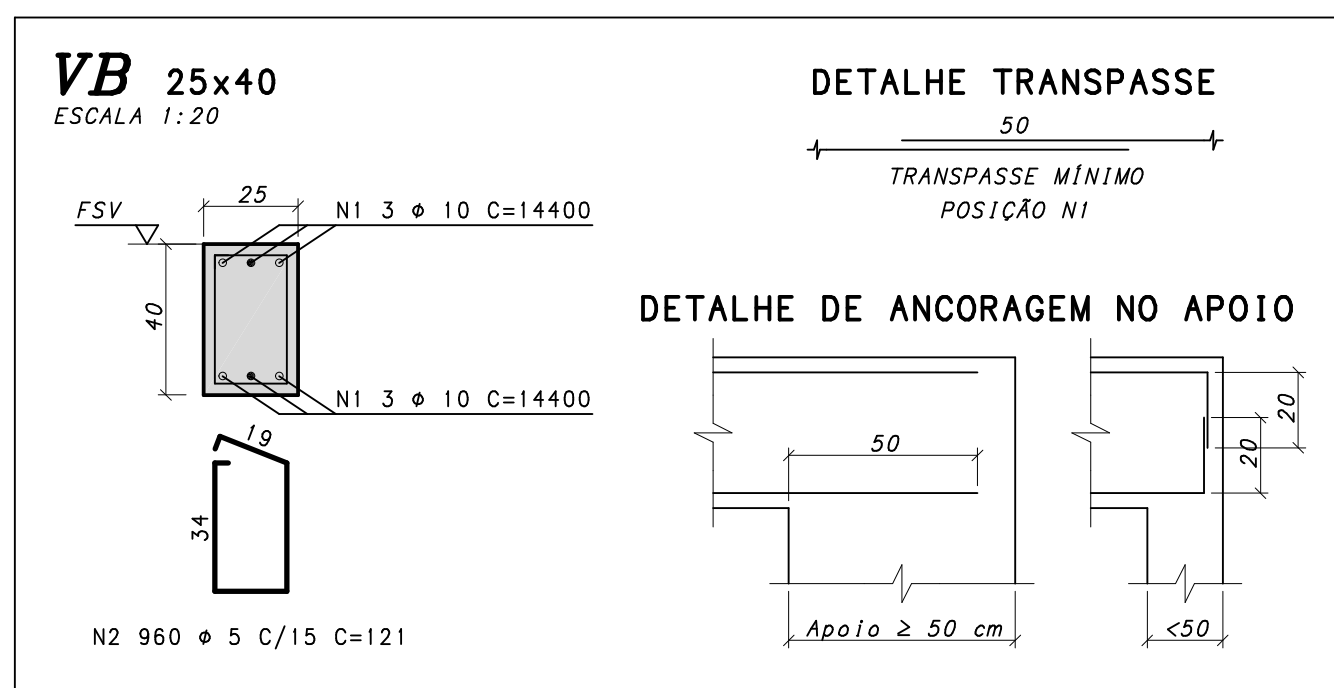
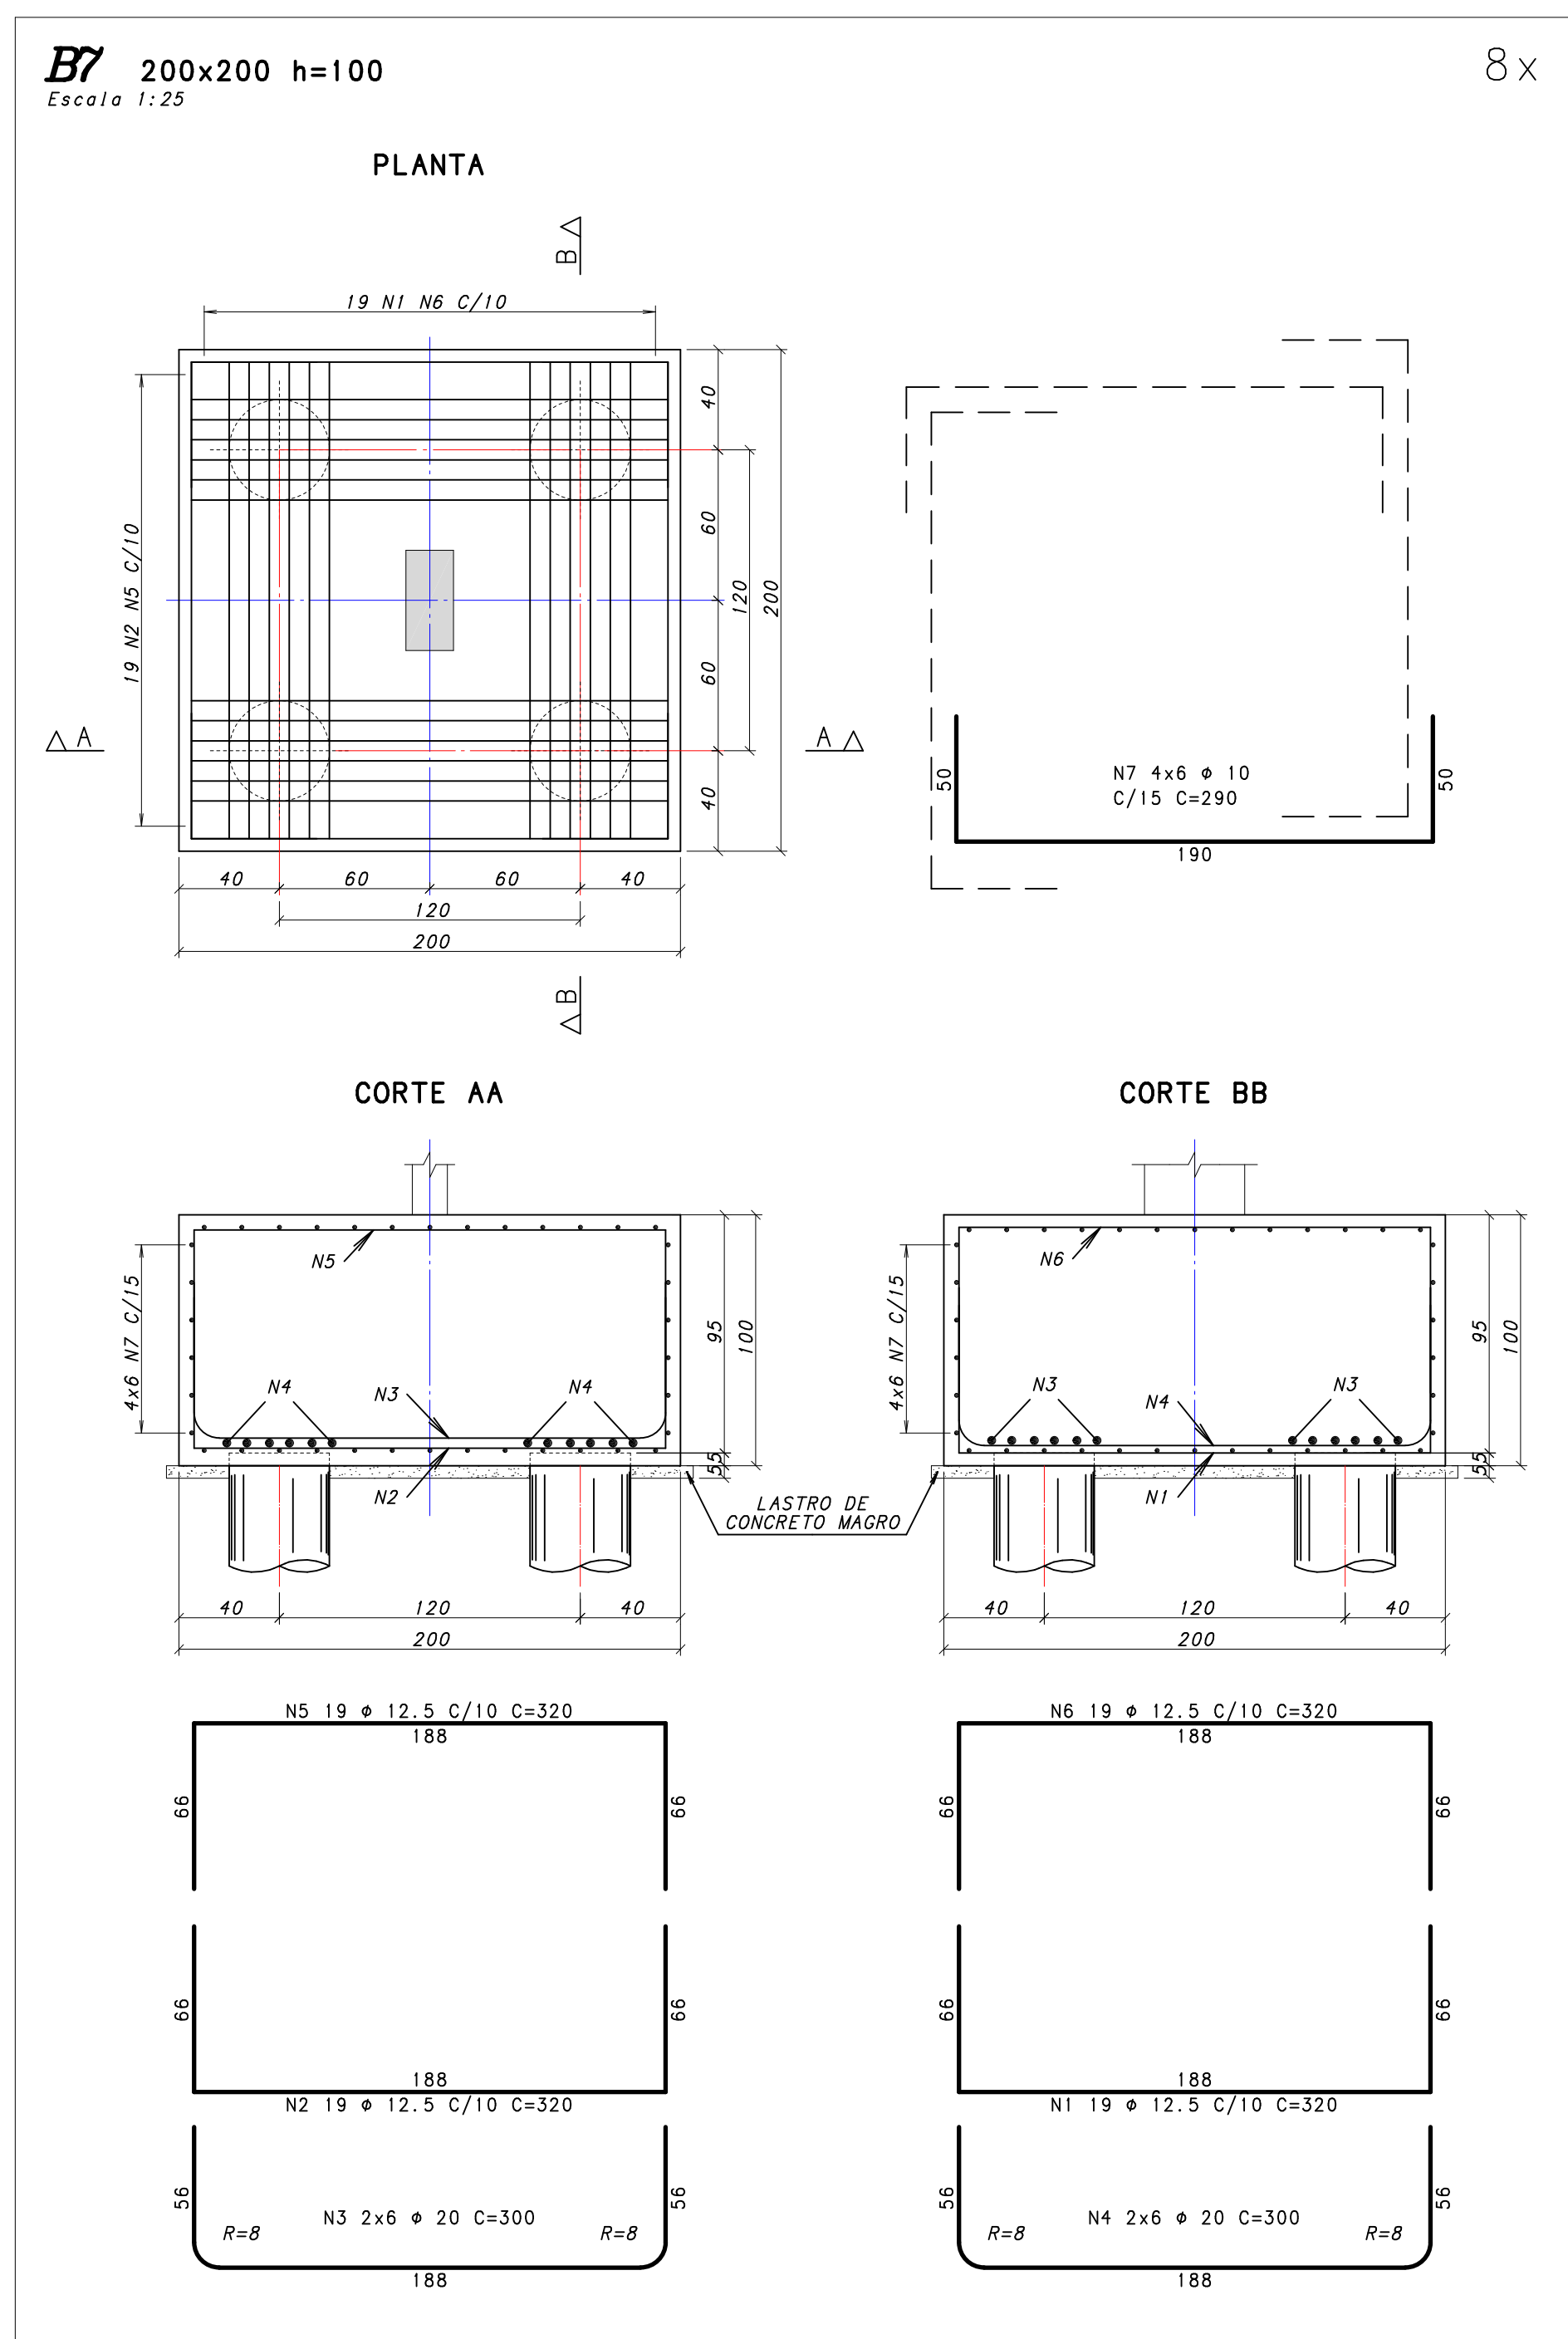
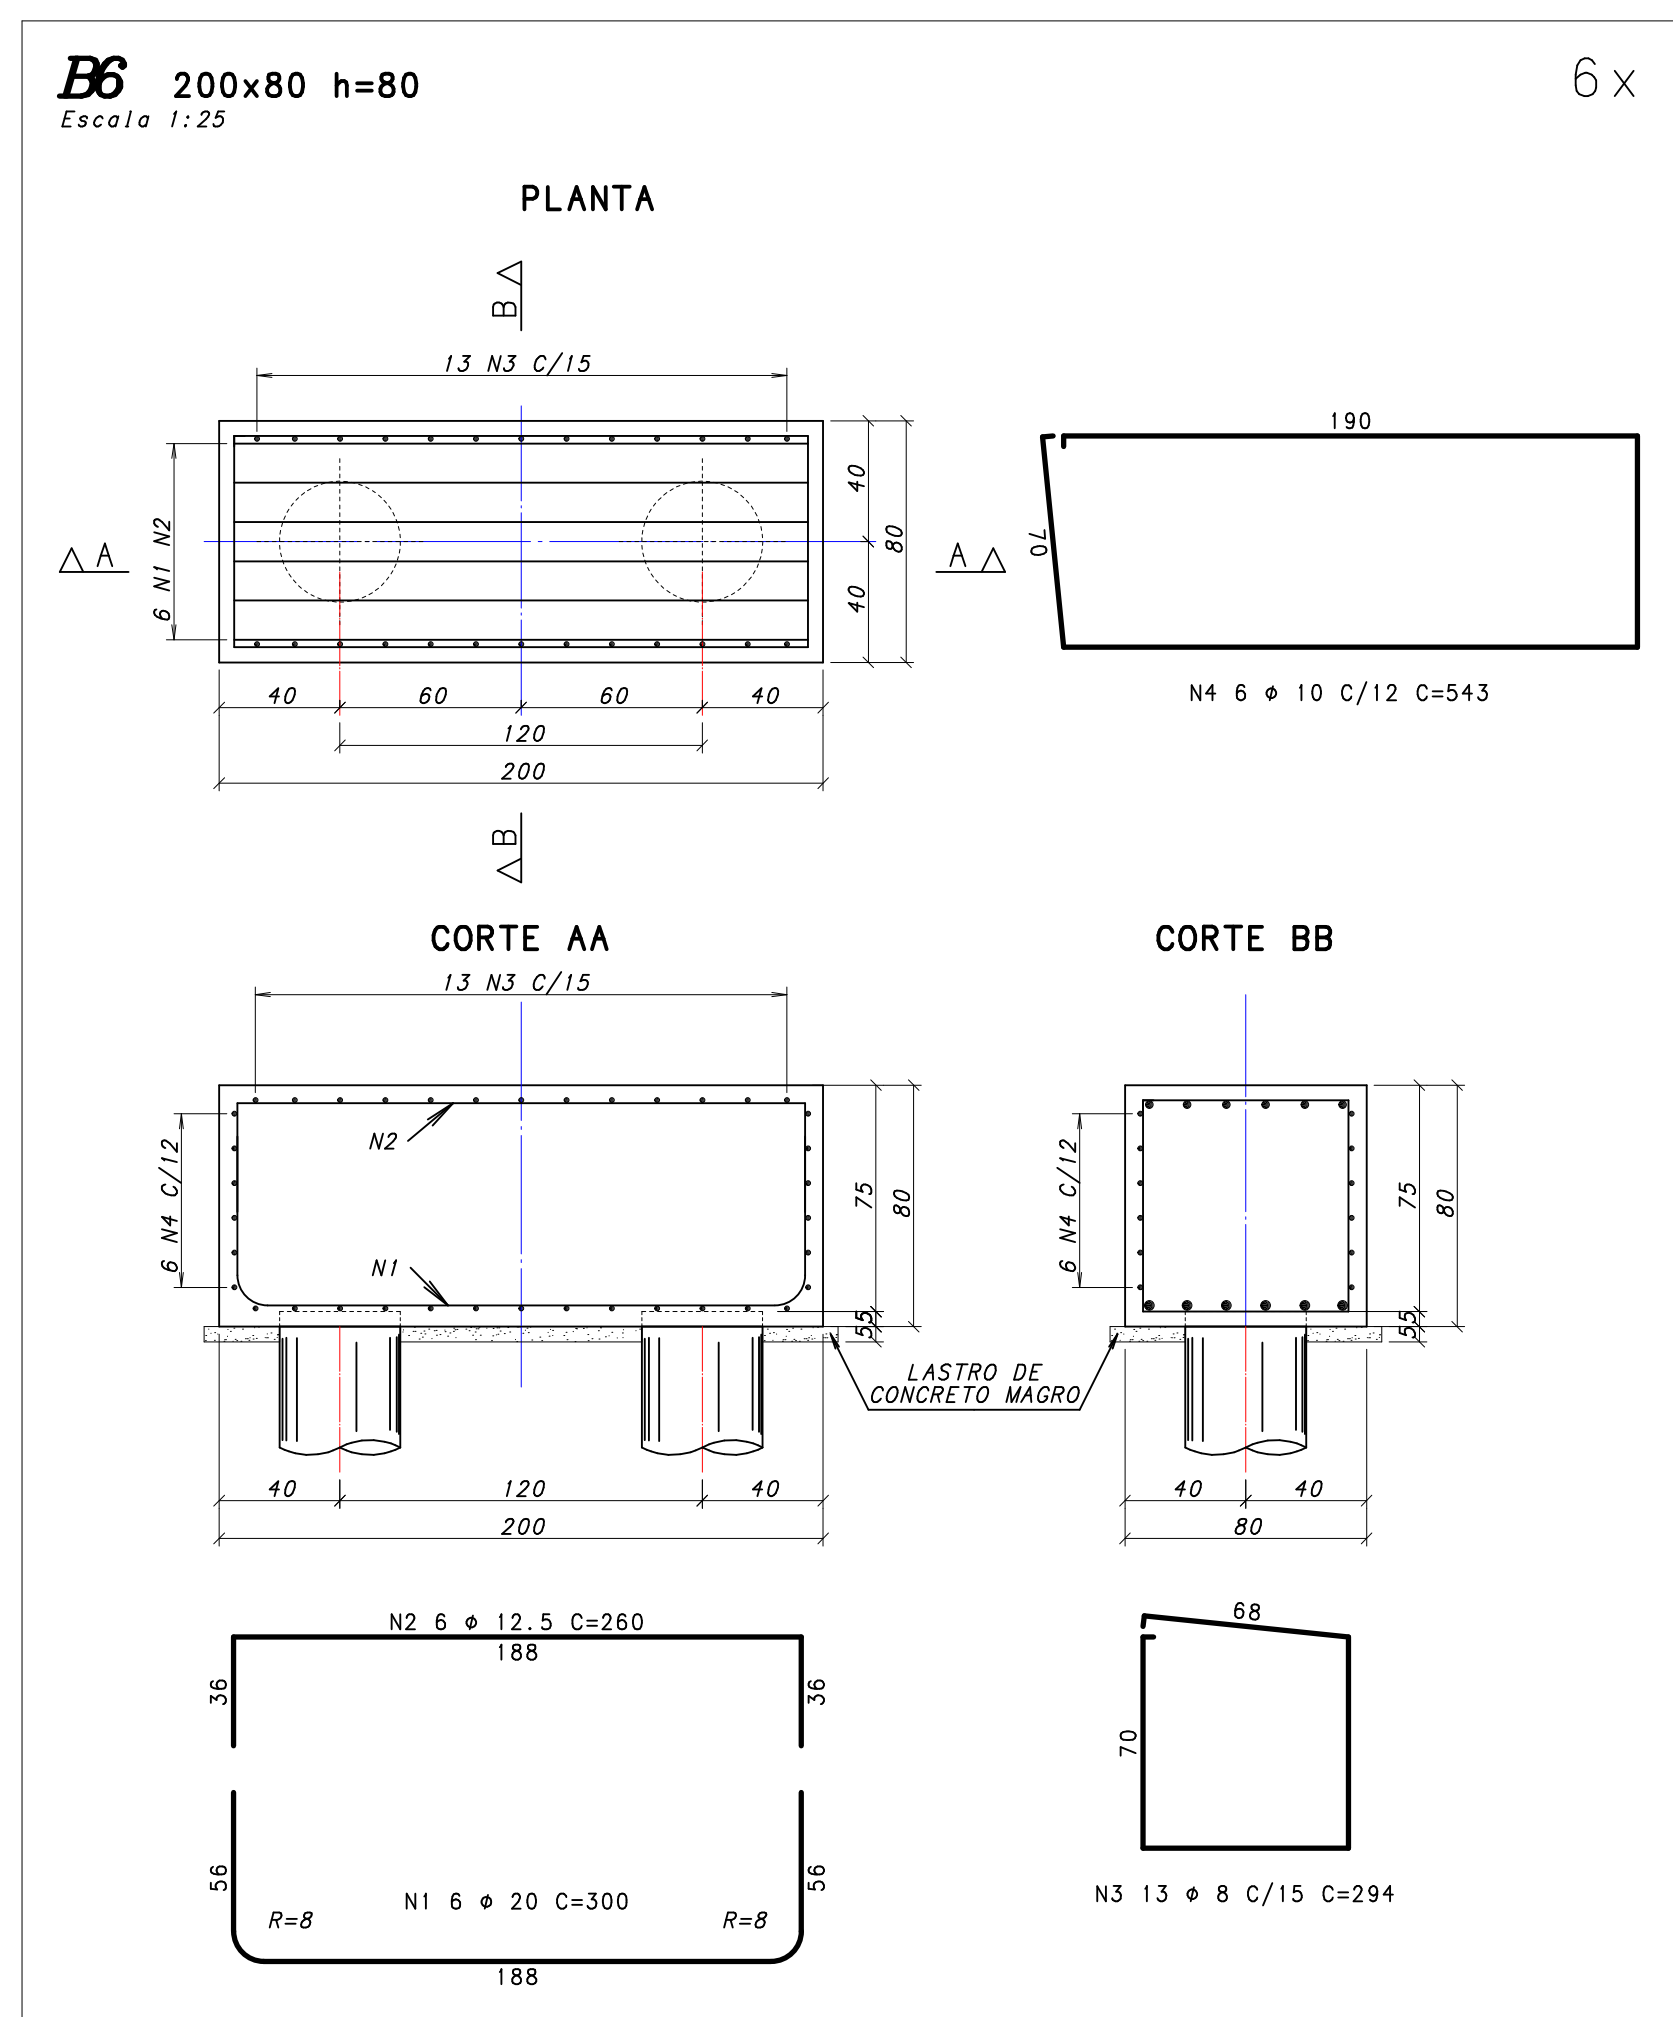
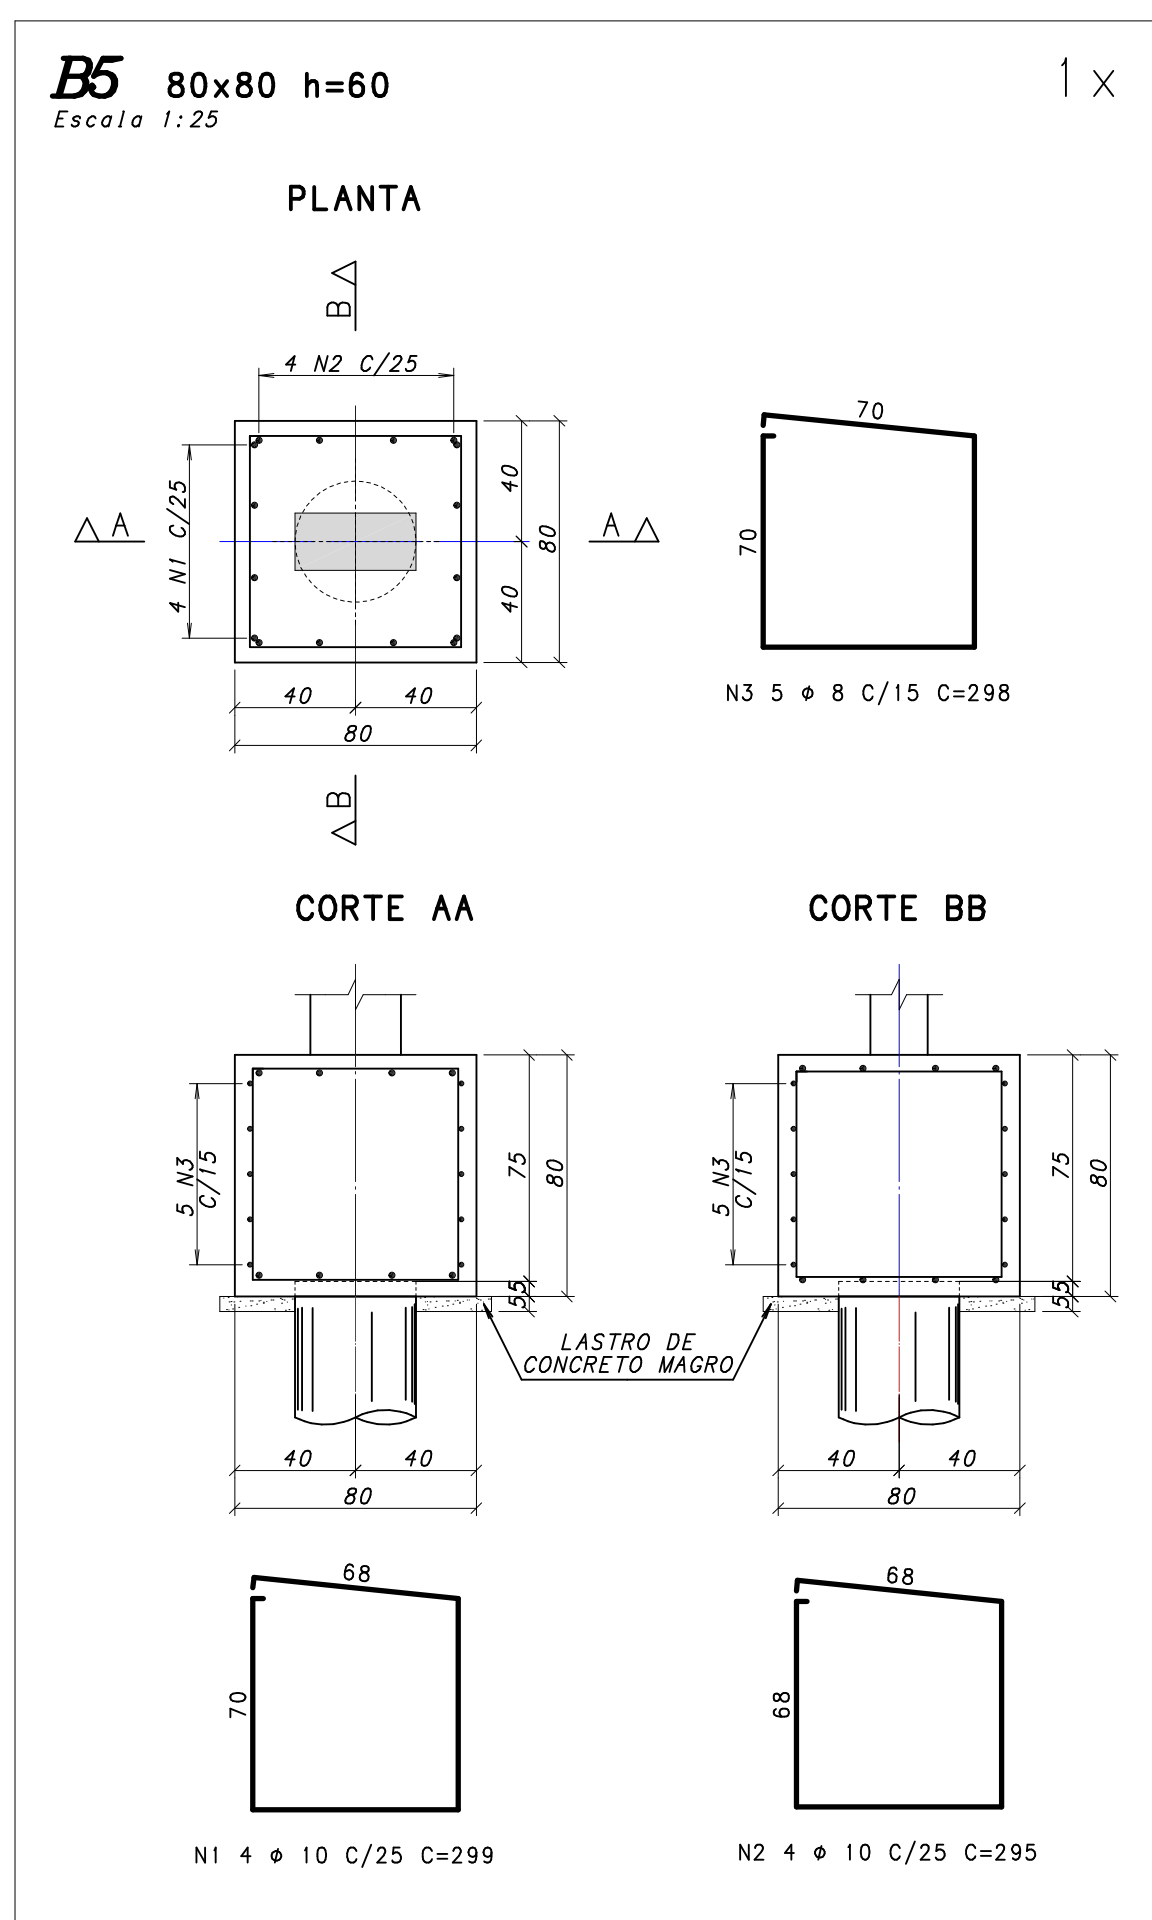
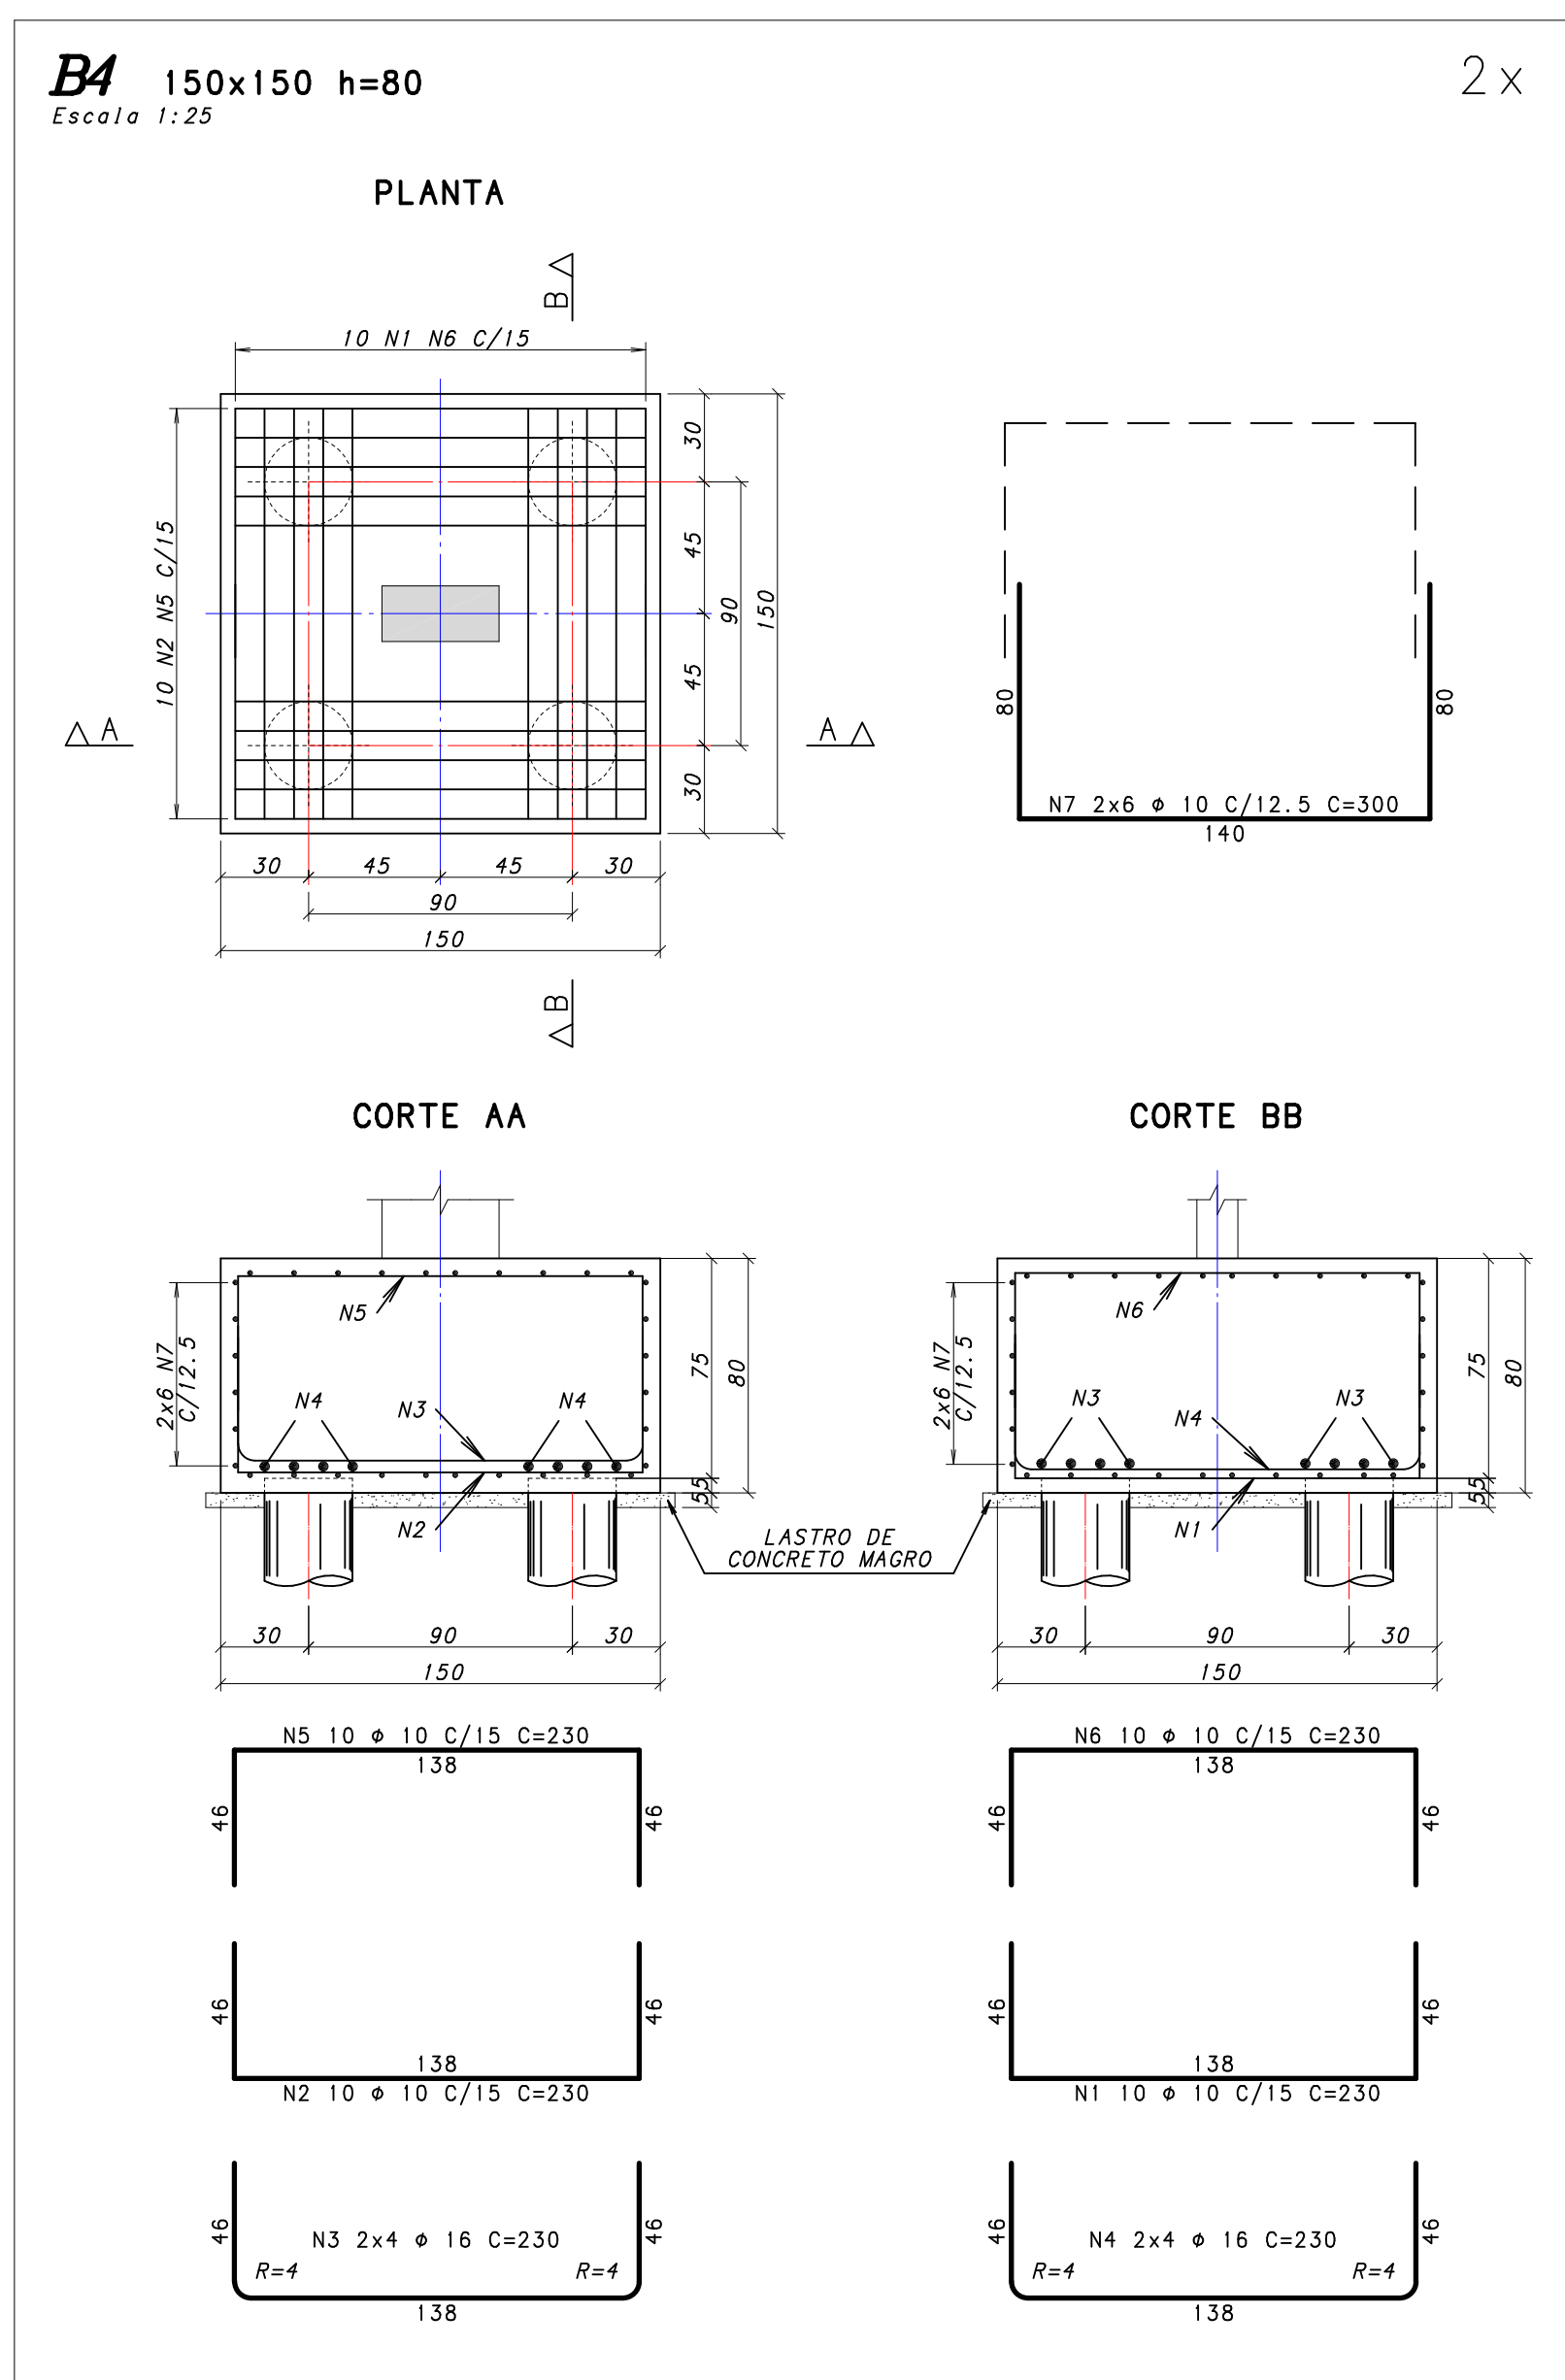
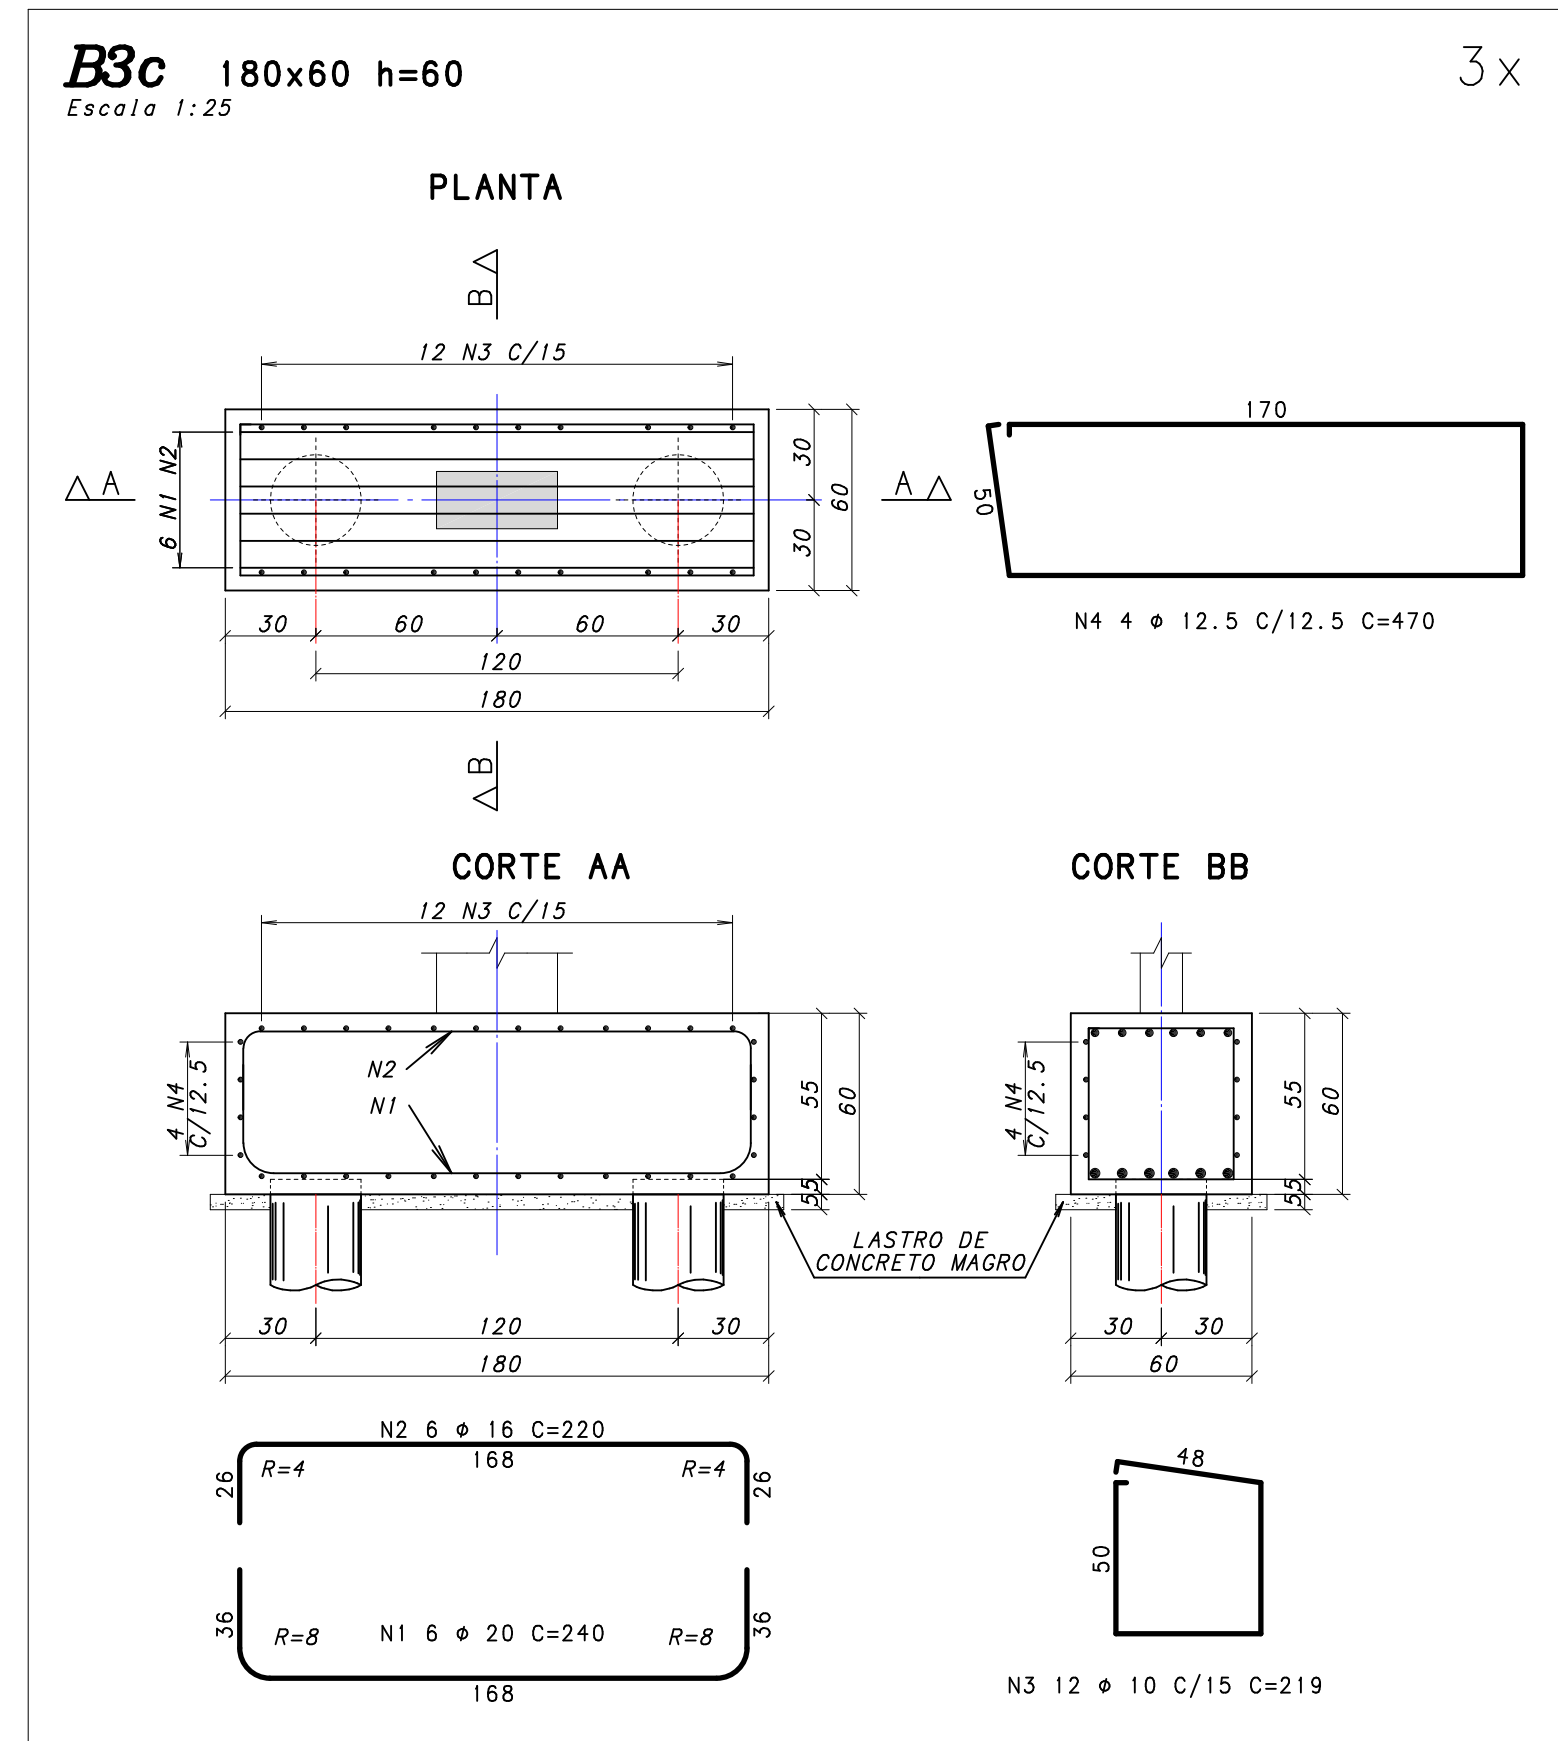
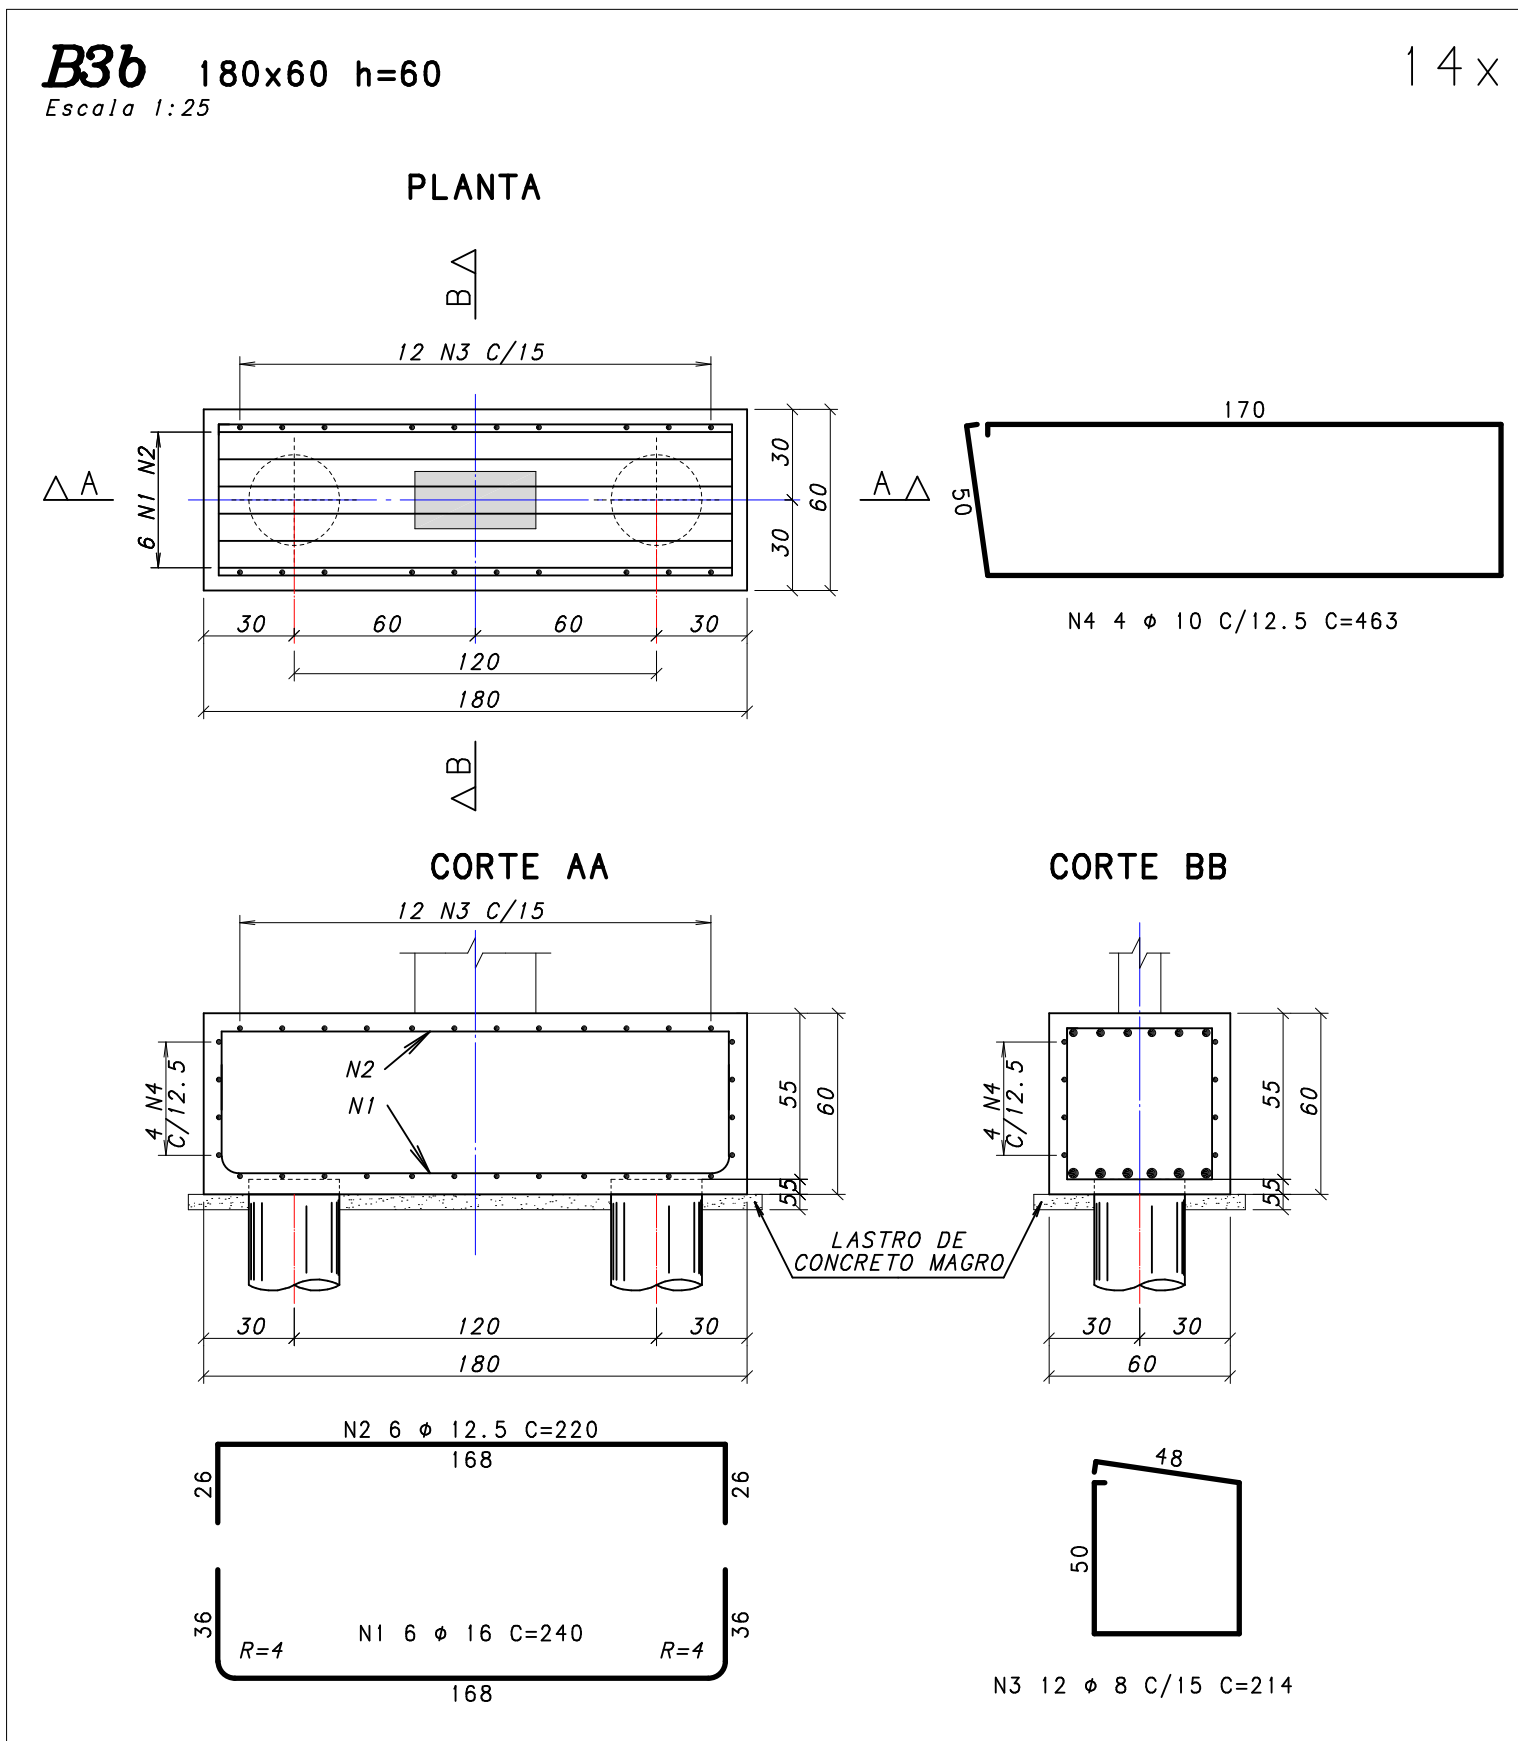
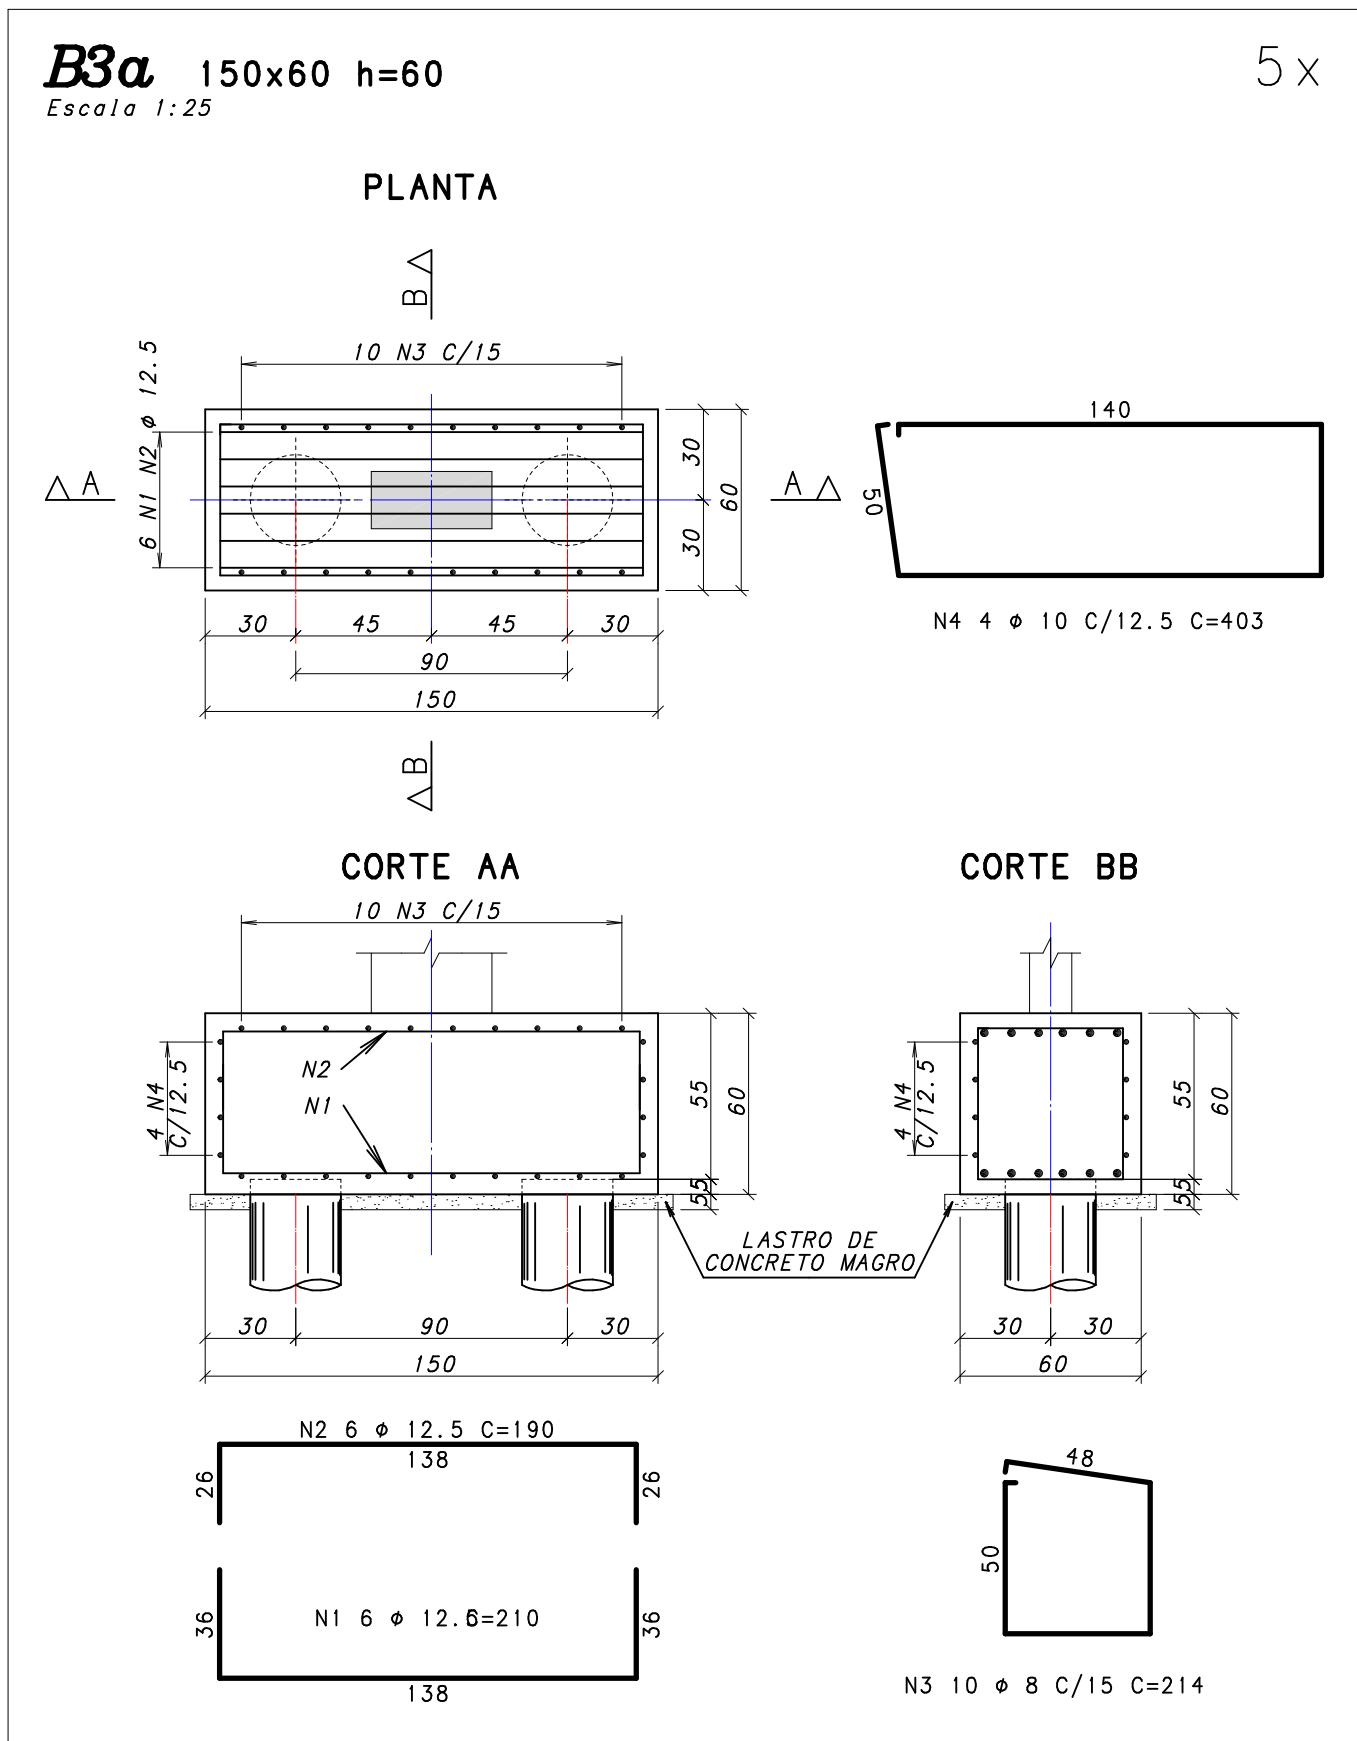
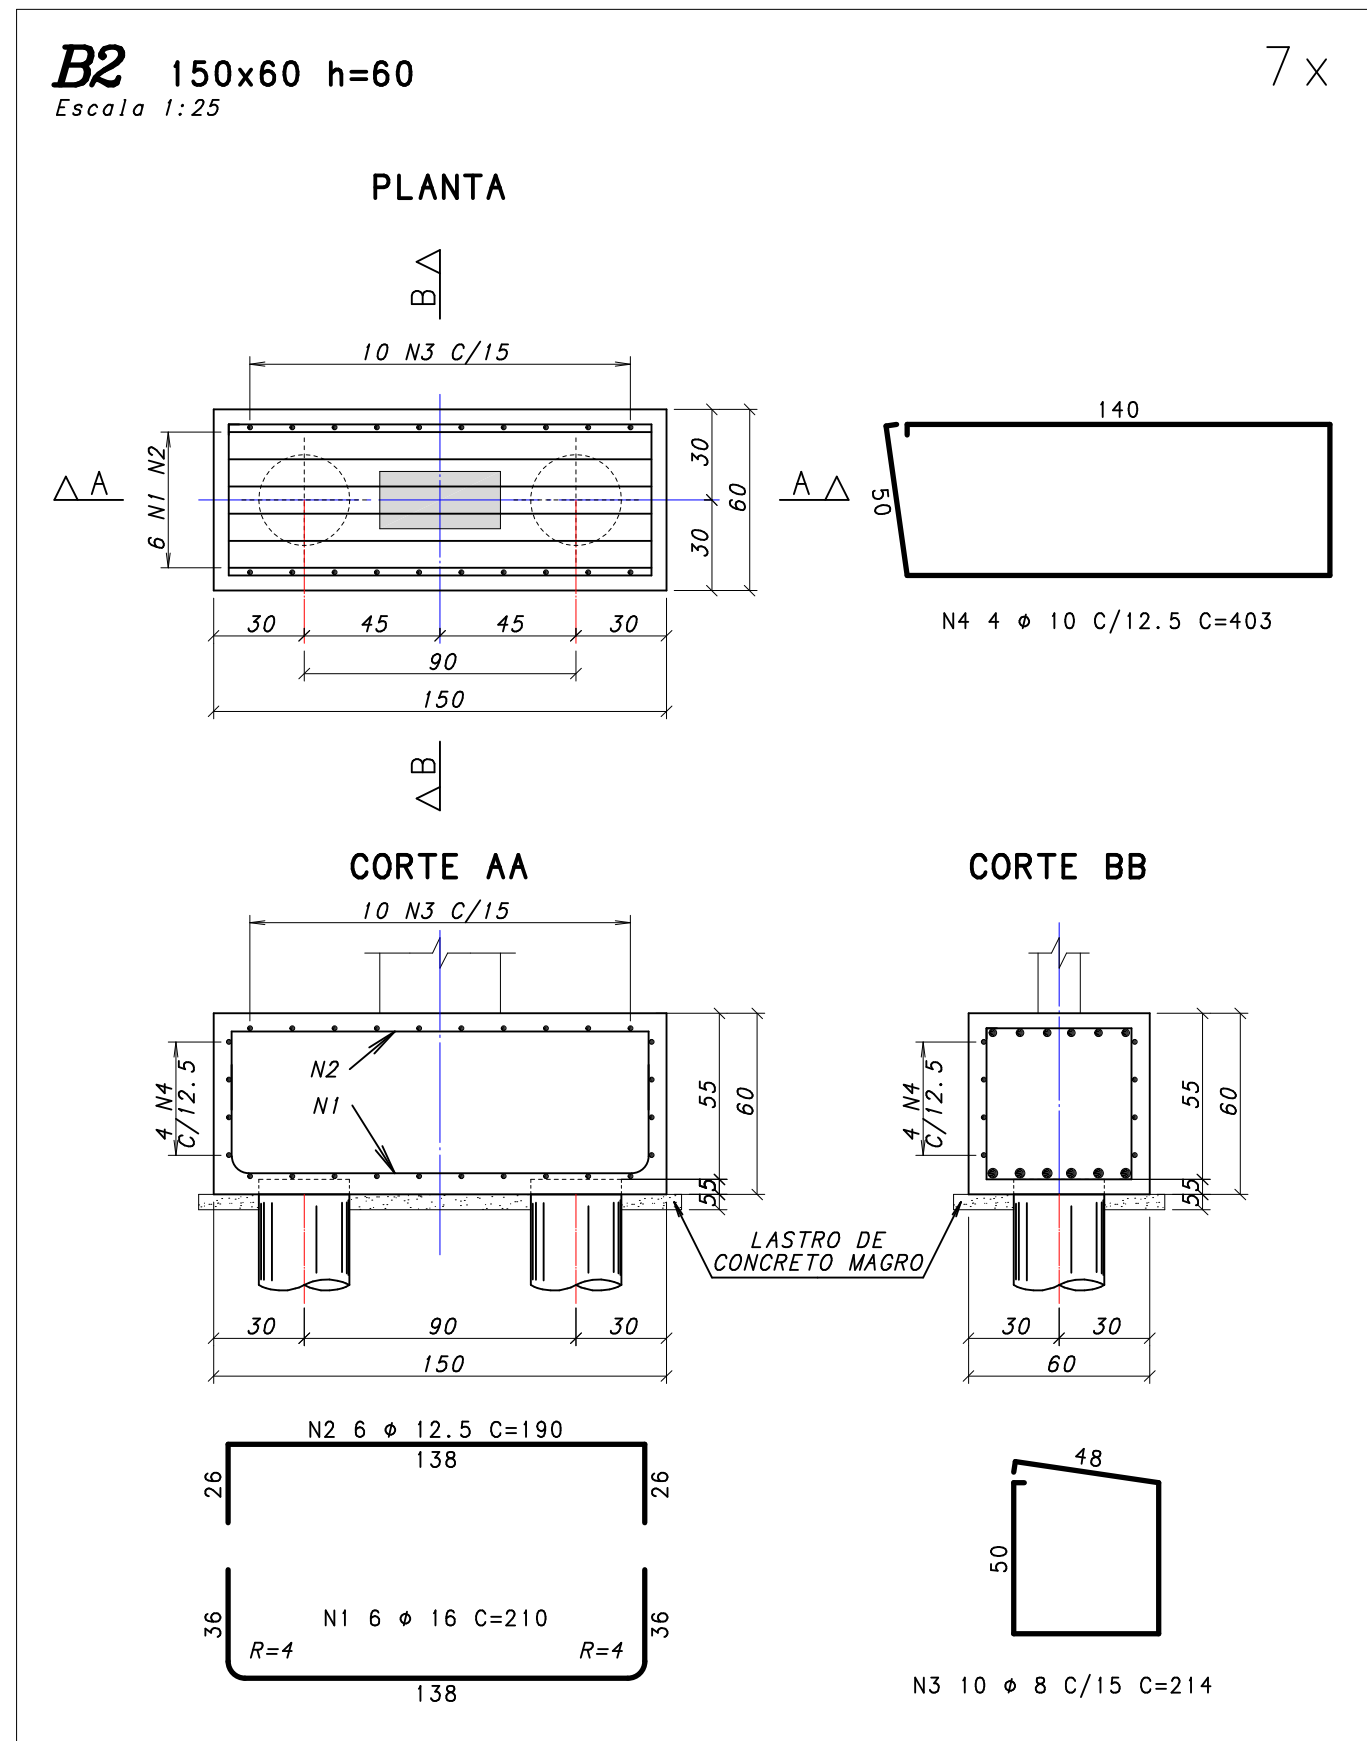


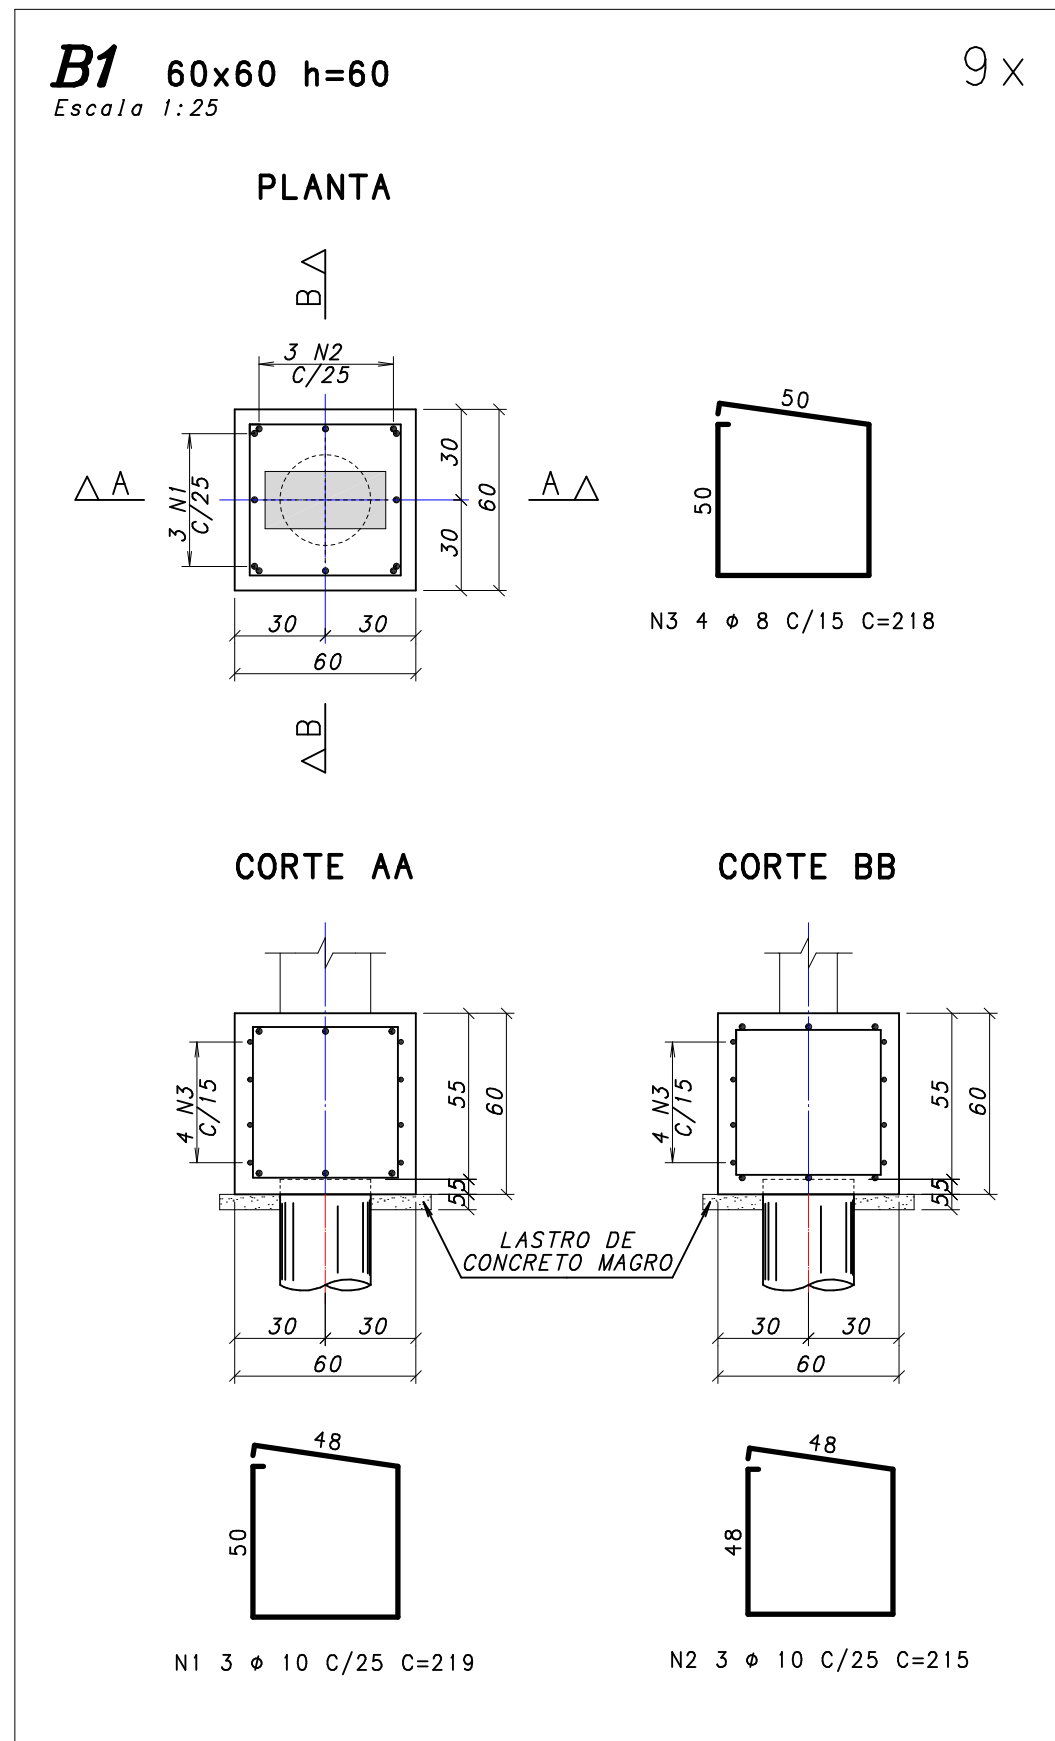

POS	BIT	QUANT	COMPRIMENTO	UNIT	TOTAL
(mm)	(X)		(cm)	(cm)	
B1	(X9)				
1	10	27	219		5913
2	16	27	215		3805
3	8	36	218		7848
B2	(X7)				
1	18	42	210		8820
2	12.5	42	210		7880
3	8	70	214		14980
4	10	28	403		11284
B3a	(X5)				
1	12.5	30	210		6300
2	16	30	210		6300
3	8	50	214		10700
4	10	20	403		8060
B3b	(X14)				
1	16	84	240		20160
2	16	84	220		18480
3	8	168	214		35952
4	10	58	463		25928
B3c	(X3)				
1	20	18	240		4320
2	16	18	220		3960
3	10	36	219		7884
4	12.5	12	470		5640
B4	(X2)				
1	20	20	230		4600
2	10	20	230		4600
3	16	16	230		3680
4	16	16	230		3680
5	10	20	230		4600
6	10	20	230		4600
7	10	24	300		7200
B5					
1	10	4	299		1196
2	10	4	299		1196
3	5	4	299		1196
B6	(X6)				
1	12.5	36	300		10800
2	12.5	36	280		9360
3	10	78	294		22932
4	10	36	543		19548
B7	(X8)				
1	12.5	152	320		48640
2	12.5	152	320		48640
3	10	96	300		28800
4	20	96	300		28800
5	12.5	152	320		48640
6	12.5	152	320		48640
7	10	192	290		55680
VB					
1	10	6	14400		86400
2	5	960	121		116160
VB1					
1	12.5	5	4800		28800
2	12.5	5	4800		28800
VT1					
1	12.5	3	500		1000
2	12.5	2	240		480
3	10	2	400		800
4	6.3	15	122		1830
VT2					
1	12.5	3	490		1470
2	10	2	485		930
3	6.3	18	122		2196
VT3					
1	12.5	3	500		1000
2	12.5	2	240		480
3	10	2	420		840
4	6.3	14	122		1708
VT4					
1	12.5	2	500		1000
2	12.5	2	240		480
3	10	2	420		840
4	6.3	16	122		1952
VT5					
1	12.5	2	505		1010
2	12.5	2	200		400
3	10	2	458		916
4	6.3	18	122		2196
VT6					
1	12.5	6	300		1800
2	6.3	4	122		488
VT7					
1	10	3	300		900
2	10	5	280		840
3	6.3	3	122		1098

ACO	BIT	COMPR	PESO
(mm)	(m)	(m)	(kg)
60B	5	2323	358
50A	6.3	115	28
50A	8	936	371
50A	10	2597	1602
50A	12.5	2870	2164
50A	16	403	636
50A	20	227	193
Peso Total	60B =	358	1.5 kg
Peso Total	50A =	7195	kg

NOTAS GERAIS:
- VER NOTAS GERAIS FOLHA 5587-C01

ESTRUTURA DE CONCRETO:
- COBRIMENTO DAS ARMADURAS:
BLOCOS DE FUNDAÇÃO = 5,0 cm
- ADOTAR CONTROLE ADEQUADO DE QUALIDADE PARA ANÁLISE DO CONCRETO E LIMITES RIGIDOS DE TOLERÂNCIA DA VARIABILIDADE DAS MEDIDAS

IMPORTANTE:
- A EXECUÇÃO DO PROJETO DE ESTRUTURA REQUER UM ENGENHEIRO RESPONSÁVEL, EXECUÇÃO DA OBRA:
- EM CASO DE DÚVIDAS CONSULTAR ENG. SALVADOR.

MATERIAIS:
ACO CA-50A/CA-60B
CONCRETO C25 Fck≥25 MPa; Ec≥28 GPa
Fator A/Cs 0,60
Brita 1
Consumo Cimento≥280 kg/m³