



FORMA FUNDAÇÃO – NÍVEIS -0,60 / 0,00

ESCALA 1:50

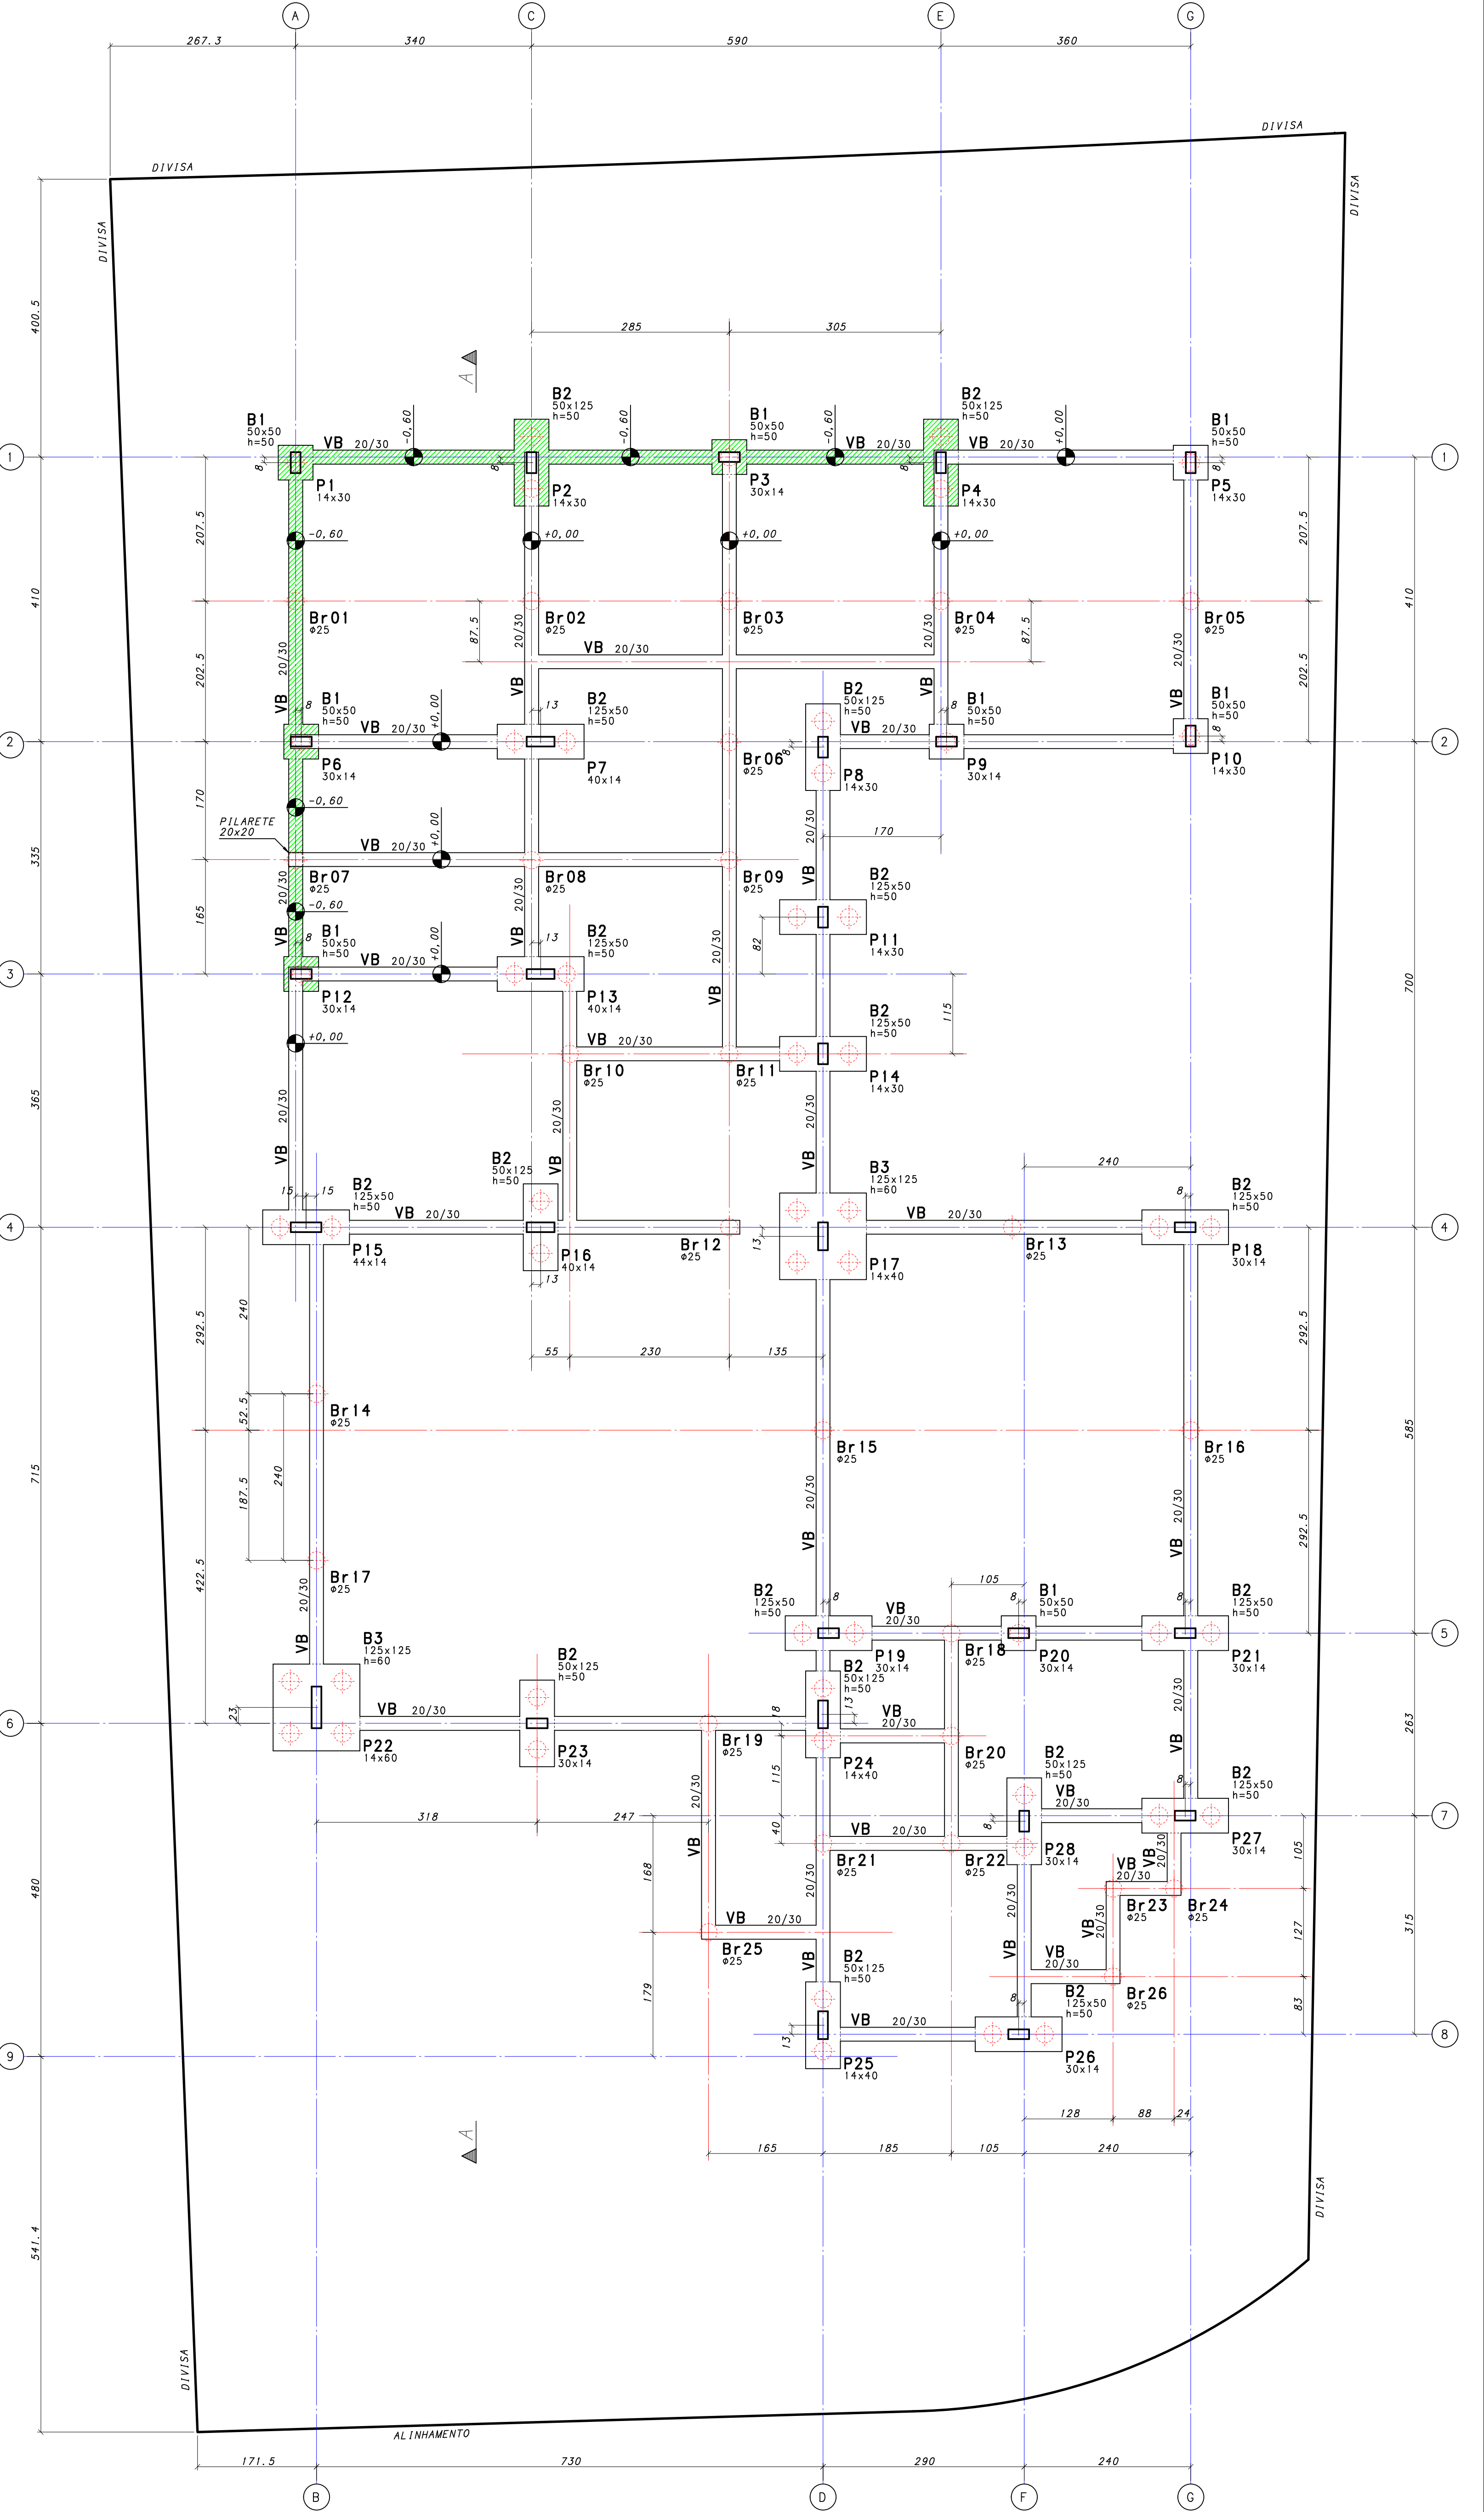


B1 50x50 h=50
Escala 1:25

8 x

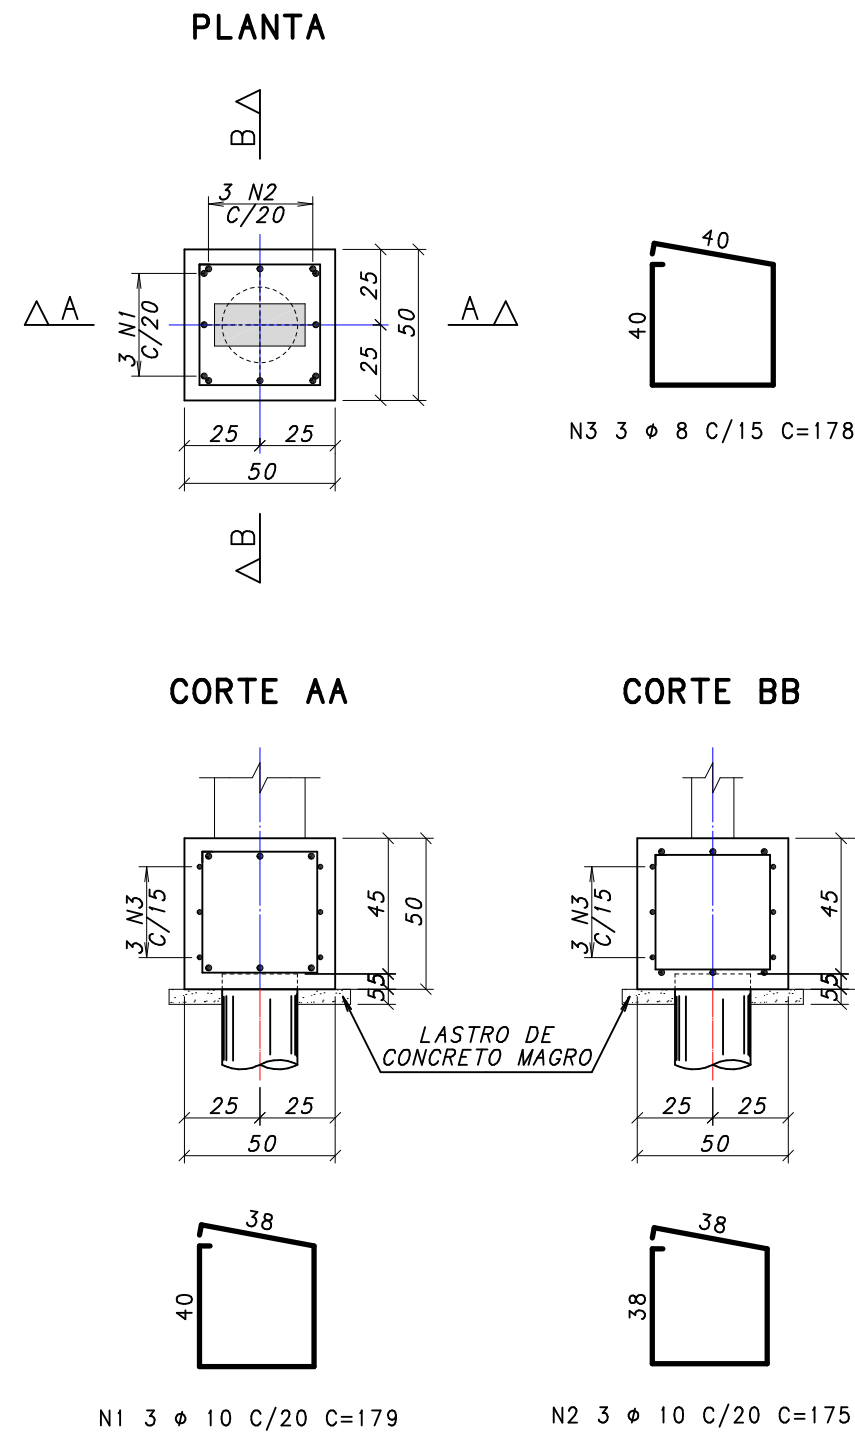


B2 125x50 h=50
Escala 1:25

18 x

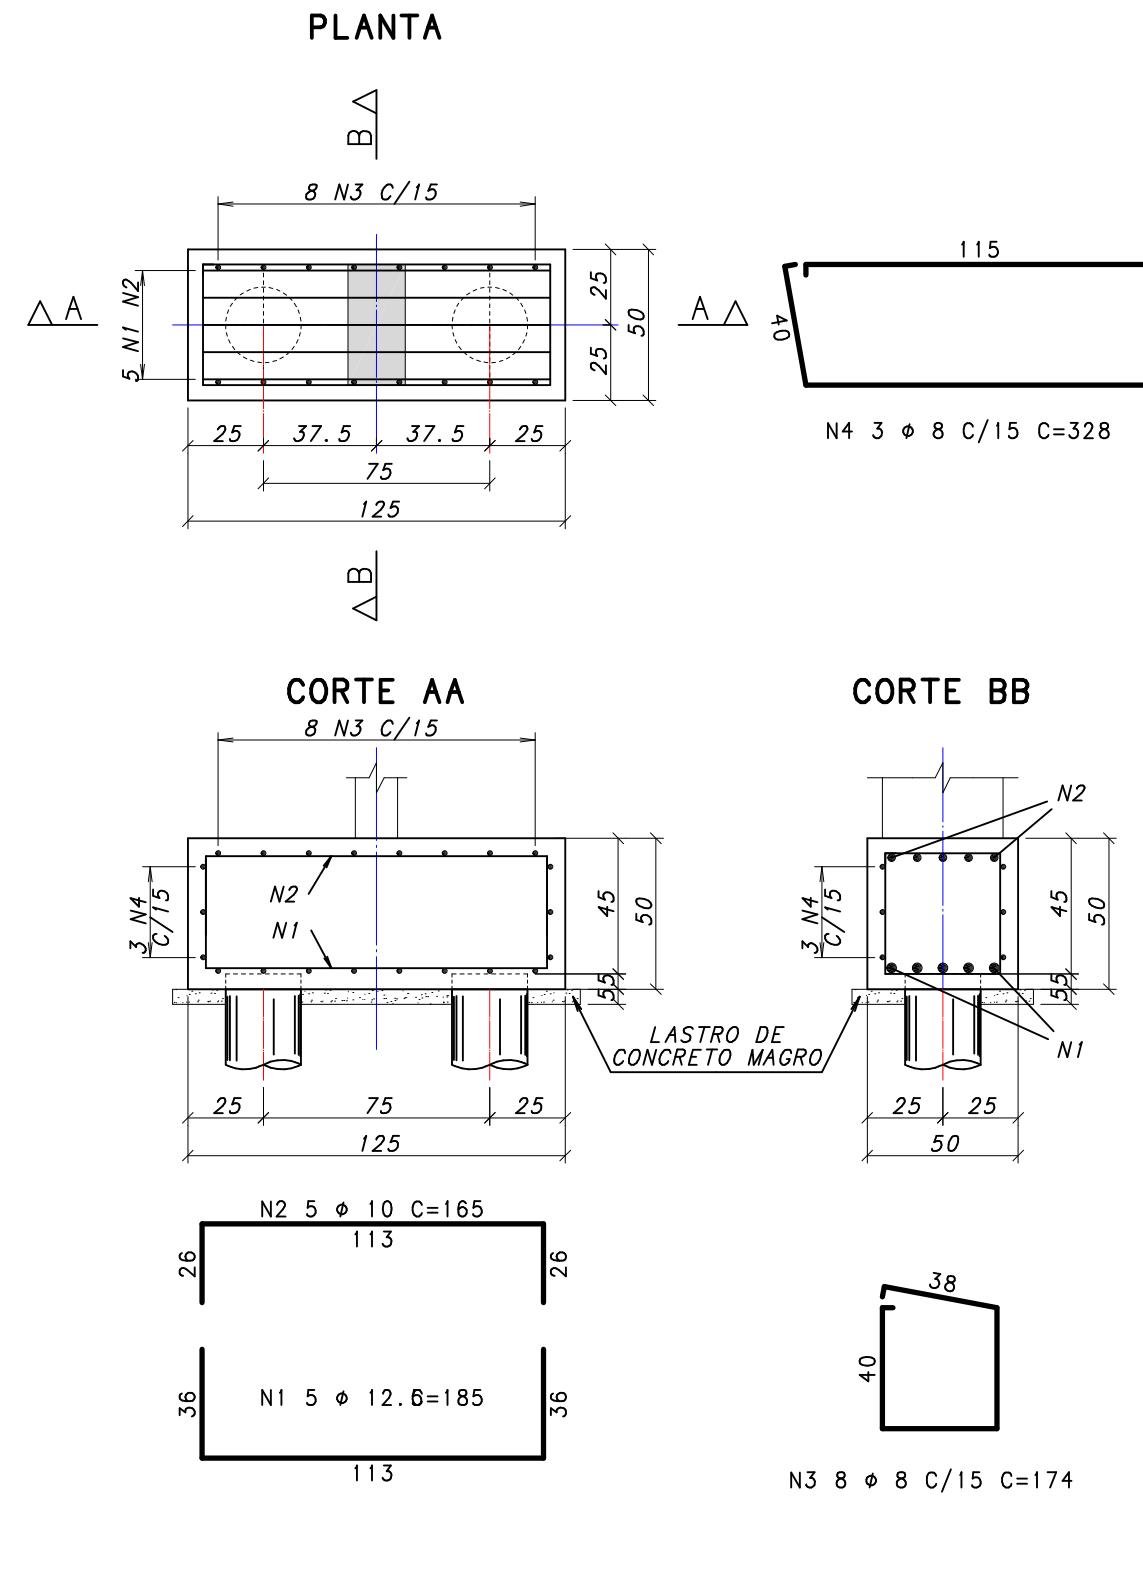


B3 125x125 h=60
Escala 1:25

2 x

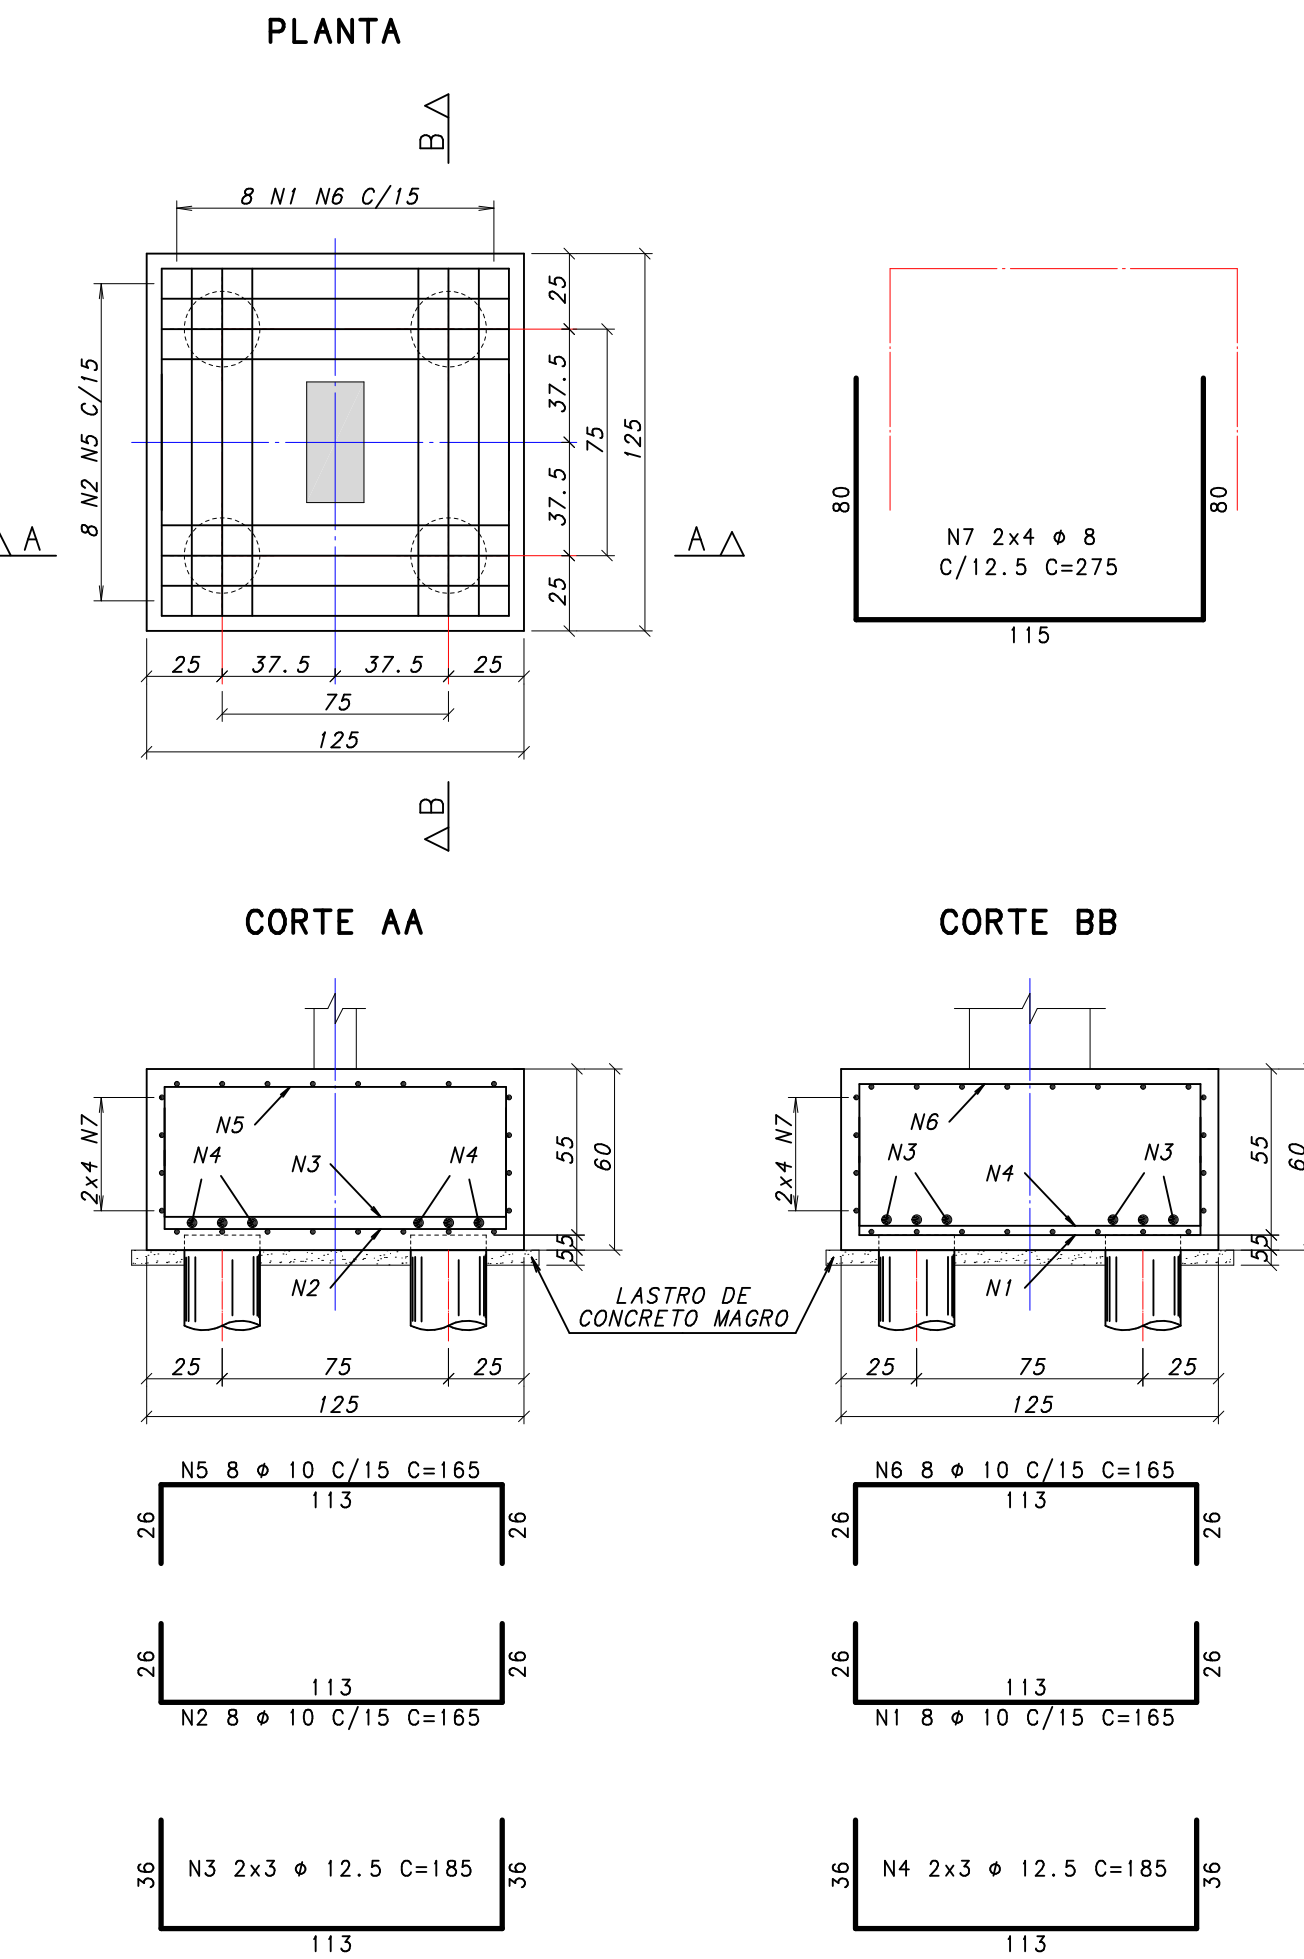


VB 20x30
ESCALA 1:20

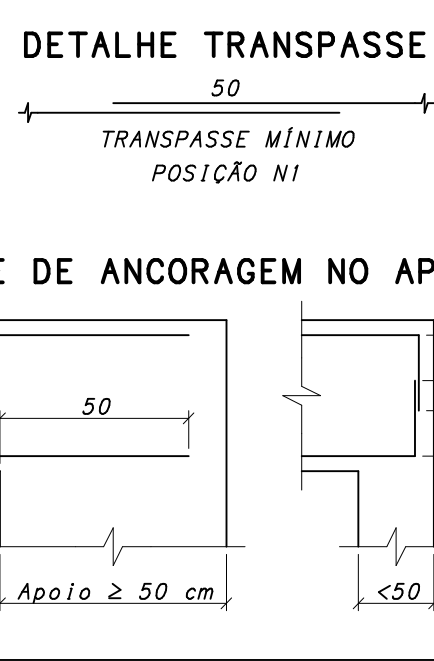

PILARETE

1 x

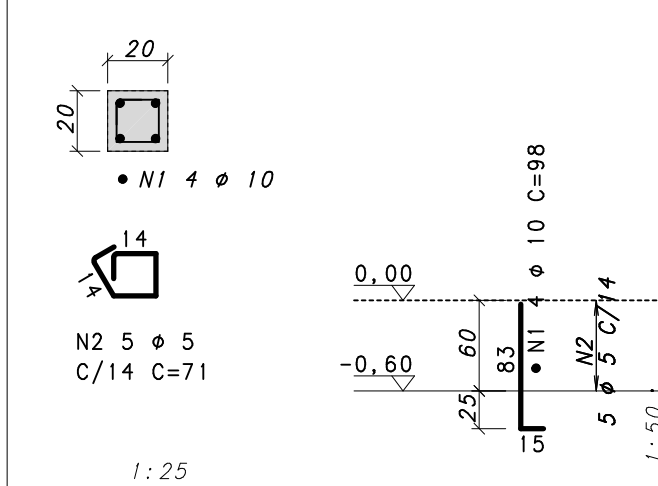

POS	BIT (mm)	QUANT	COMPRIMENTO UNIT (cm)	TOTAL (cm)
B1	(X8)			
1	10	24	179	4296
2	10	24	175	4200
3	8	24	178	4272
B2	(X18)			
1	12.5	90	185	16650
2	10	90	185	16650
3	8	144	174	25056
4	8	54	328	17712
B3	(X2)			
1	10	16	185	2960
2	10	16	185	2960
3	12.5	12	185	2220
4	12.5	12	185	2220
5	10	16	185	2960
6	10	16	185	2960
7	8	16	175	2800
PILARETE				
1	10	4	98	392
2	5	5	71	355
VB				
1	10	4	14400	57600
2	5	851	91	77441

ACO	BIT (mm)	COMPR (cm)	PESO (kg)
608	5	778	120
50A	8	514	203
50A	10	919	567
50A	12.5	211	204
Peso Total		609	120.1 kg
Peso Total		50A	973 kg

NOTAS GERAIS:

- VER NOTAS GERAIS: FOLHA 5388-C04

ESTRUTURA DE CONCRETO:

- COBERTURA DAS ARMADURAS:
BLOCOS DE FUNDAÇÃO = 5,0 cm
ELEMENTOS EM CONTATO COM O SOLO = 5,0 cm

IMPORTANTE:

- A EXECUÇÃO DO PROJETO DE ESTRUTURA REQUER
UM ENGENHEIRO RESPONSÁVEL EXECUÇÃO DA OBRA;
- EM CASO DE DÚVIDAS CONSULTAR ENG. SALVADOR.

MATERIAIS:

ACO CA-50A/CA-60B

CONCRETO C25 Fck≥ 25 MPa; Eci≥ 28 GPa
Fator A/Cs 0,60
Brita 1
Consumo Cimento≥280 kg/m³

R2 25/03/2023 REVISADO CONFORME ARG. DE 23/03/23
R1 04/02/2023 REVISADO CONFORME ARG. DE 27/01/23
R0 21/01/2023 EMISSÃO INICIAL

CLIENTE

OBRA

LOCAL

CONTÉUDO DO DOCUMENTO

FUNDAÇÃO
FORMA NÍVEL -0,60 / 0,00
ARMADURA BLOCOS E BALDRAMES

PROJETO INÚ DOCUMENTO
ESCALA Indicada C05 R2

SALVADOR NOROIA FILHO - ENG. CIVIL - CREA 506.012.830-2
RUA CAJUEIRO, 197/202 (110) 9-9611-4651 RIBEIRÃO PRETO - SP

CONVENÇÃO DE PILARES

