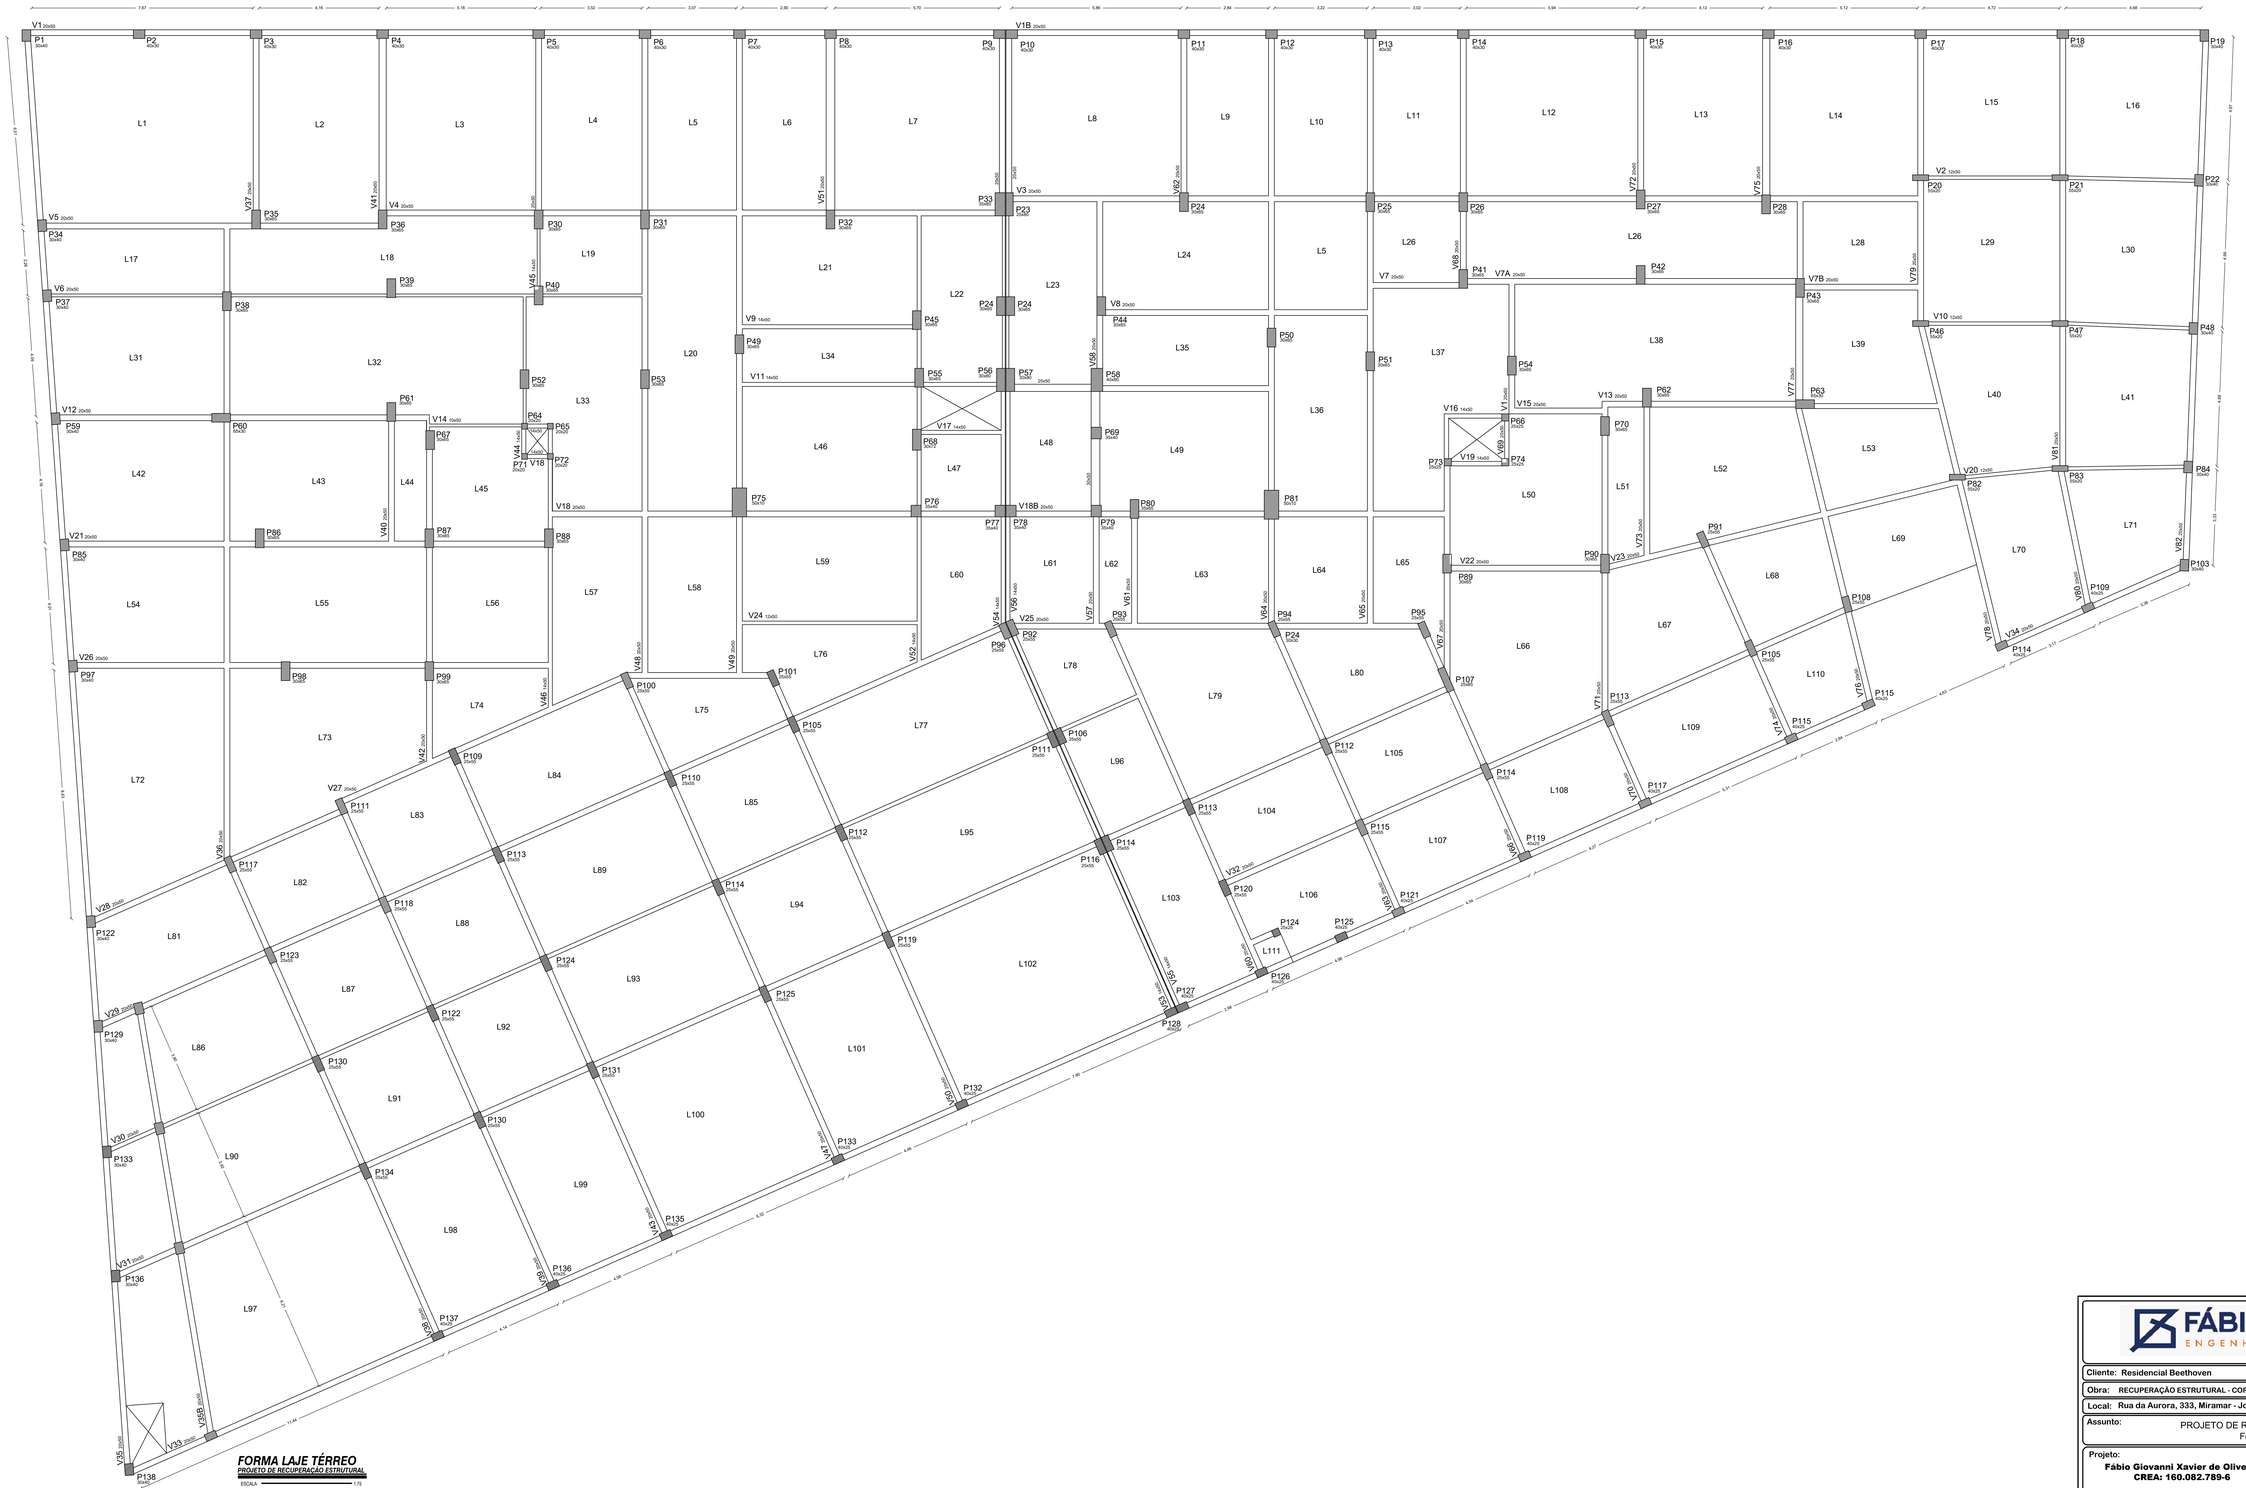

FÁBIO GIOVANNI
ENGENHARIA CONSULTIVA

Cliente:	Residencial Beethoven
Obra:	RECUPERAÇÃO ESTRUTURAL - CORROSÃO DAS ARMADURAS - PAVIMENTO SUBSOLO
Local:	Rua da Aurora, 333, Miramar - João Pessoa/PB
Assunto:	PROJETO DE RECUPERAÇÃO ESTRUTURAL Forma Laje Térreo

Projeto:
Fábio Giovanni Xavier de Oliveira
CREA: 160.082.789-6

desenho: Fábio Giovanni	escala: indicada
projeto nº: 000920	data: Agosto/2023

folha 01 / 03