




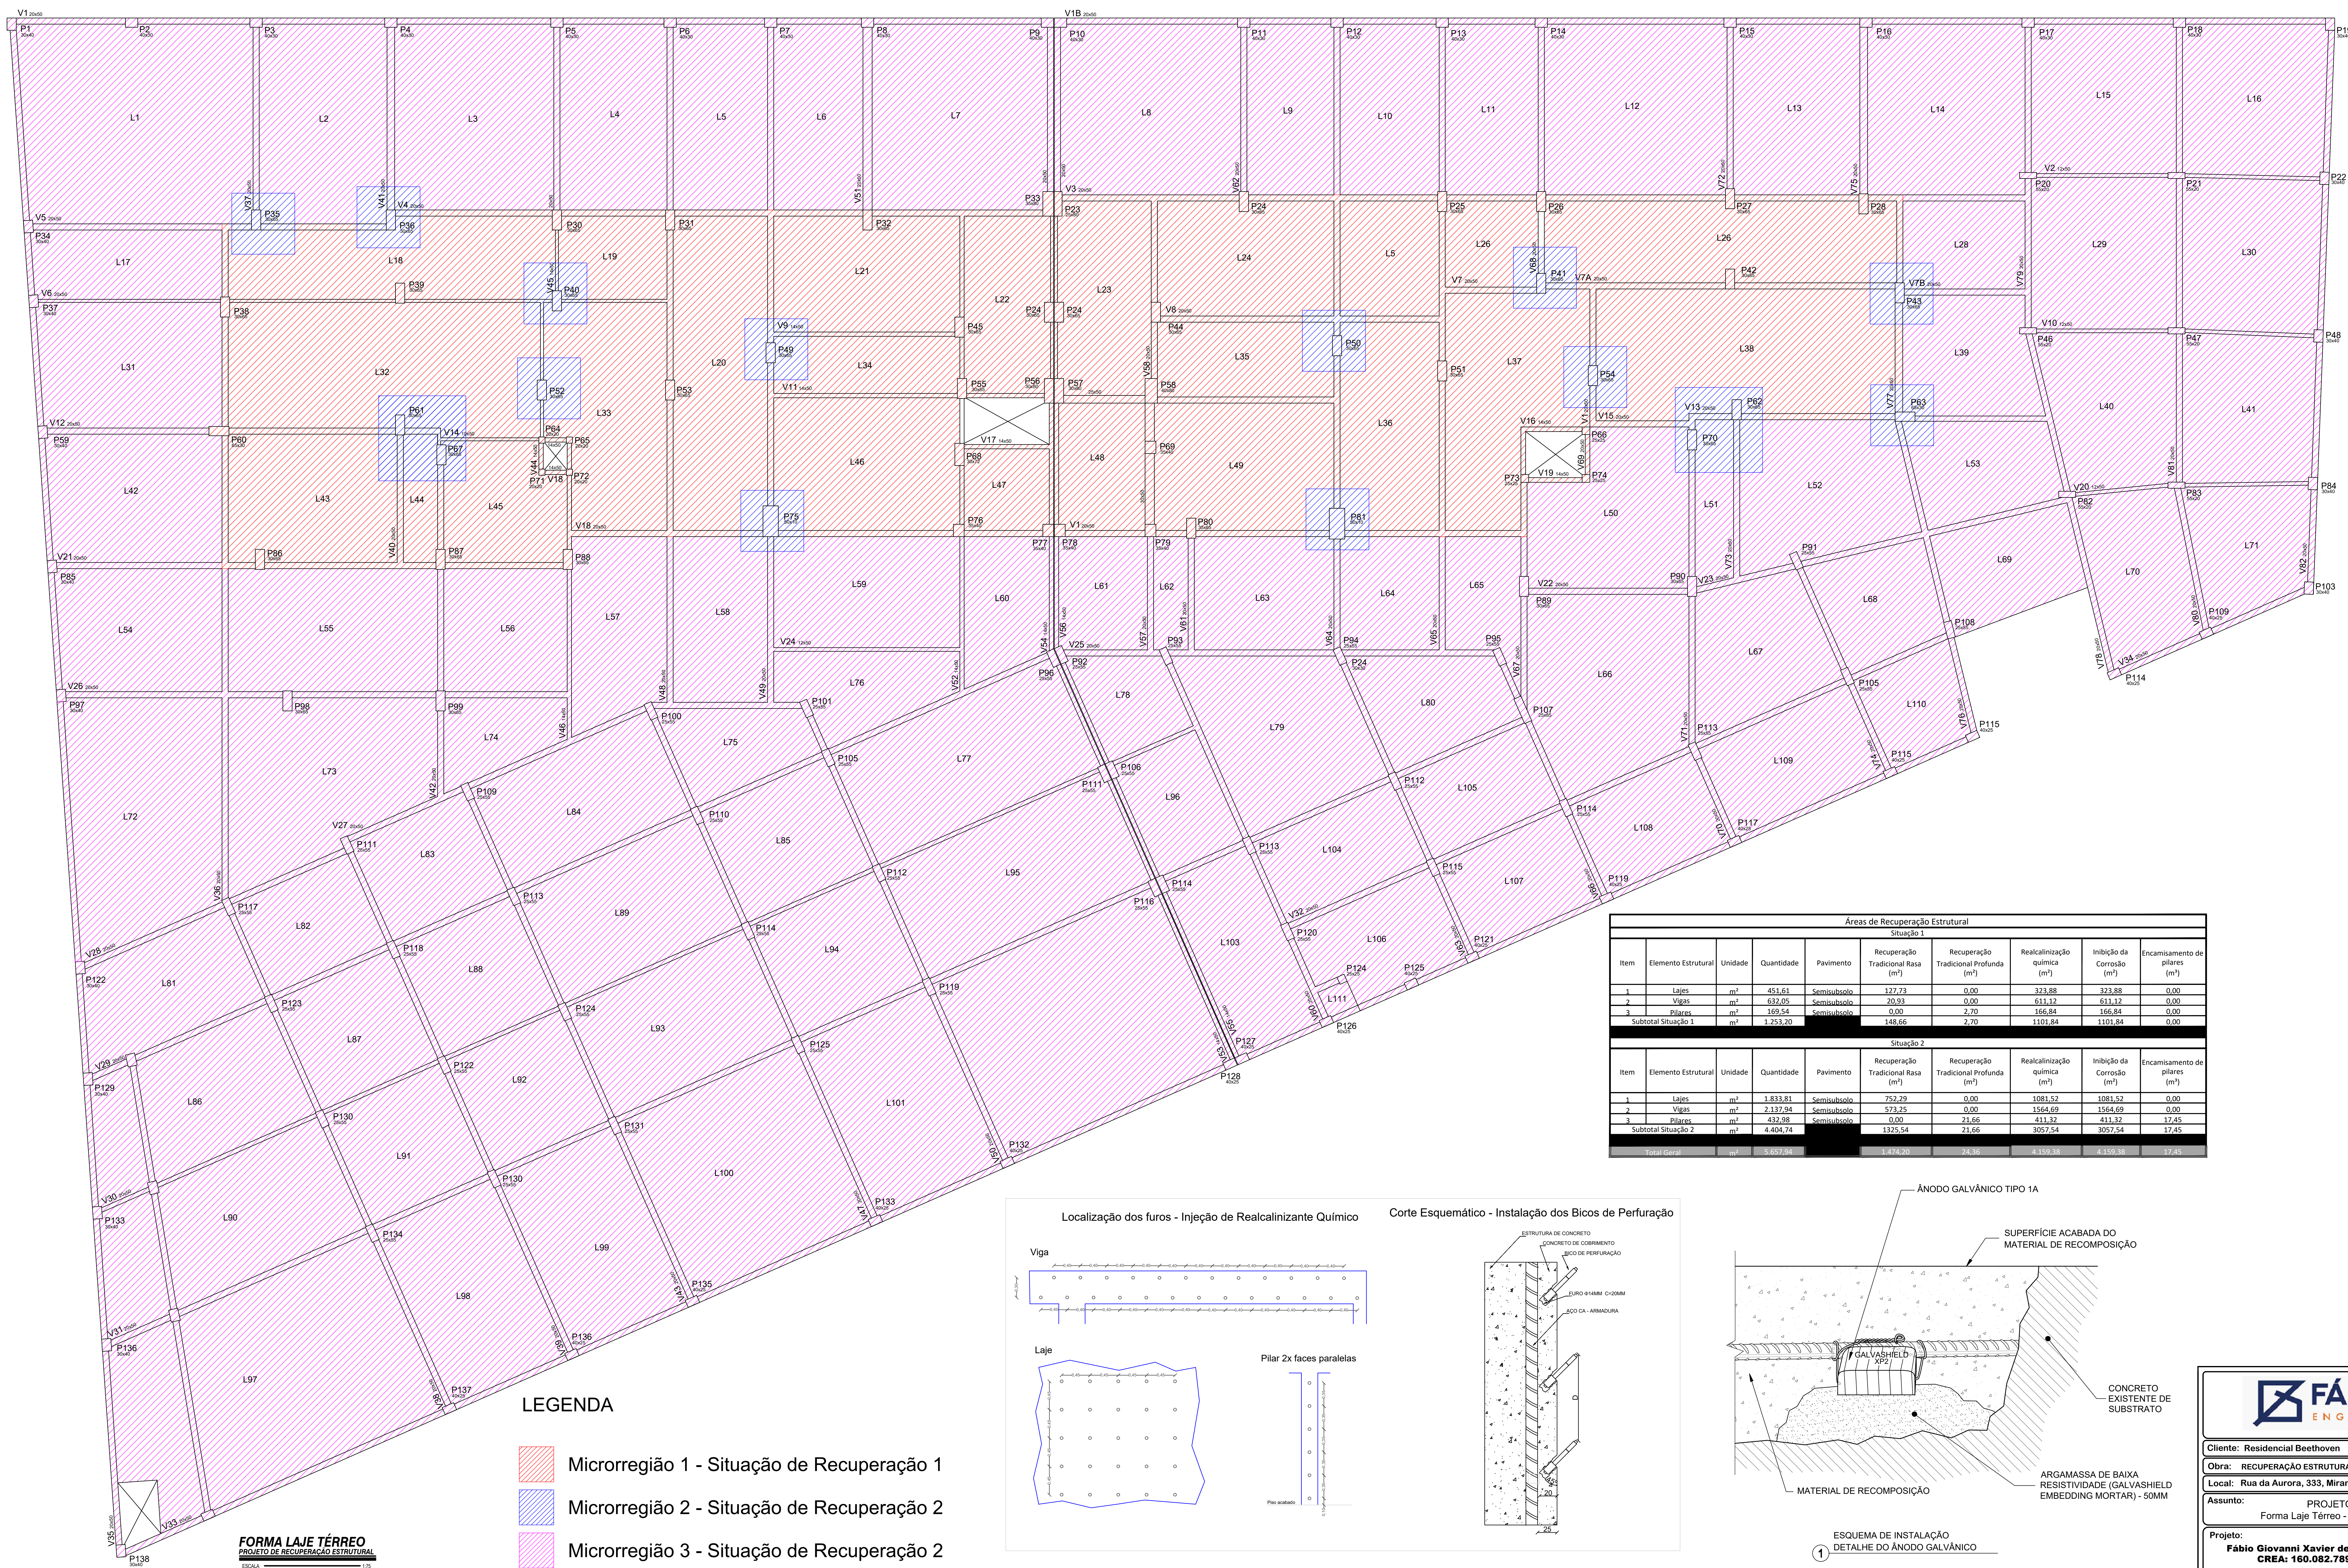


Áreas de Recuperação Estrutural								
Situação 1								
Item	Elemento Estrutural	Unidade	Quantidade	Pavimento	Recuperação Tradicional Rasa (m²)	Recuperação Tradicional Profunda (m²)	Realcalização química (m²)	Encamissamento de pilares (m²)
1	Lajes	m²	451,61	Semissubstituição	127,73	0,00	323,88	0,00
2	Vigas	m²	632,05	Semissubstituição	20,93	0,00	611,12	0,00
3	Pilares	m²	109,54	Semissubstituição	0,38	2,70	106,84	0,00
Subtotal Situação 1					148,66	2,70	1101,84	0,00
Situação 2								
Item	Elemento Estrutural	Unidade	Quantidade	Pavimento	Recuperação Tradicional Rasa (m²)	Recuperação Tradicional Profunda (m²)	Realcalização química (m²)	Encamissamento de pilares (m²)
1	Lajes	m²	1.823,81	Semissubstituição	752,29	0,00	1.081,52	0,00
2	Vigas	m²	2.137,94	Semissubstituição	579,25	0,00	1.564,69	0,00
3	Pilares	m²	432,98	Semissubstituição	0,00	21,66	411,32	17,45
Subtotal Situação 2					1.325,54	21,66	3.057,54	17,45
Total Geral					1.474,20	24,36	4.159,38	17,45

Localização dos furos - Injeção de Realcalinizante Químico

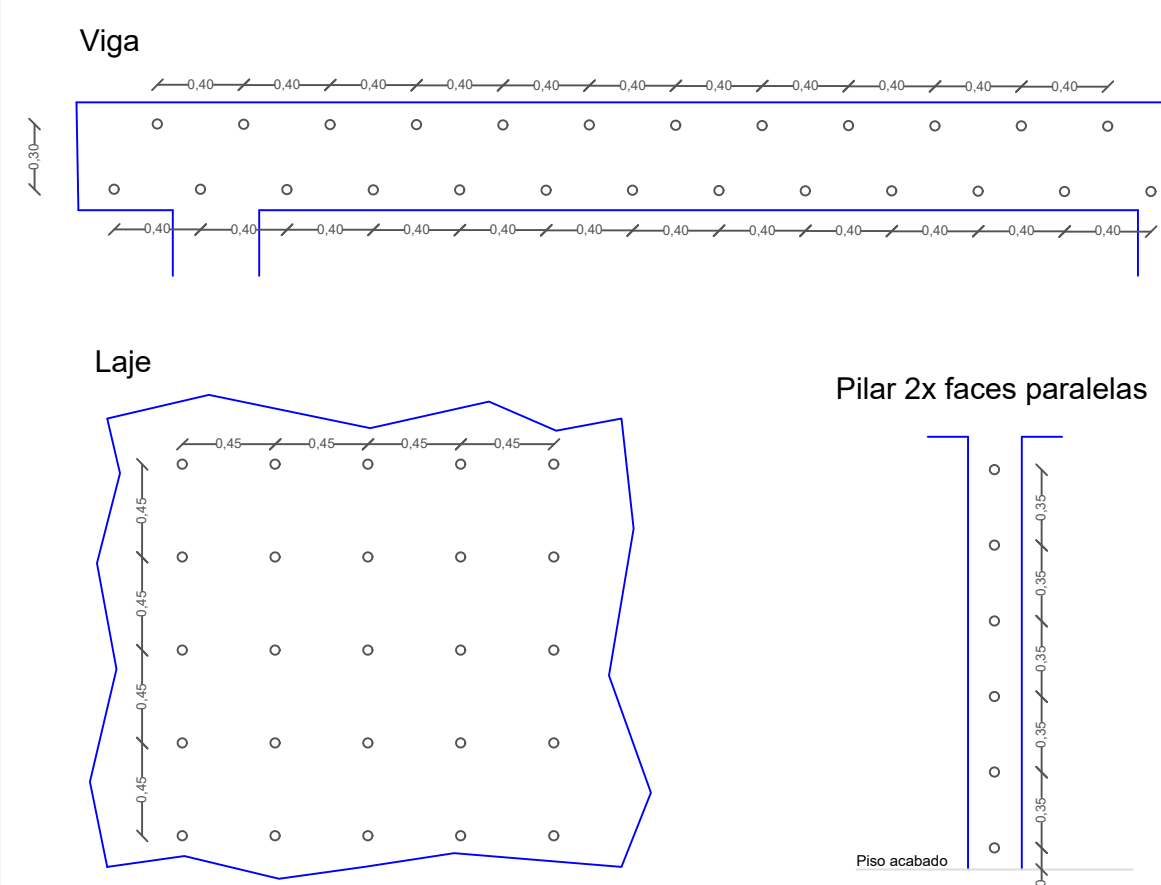

Corte Esquemático - Instalação dos Bicos de Perfuração

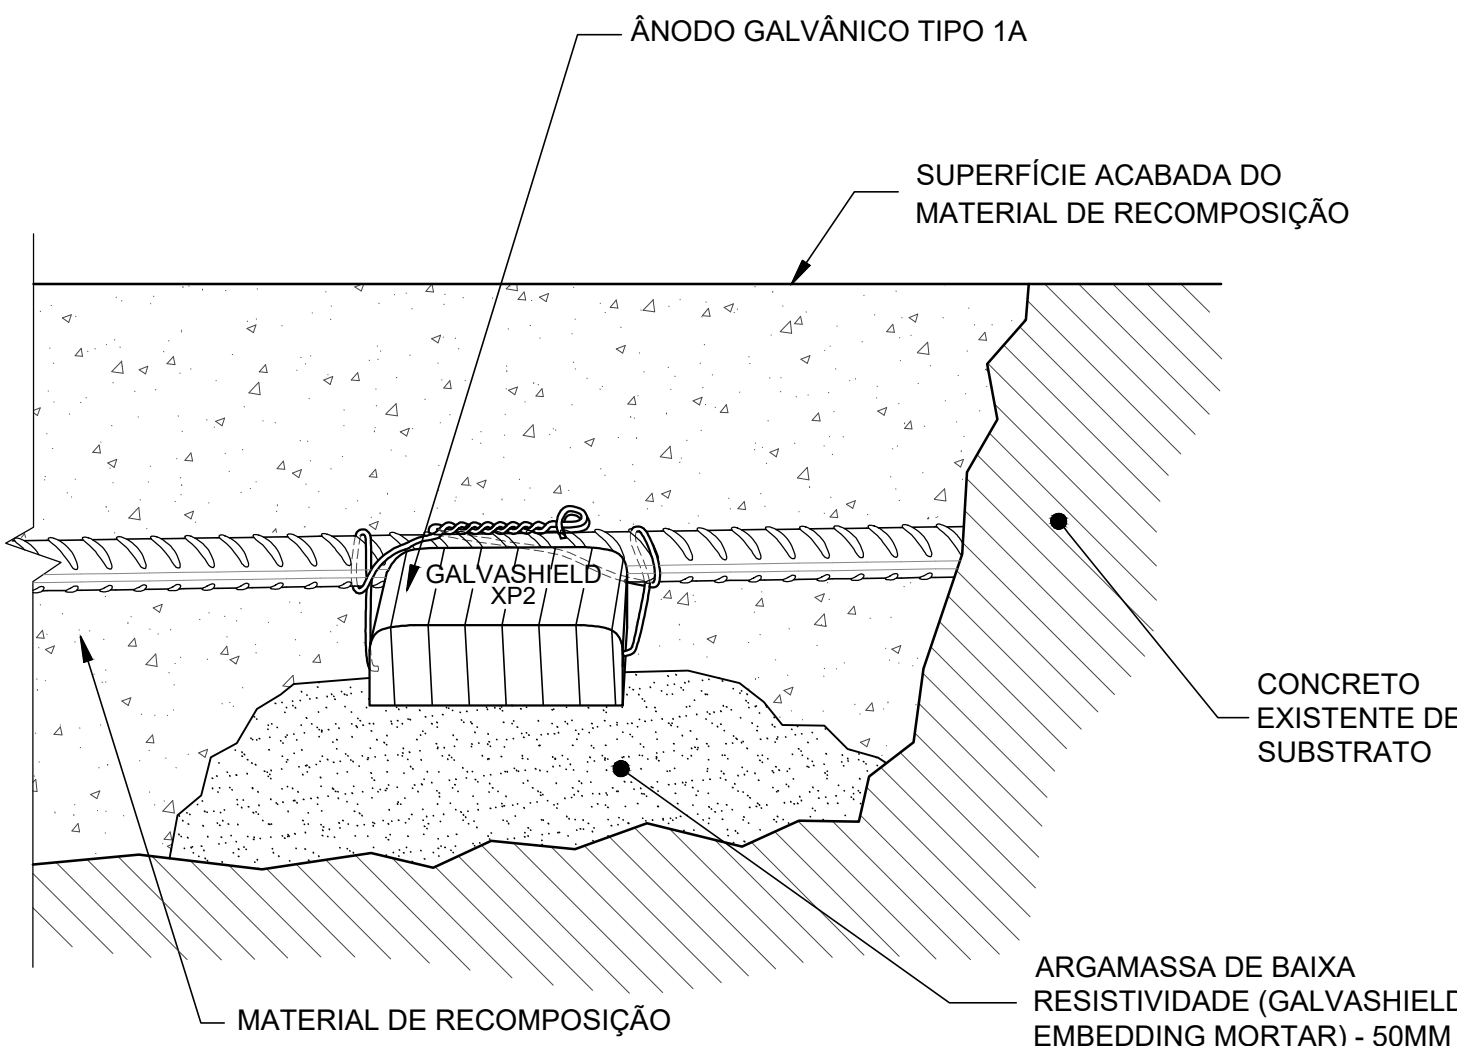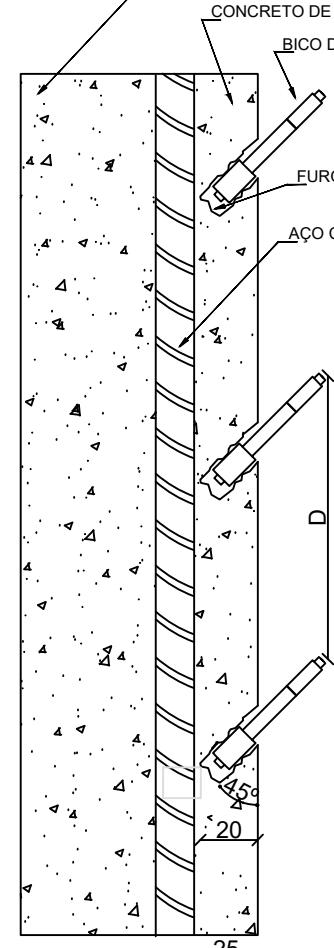

ESQUEMA DE INSTALAÇÃO
DETALHE DO ANÓDO GALVÂNICO

Ciente: Residencial Beethoven

Obra: RECUPERAÇÃO ESTRUTURAL - CORROSÃO DAS ARMADURAS - PAVIMENTO SUBSOLO

Local: Rua da Aurora, 333, Miramar - João Pessoa/PB

Assunto: PROJETO DE RECUPERAÇÃO ESTRUTURAL
Forma Laje Térreo - Localização das Microrregiões e Detalhes Gerais

Projeto: Fábio Giovanni Xavier de Oliveira
CREA: 160.082.789-6

desenho: Fábio Giovanni
projeto nº: 000000

escala: indicada
data: Agosto/2023

folha 03
03