
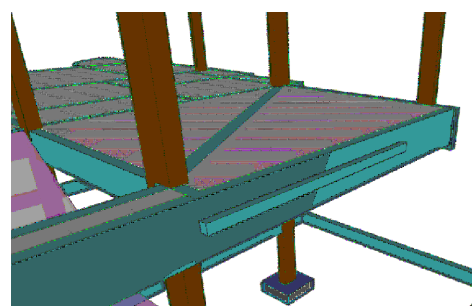


PLANTA DE FÔRMA - 1º ANDAR

Continuidade completa
- opoída
- ingosta

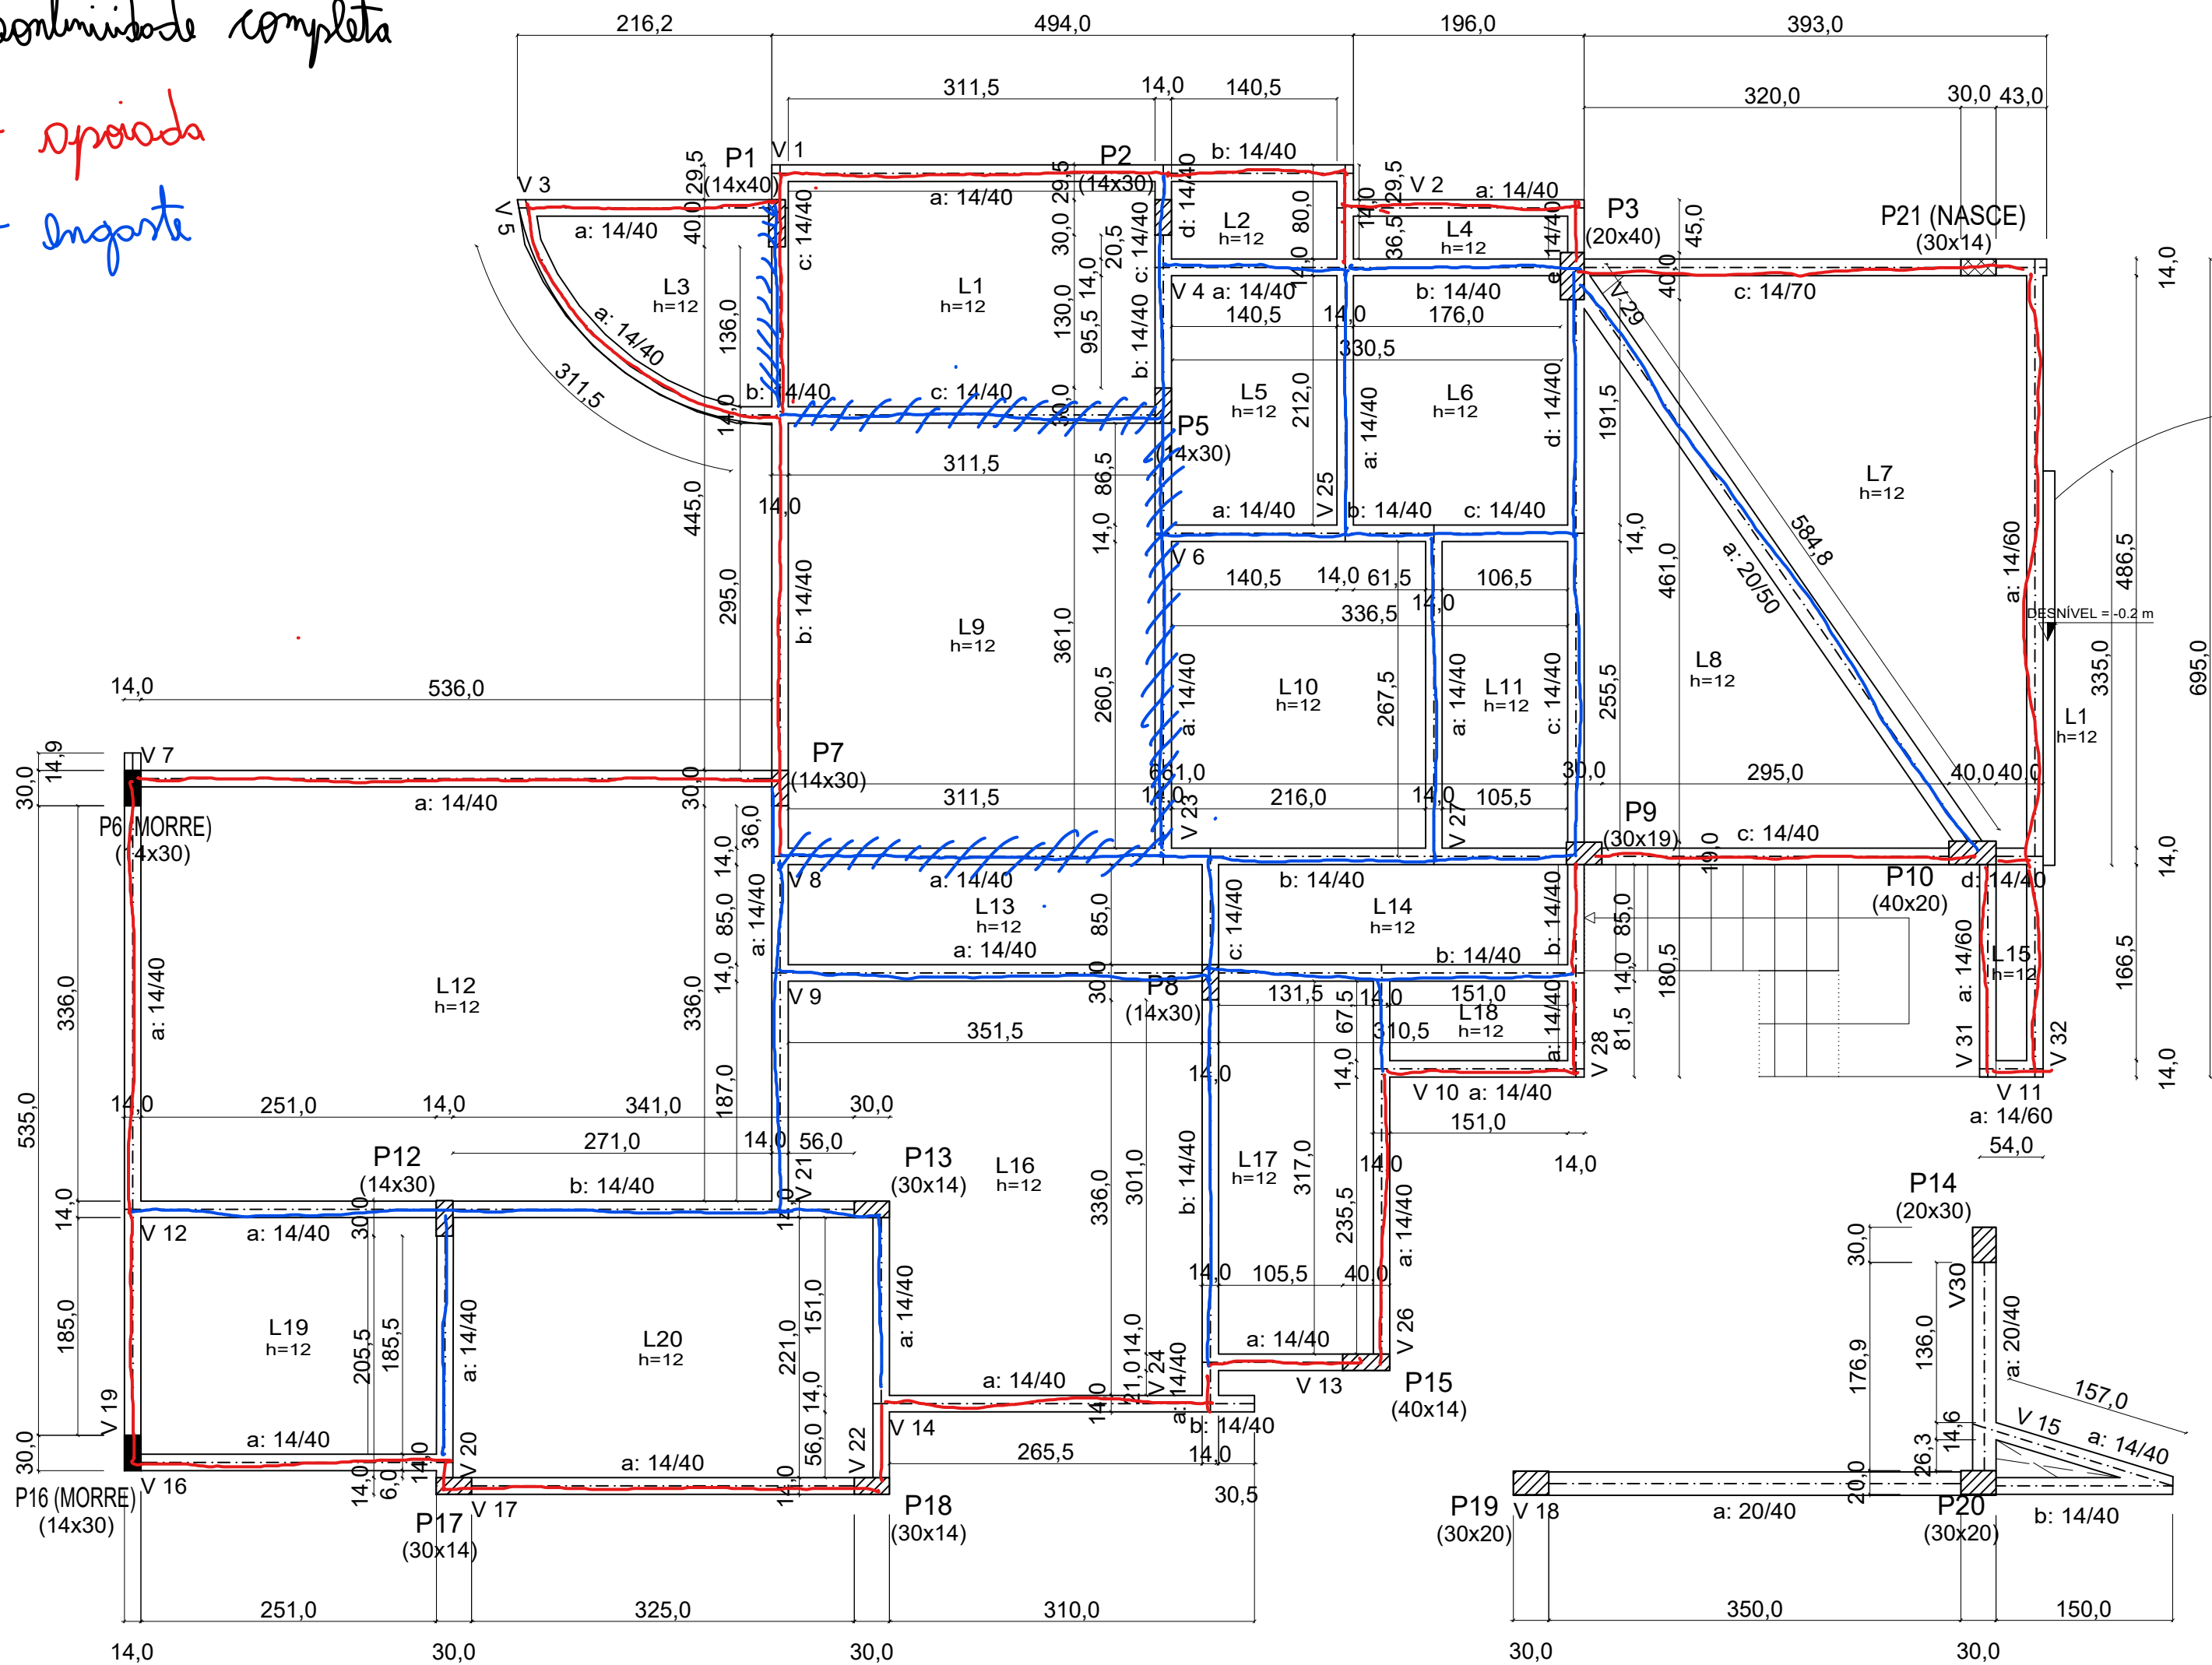


PLANTA DE FÔRMA - 1º ANDAR (+3,45)
esc 1:50

PERSPECTIVA 1

PERSPECTIVA 2

PERSPECTIVA 3

PERSPECTIVA 4

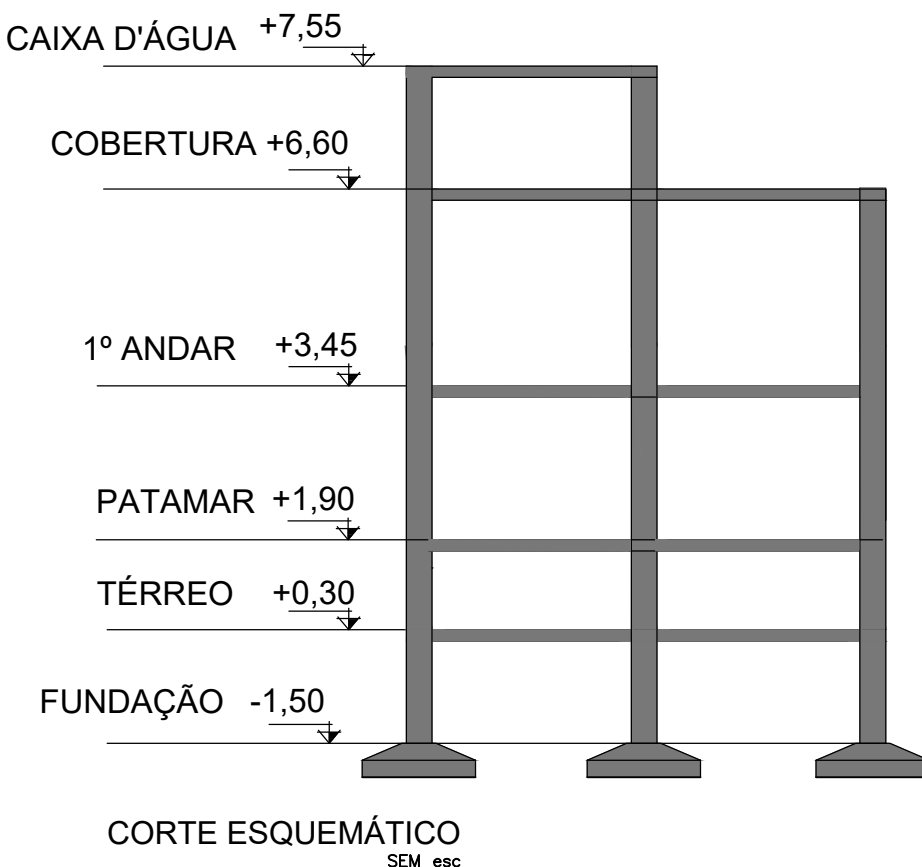

- NOTAS
- 1- POSICIONAR SAPATAS SOBRE CONCRETO MAGRO DE 5cm DE ESPESSURA;
 - 2- A EXECUÇÃO DO ESCORAMENTO DEVE RESPEITAR A NBR 15696
 - 3- RETIRAR ESCORAMENTO APÓS 28 DIAS DA CONCRETAGEM
 - 4 - QUALQUER MODIFICAÇÃO OU DÚVIDA NO PROJETO DEVERÁ SER IMEDIATAMENTE INFORMADA AO PROJETISTA ESTRUTURAL

PROJETO ESTRUTURAL

COBRIMENTOS MÍNIMOS

LAJE E ESCADA: 2,5cm
PILAR: 2,5cm
PILAR (CONTATO COM O SOLO): 2,5cm

SAPATA: 4cm
VIGA: 2,5cm

CONCRETO
fck = 25 MPa
AÇO: CA-50 E CA-60

LEGENDA

- | | |
|------------------|------------------|
| PILAR NASCE | VAZADO |
| MUDANÇA DE SEÇÃO | L LAJE |
| PILAR SOBRE | H ALTURA DA LAJE |
| PILAR MORRE | V VIGA |
| | P PILAR |
| | S SAPATA |

Responsável Técnico

Área: Área terreno _____ m²
Área construída _____ m²

Obra: Residência unifamiliar.

Local:

Assunto: PLANTA DE FÔRMA - 1º ANDAR

Folha: 01/01

Escala: 1:50




Data:

Calculista Estrutural:

Proprietário:

Estrutural

PLANTA DE FÔRMA - 1º ANDAR

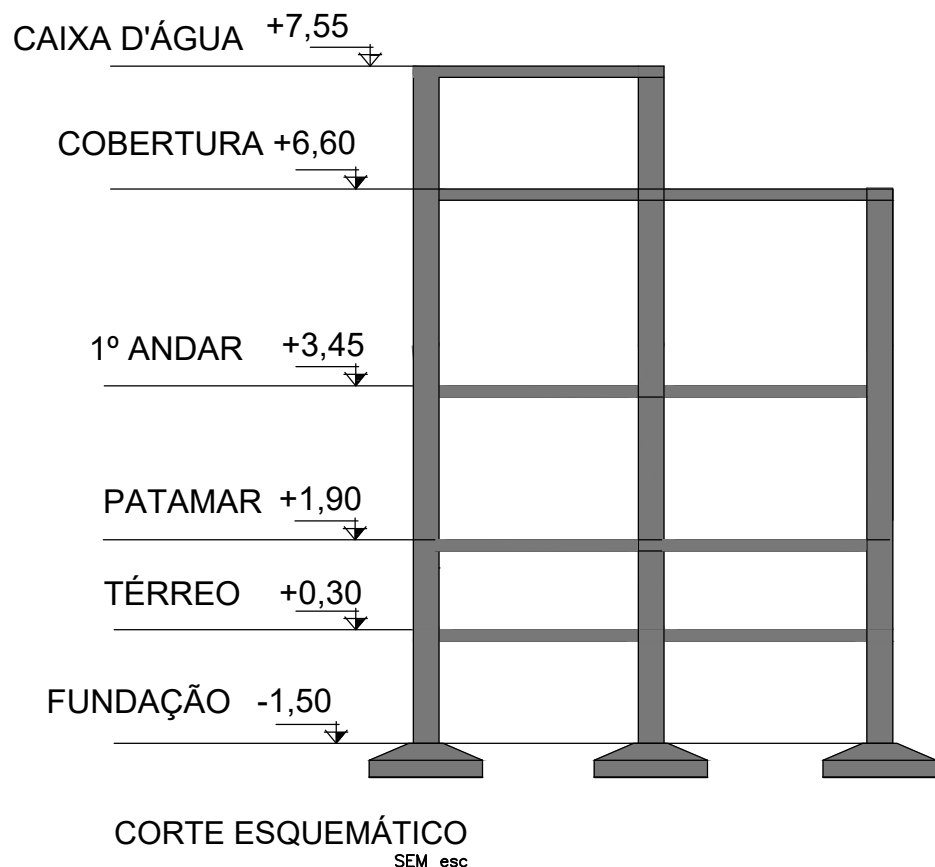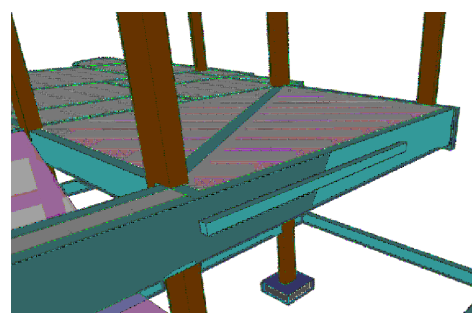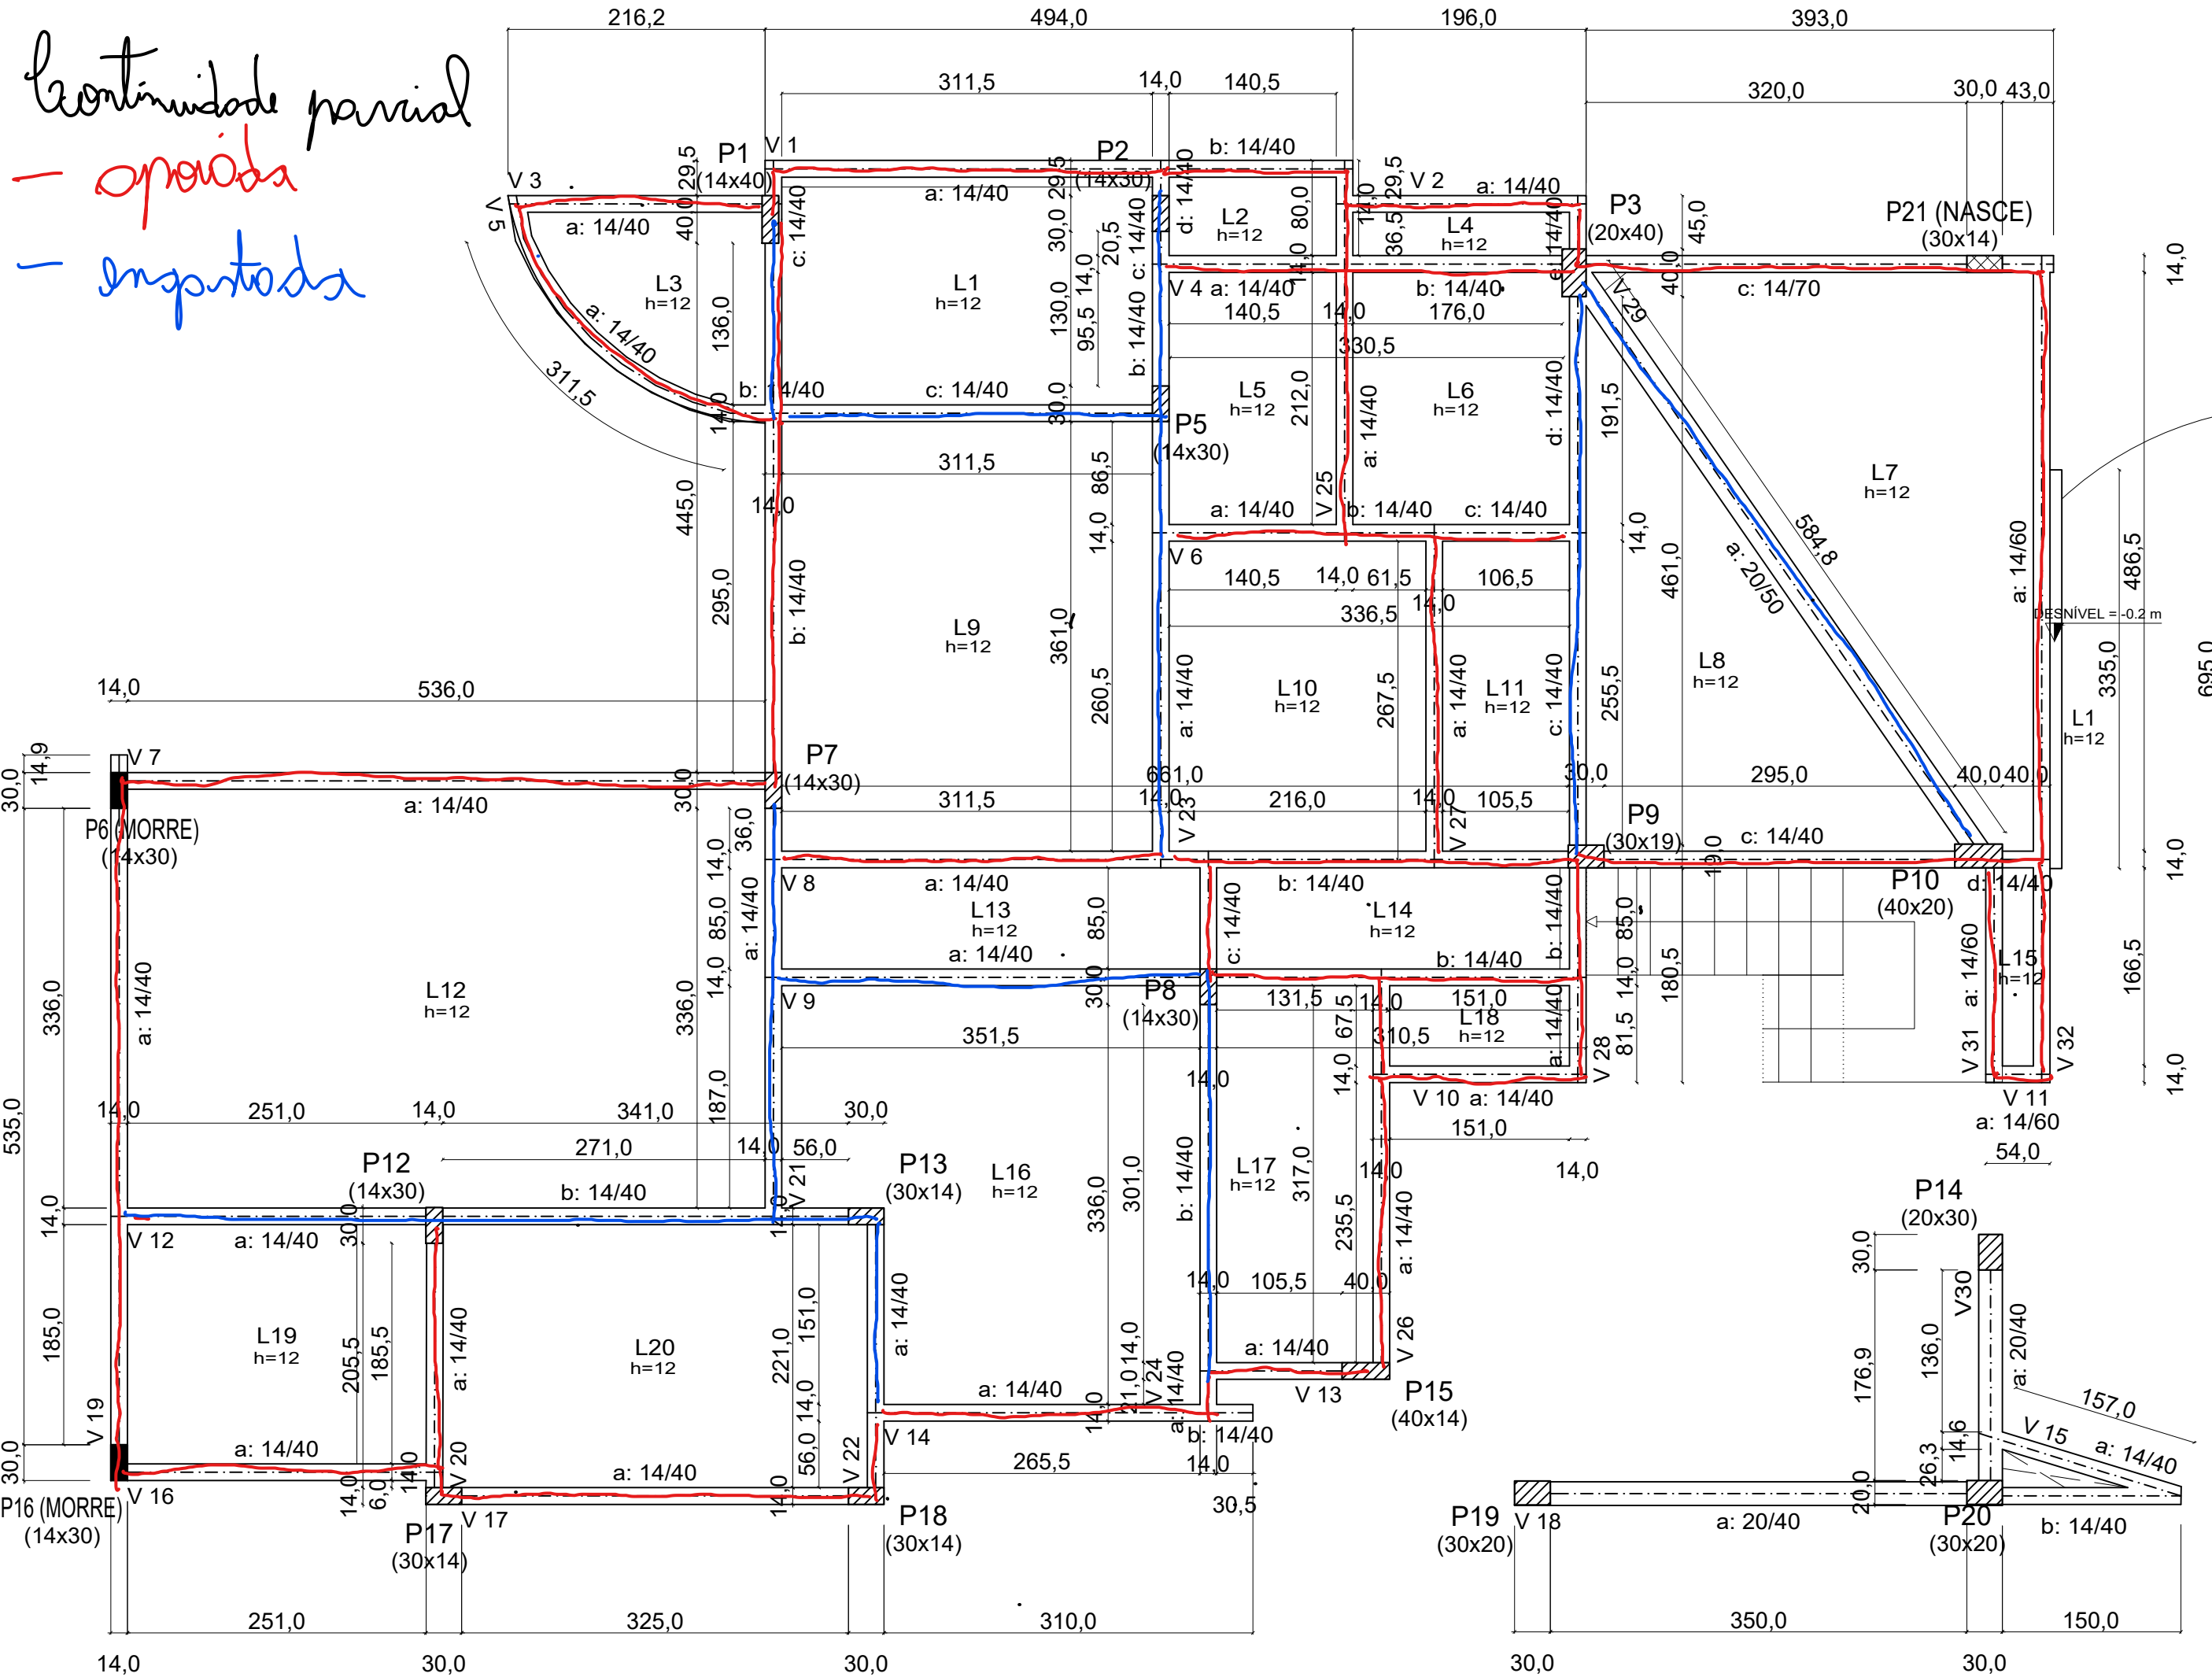

- NOTAS
- 1- POSICIONAR SAPATAS SOBRE CONCRETO MAGRO DE 5cm DE ESPESSURA;
 - 2- A EXECUÇÃO DO ESCORAMENTO DEVE RESPEITAR A NBR 15696
 - 3- RETIRAR ESCORAMENTO APÓS 28 DIAS DA CONCRETAGEM
 - 4 - QUALQUER MODIFICAÇÃO OU DÚVIDA NO PROJETO DEVERÁ SER IMEDIATAMENTE INFORMADA AO PROJETISTA ESTRUTURAL

PROJETO ESTRUTURAL

COBRIMENTOS MÍNIMOS

LAJE E ESCADA: 2,5cm
PILAR: 2,5cm
PILAR (CONTATO COM O SOLO): 2,5cm

SAPATA: 4cm
VIGA: 2,5cm

CONCRETO
fck = 25 MPa
AÇO: CA-50 E CA-60

LEGENDA

- | | |
|------------------|------------------|
| PILAR NASCE | VAZADO |
| MUDANÇA DE SEÇÃO | LAJE |
| PILAR SOBRE | H ALTURA DA LAJE |
| PILAR MORRE | V VIGA |
| | P PILAR |
| | S SAPATA |

Responsável Técnico


Área:	Obra: Residência unifamiliar.
Área terreno _____ m²	Local:
Área construída _____ m²	

Assunto:	Folha:
PLANTA DE FÔRMA - 1º ANDAR	01/01

Escala:	Data:	Calculista Estrutural:
1:50		

Proprietário:	Estrutural
---------------	------------

PLANTA DE FÔRMA - 1º ANDAR

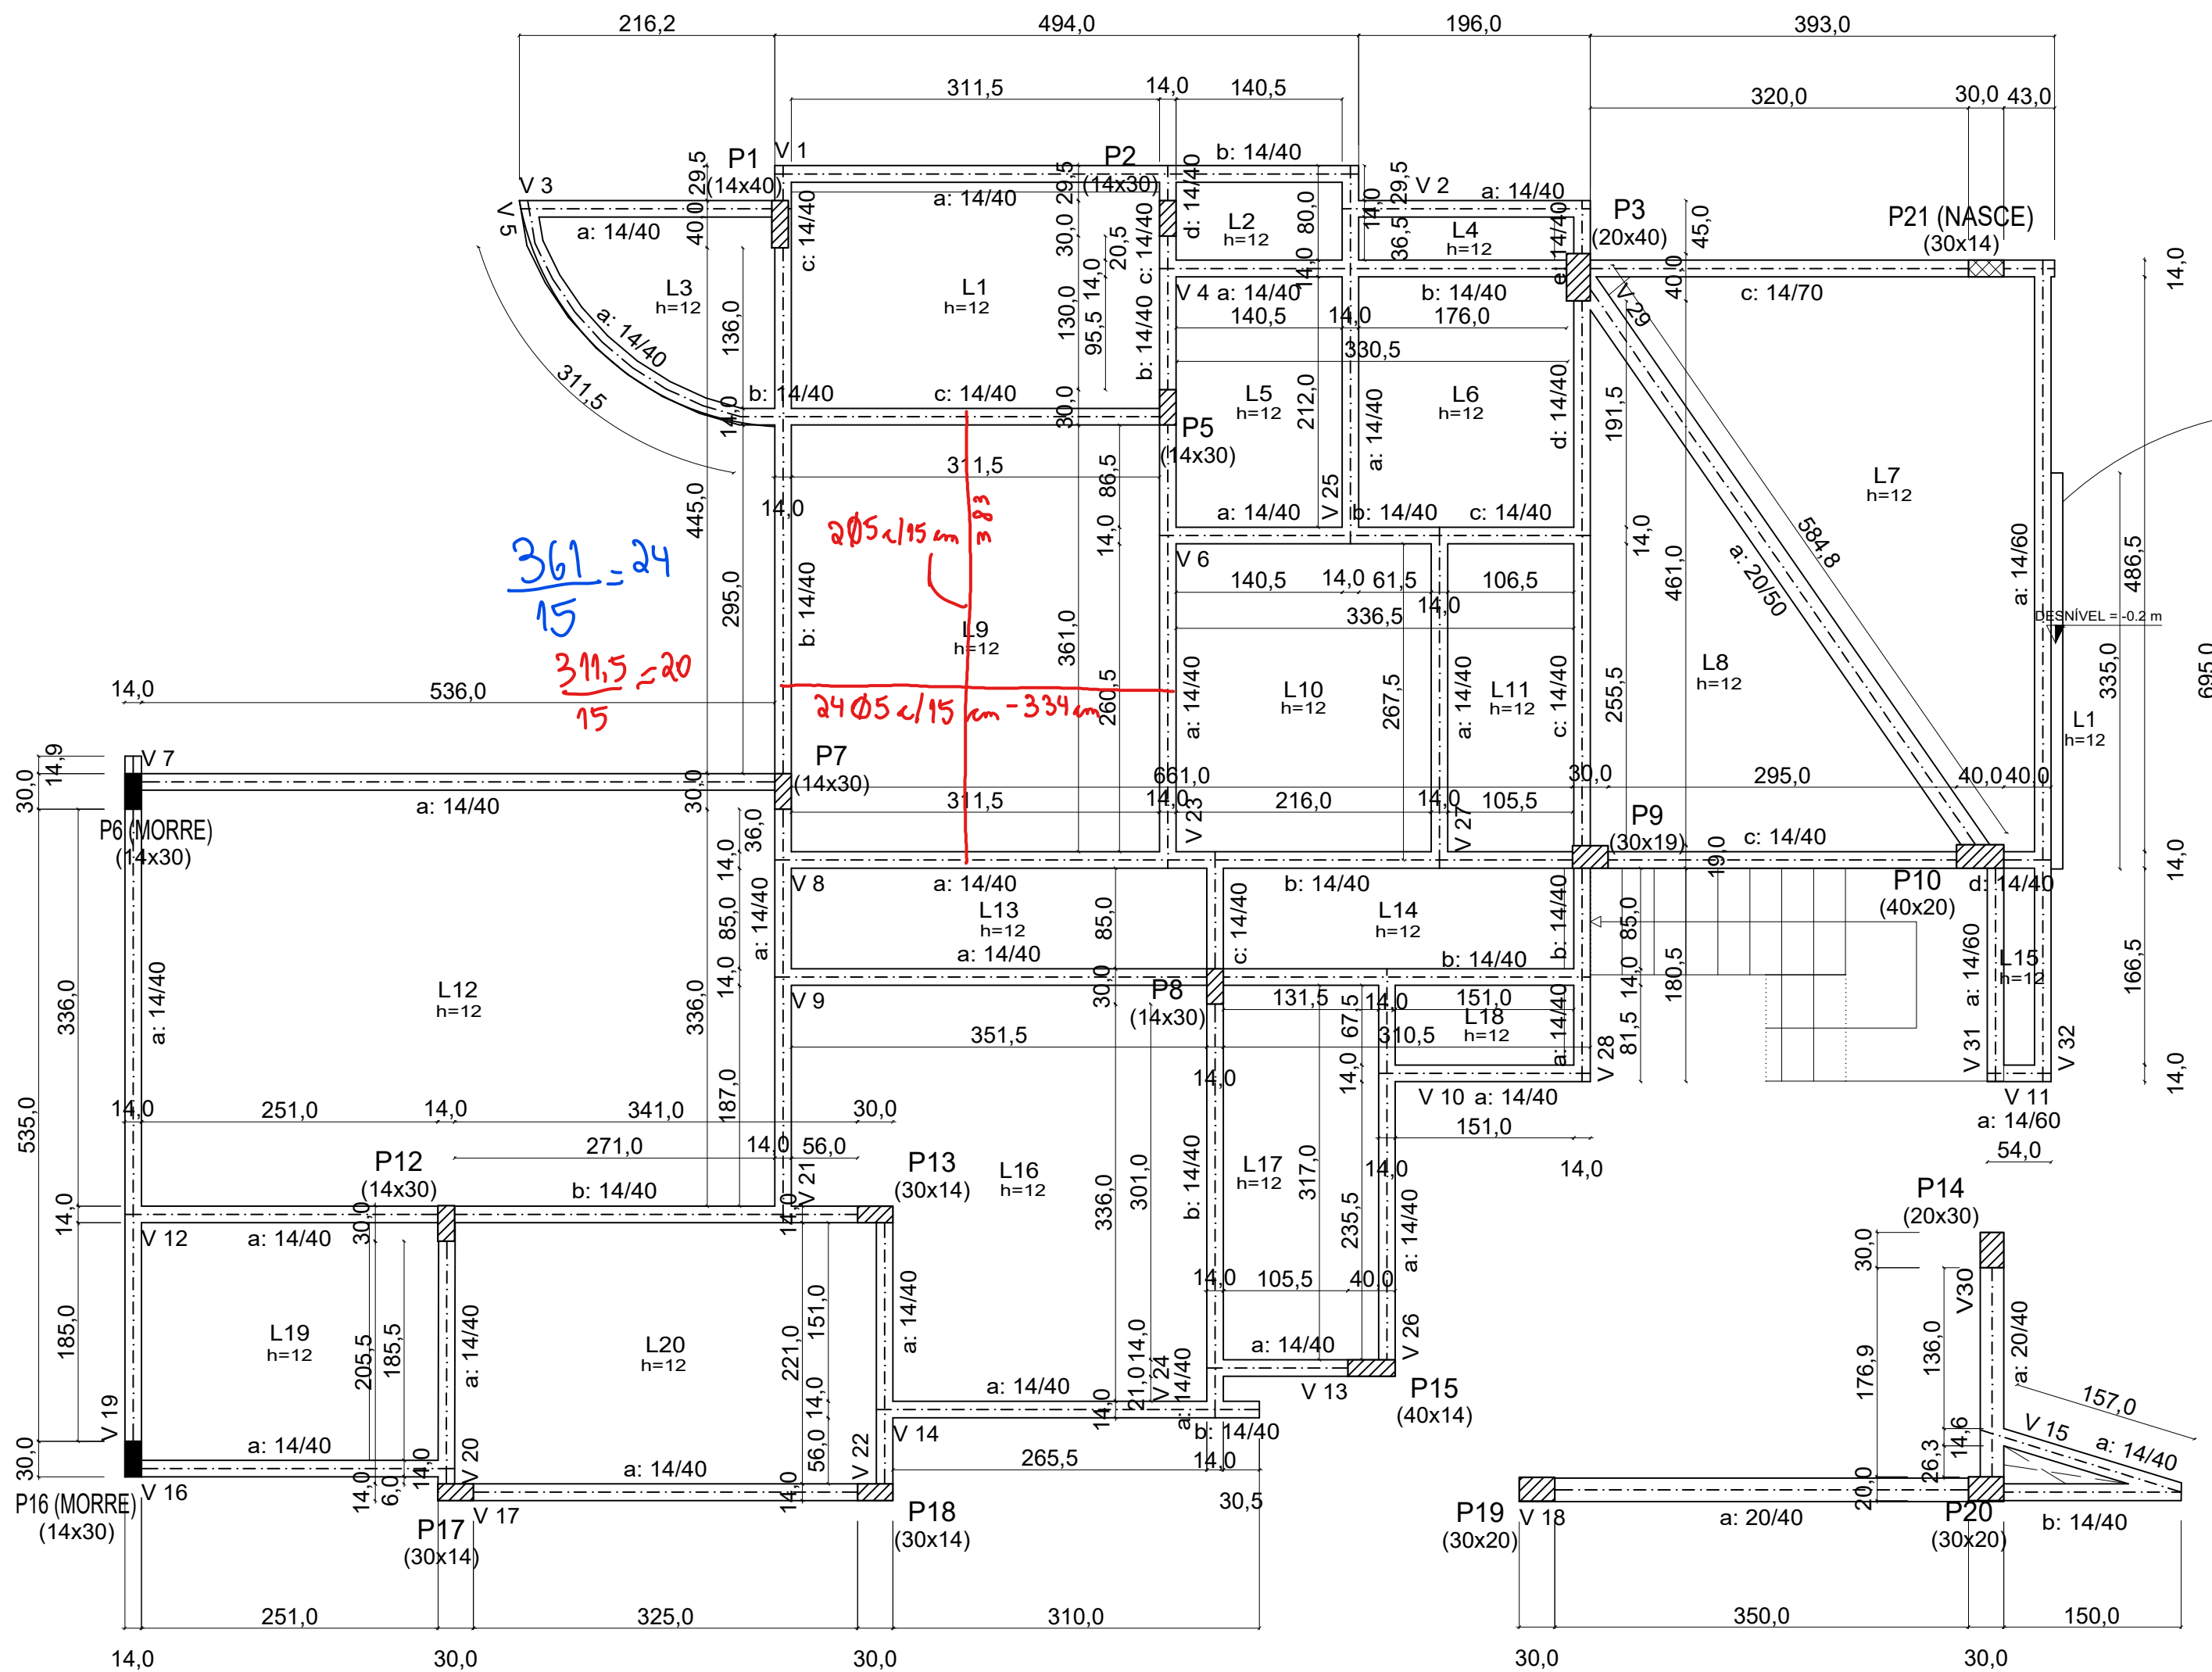


PLANTA DE FÔRMA - 1º ANDAR (+3,45)
esc 1:50

PERSPECTIVA 1

PERSPECTIVA 2

PERSPECTIVA 3

PERSPECTIVA 4

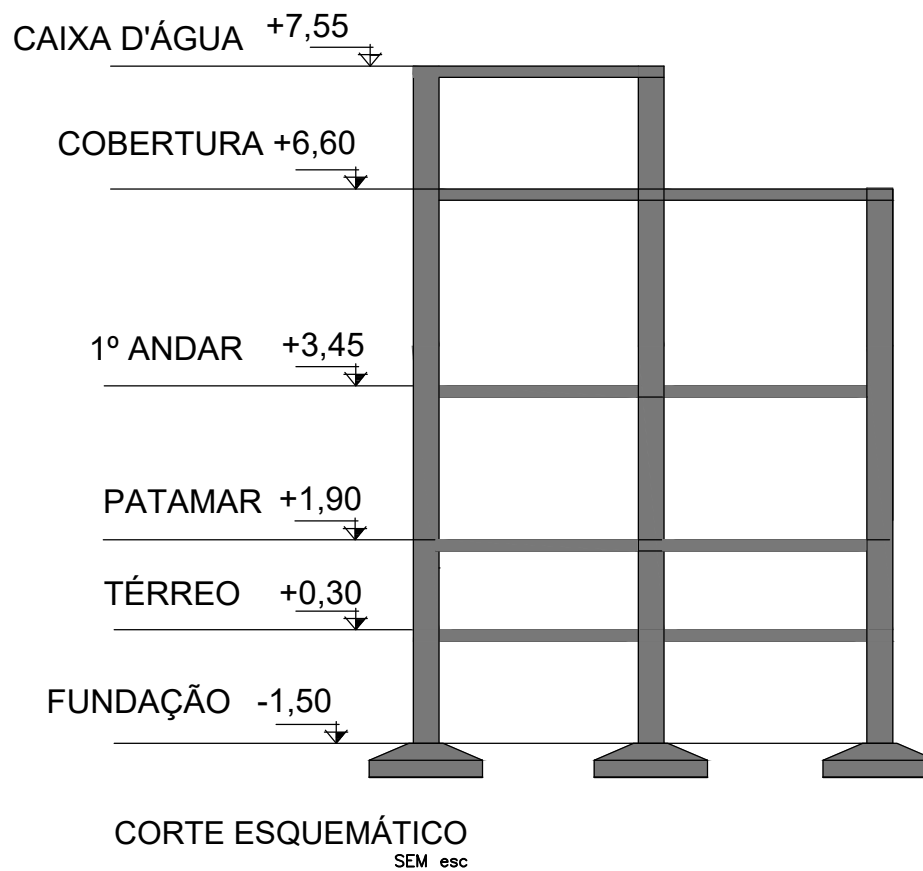

- NOTAS
- 1- POSICIONAR SAPATAS SOBRE CONCRETO MAGRO DE 5cm DE ESPESSURA;
 - 2- A EXECUÇÃO DO ESCORAMENTO DEVE RESPEITAR A NBR 15696
 - 3- RETIRAR ESCORAMENTO APÓS 28 DIAS DA CONCRETAGEM
 - 4 - QUALQUER MODIFICAÇÃO OU DÚVIDA NO PROJETO DEVERÁ SER IMEDIATAMENTE INFORMADA AO PROJETISTA ESTRUTURAL

PROJETO ESTRUTURAL

COBRIMENTOS MÍNIMOS

LAJE E ESCADA: 2,5cm
PILAR: 2,5cm
PILAR (CONTATO COM O SOLO): 2,5cm

SAPATA: 4cm
VIGA: 2,5cm

CONCRETO
fck = **25** MPa
AÇO: CA-50 E CA-60

LEGENDA

- | | |
|--------------------|------------------|
| ▣ PILAR NASCE | ▣ VAZADO |
| ▣ MUDANÇA DE SEÇÃO | L LAJE |
| ▣ PILAR SOBE | H ALTURA DA LAJE |
| ▣ PILAR MORRE | V VIGA |
| | P PILAR |
| | S SAPATA |

Responsável Técnico

Área: Área terreno _____ m²
Área construída _____ m²

Obra: Residência unifamiliar.

Local:

Assunto: PLANTA DE FÔRMA - 1º ANDAR

Folha: 01/01

Escala: 1:50


Data:

Calculista Estrutural:

Proprietário:

Estrutural

PLANTA DE FÔRMA - 1º ANDAR

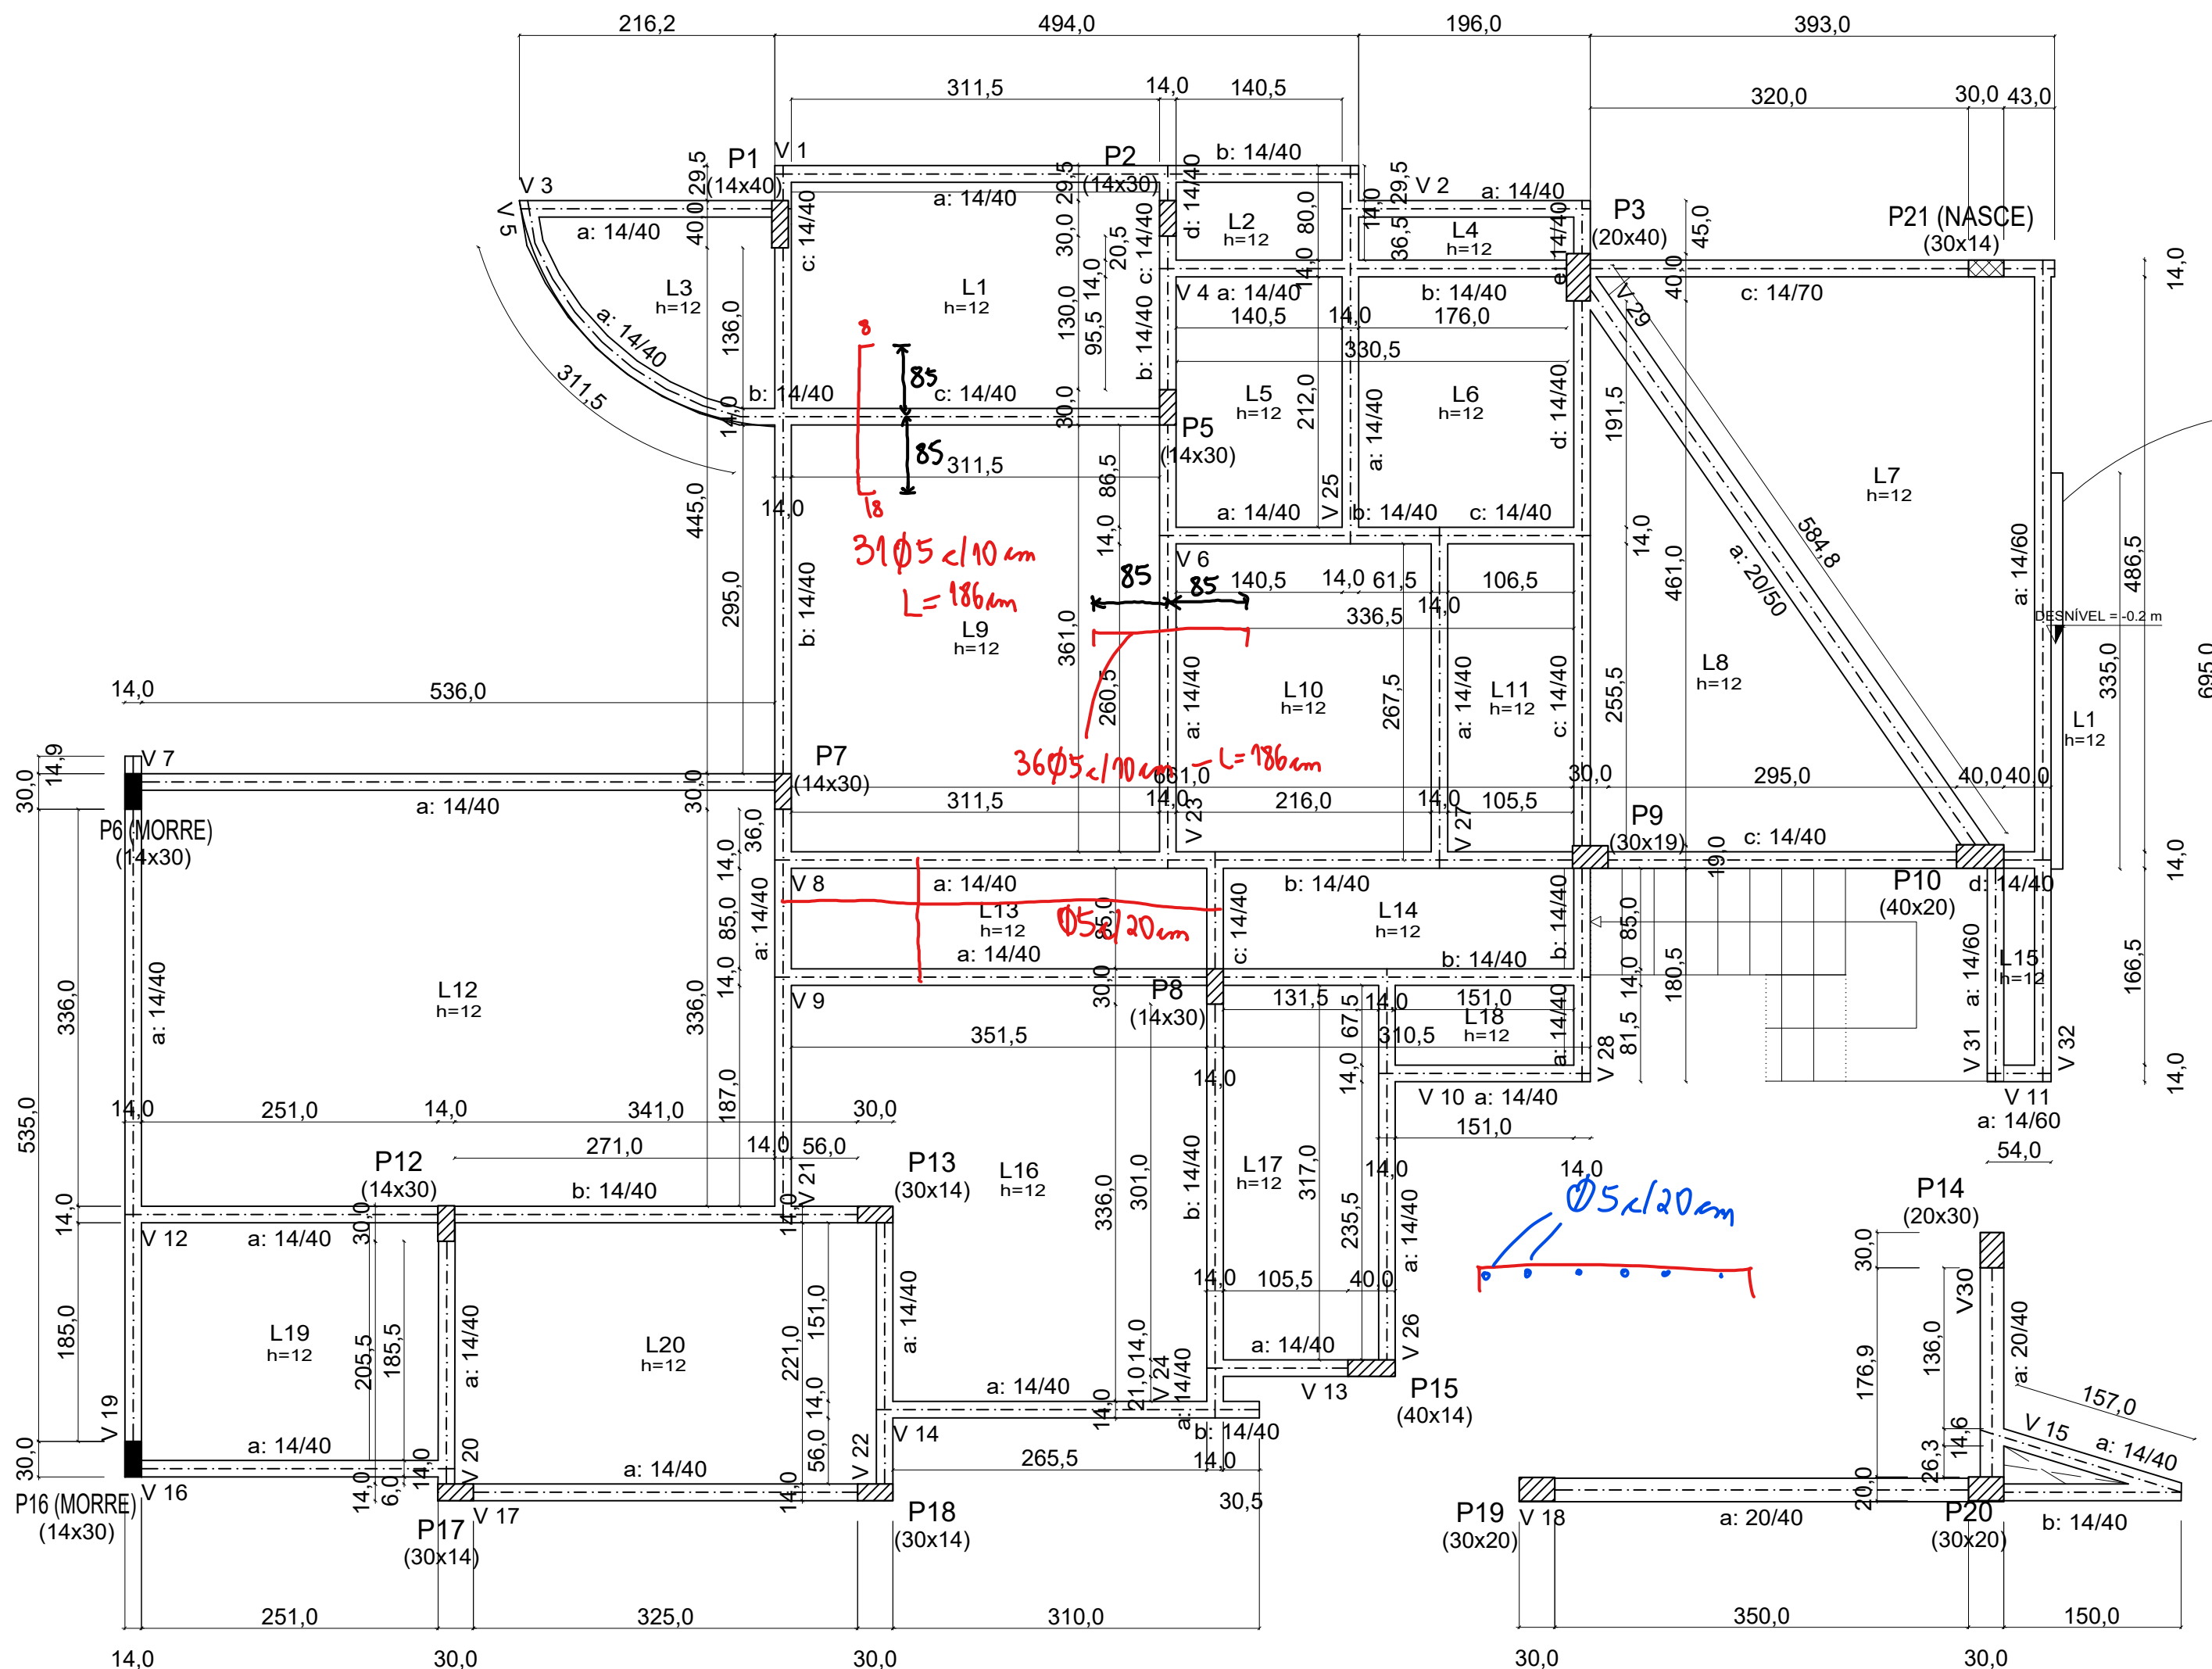


PLANTA DE FÔRMA - 1º ANDAR (+3,45)
esc 1:50

PERSPECTIVA 1

PERSPECTIVA 2

PERSPECTIVA 3

PERSPECTIVA 4

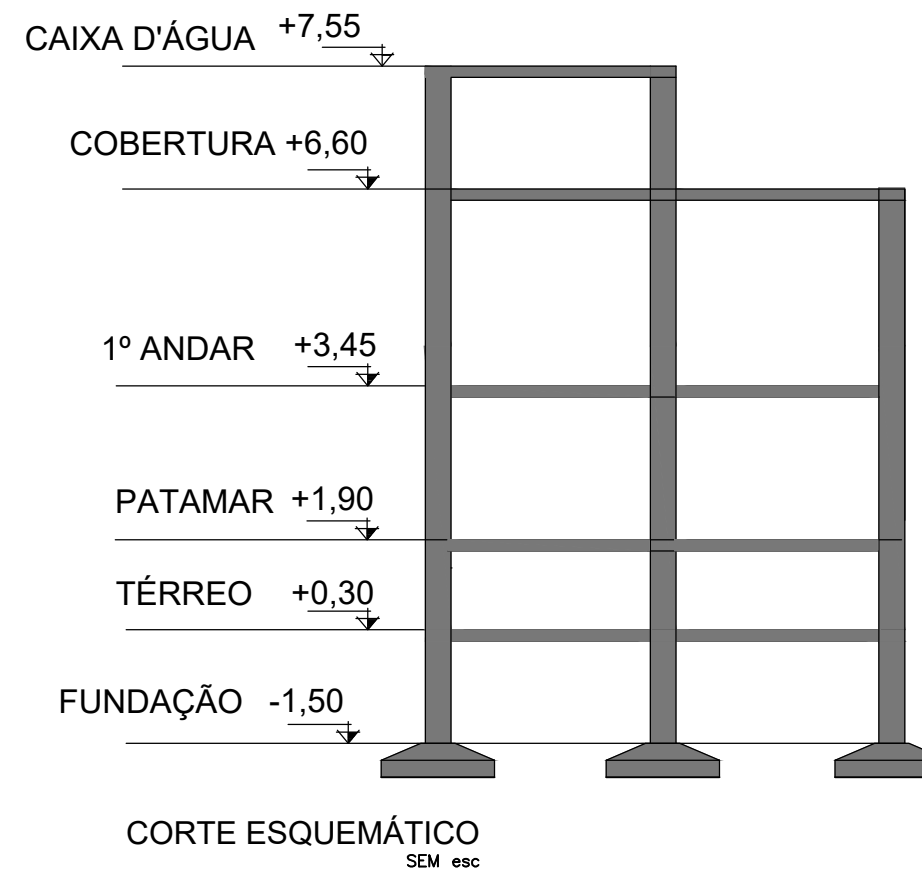

NOTAS

- 1- POSICIONAR SAPATAS SOBRE CONCRETO MAGRO DE 5cm DE ESPESSURA;
- 2- A EXECUÇÃO DO ESCORAMENTO DEVE RESPEITAR A NBR 15696
- 3- RETIRAR ESCORAMENTO APÓS 28 DIAS DA CONCRETAGEM
- 4 - QUALQUER MODIFICAÇÃO OU DÚVIDA NO PROJETO DEVERÁ SER IMEDIATAMENTE INFORMADA AO PROJETISTA ESTRUTURAL

PROJETO ESTRUTURAL

COBRIMENTOS MÍNIMOS

LAJE E ESCADA: 2,5cm
PILAR: 2,5cm
PILAR (CONTATO COM O SOLO): 2,5cm

SAPATA: 4cm
VIGA: 2,5cm

CONCRETO

fck = **25** MPa
AÇO: CA-50 E CA-60

LEGENDA

▣ PILAR NASCE	▣ VAZADO
▣ MUDANÇA DE SEÇÃO	L LAJE
▣ PILAR SOBE	H ALTURA DA LAJE
▣ PILAR MORRE	V VIGA
	P PILAR
	S SAPATA

Responsável Técnico

Área: Área terreno _____ m²
Área construída _____ m²

Obra: Residência unifamiliar.

Local:

Assunto: PLANTA DE FÔRMA - 1º ANDAR

Folha: 01/01

Escala: 1:50

Data:

Calculista Estrutural:

Proprietário:

Estrutural