


DETALHAMENTO ESCADA


ESCADA		
Geometria	Largura	0.900 m
	Espessura	0.15 m
	Piso	0.270 m
	Espelho	0.195 m
	Desnível que vence	3.12 m
	Nº de degraus	16
	Piso final	B - 1º ANDAR
Materiais	Piso inicial	A - TÉRREO
	Concreto	C25, em geral
	Aço	CA-50 e CA-60
	Cob. geométrico	2.0 cm

Seção C-C

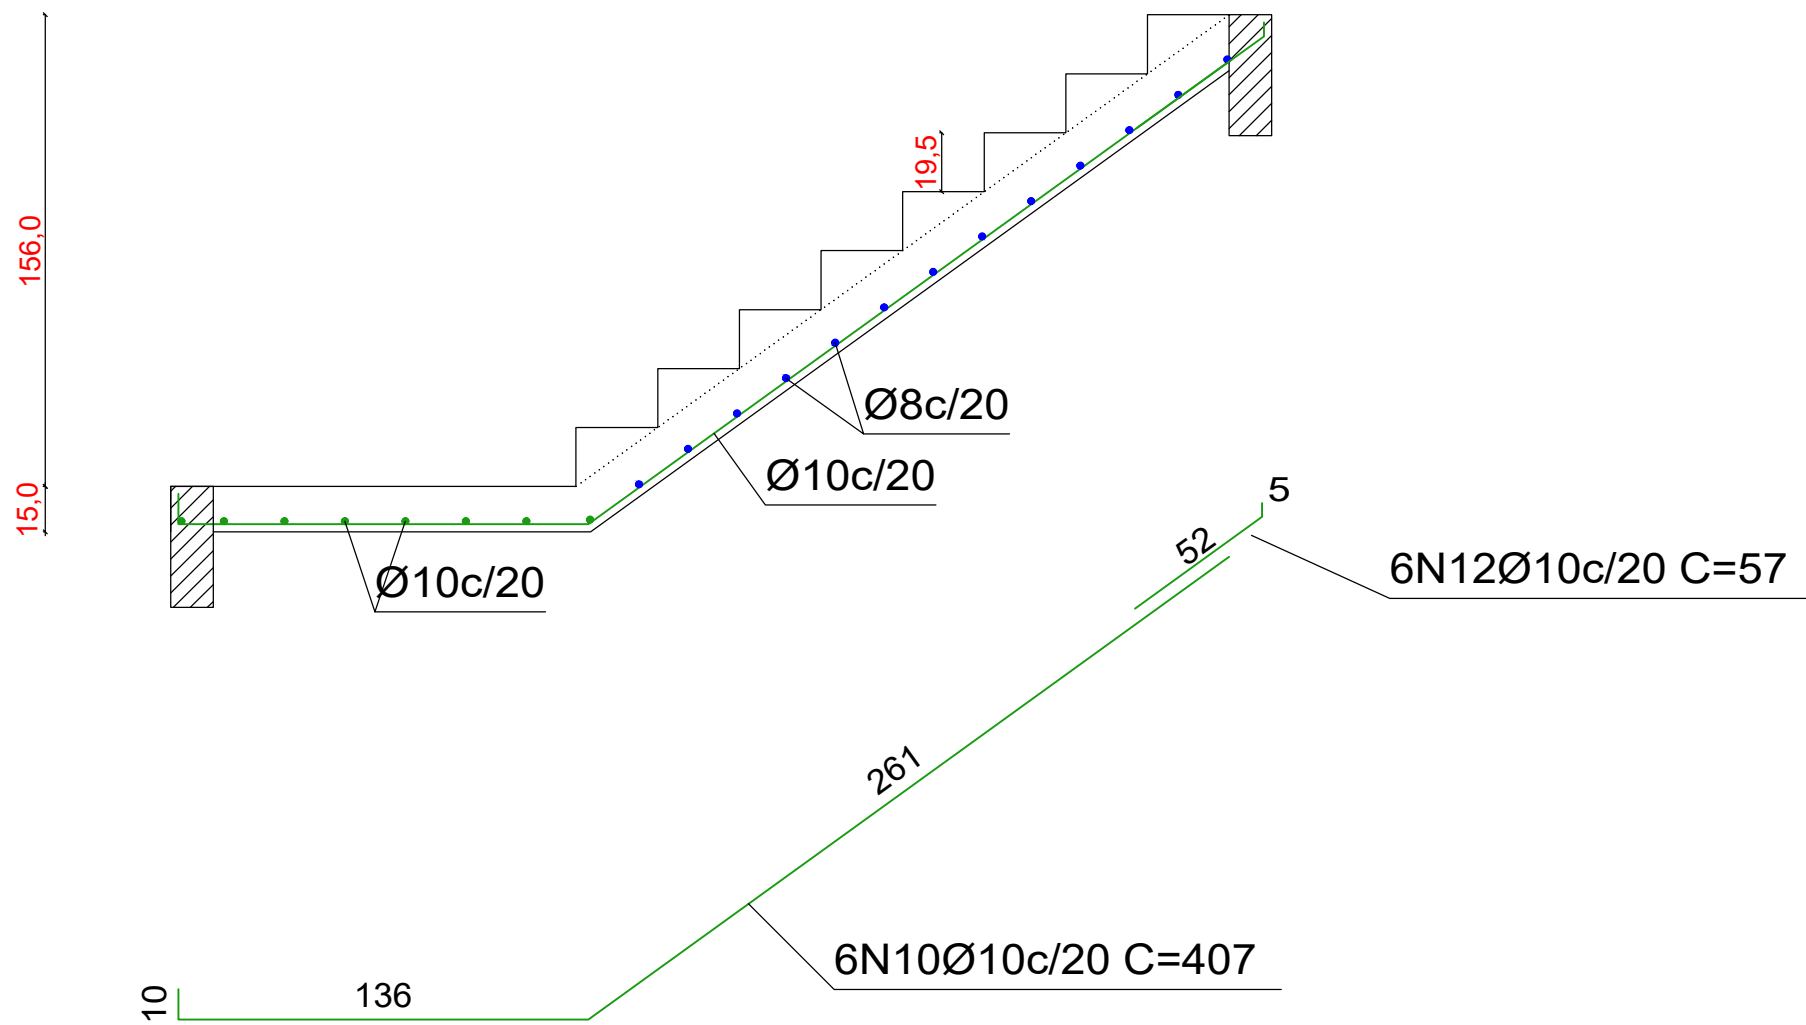


Seção D-D


Seção E-E

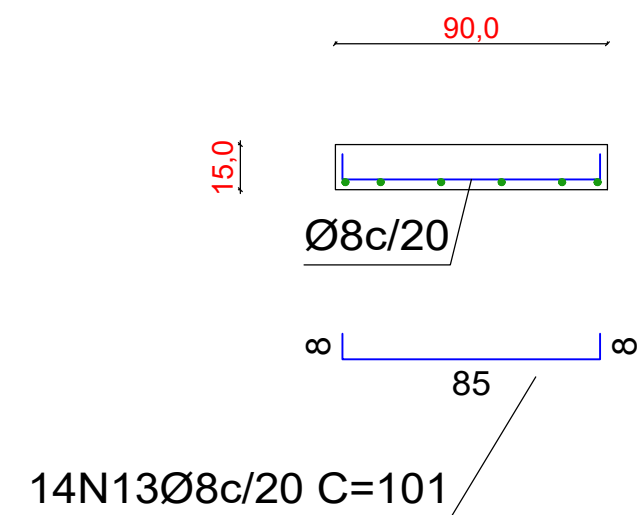


Seção A-A

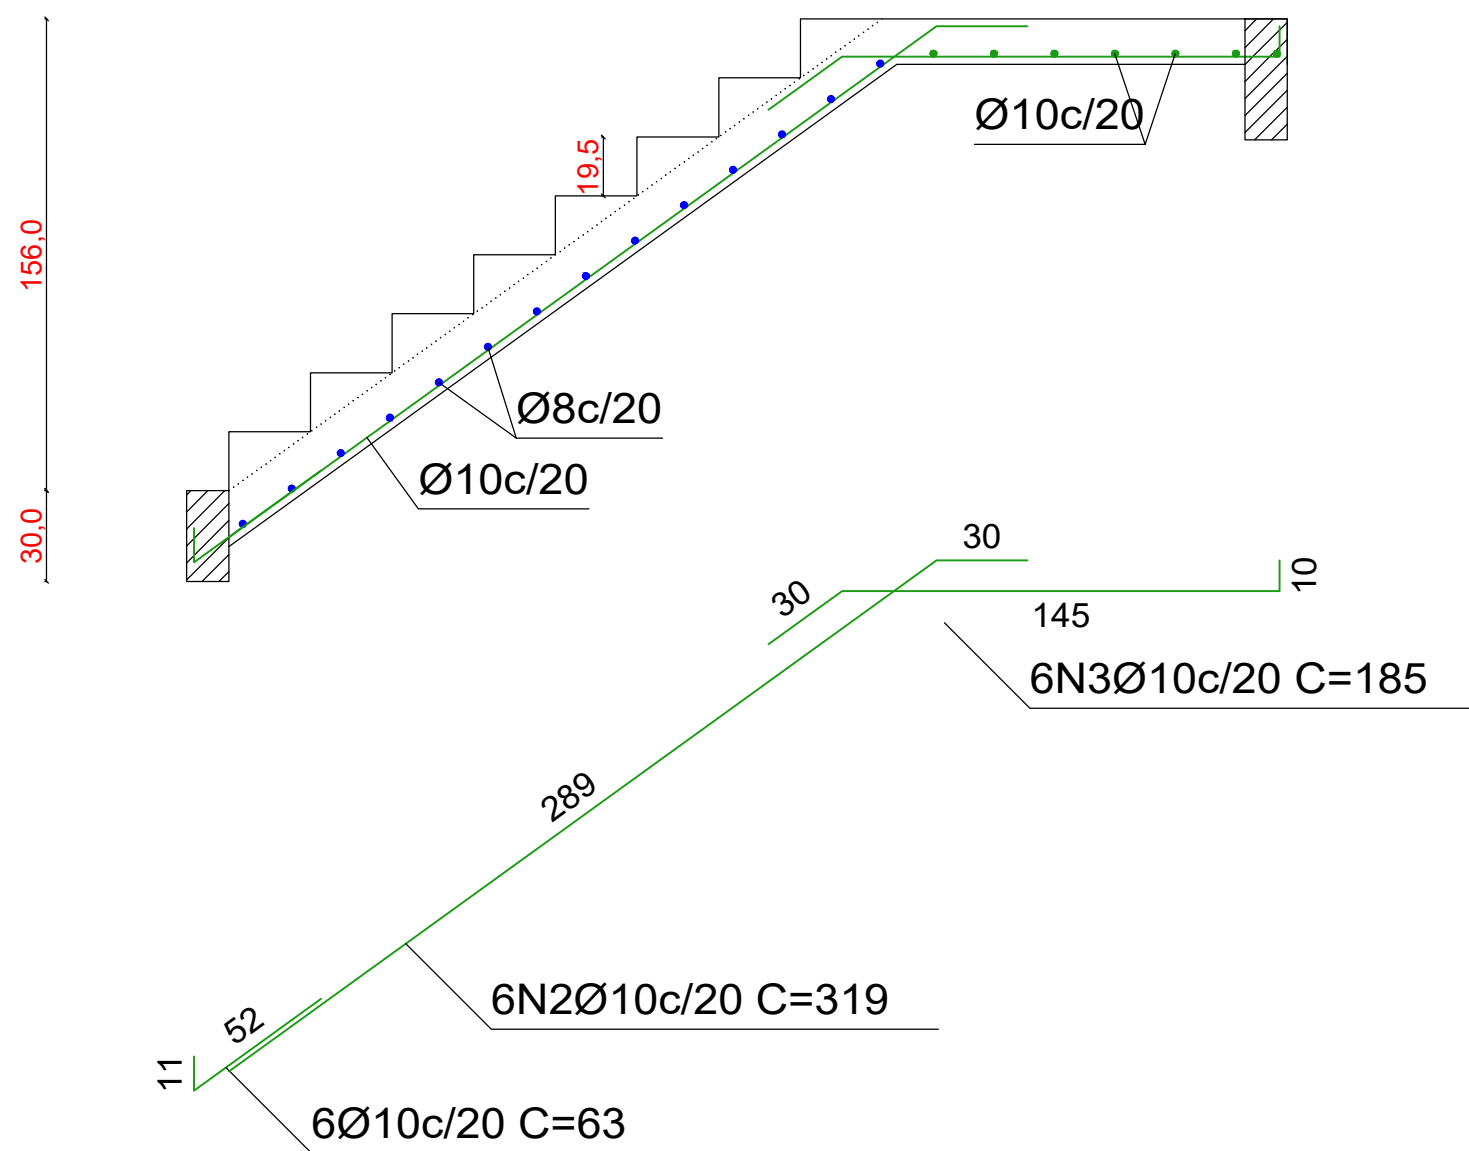

Seção B-B

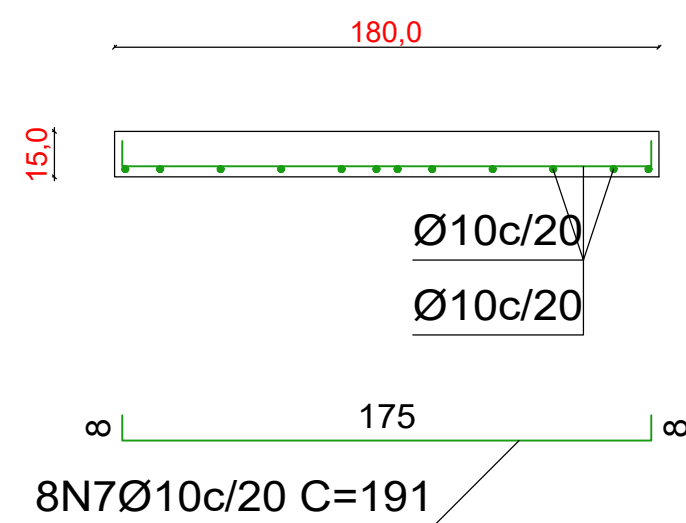

LEGENDA

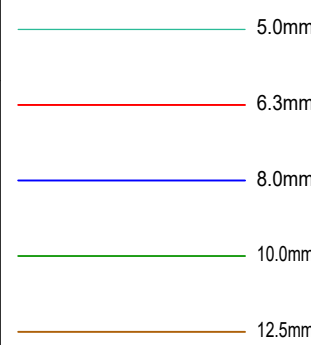

Resumo Aço Escada	Comp. total (m)	Peso+10% (kg)	Total
CA-50 Ø8 Ø10	14.1 77.1	7 53	60

NOTAS

- 1- POSICIONAR SAPATAS SOBRE CONCRETO MAGRO DE 5cm DE ESPESSURA;
- 2- A EXECUÇÃO DO ESCORAMENTO DEVE RESPEITAR A NBR 15696
- 3- RETIRAR ESCORAMENTO APÓS 28 DIAS DA CONCRETAGEM
- 4 - QUALQUER MODIFICAÇÃO OU DÚVIDA NO PROJETO DEVERÁ SER IMEDIATAMENTE INFORMADA AO PROJETISTA ESTRUTURAL

PROJETO ESTRUTURAL

COBRIMENTOS MÍNIMOS

LAJE E ESCADA: 2,5cm
PILAR: 2,5cm
PILAR (CONTATO COM O SOLO): 2,5cm

SAPATA: 4cm
VIGA: 2,5cm

CONCRETO

fck = **25** MPa
AÇO: CA-50 E CA-60

LEGENDA

▣ PILAR NASCE	▣ VAZADO
▣ MUDANÇA DE SEÇÃO	L LAJE
▣ PILAR SOBE	H ALTURA DA LAJE
▣ PILAR MORRE	V VIGA
	P PILAR
	S SAPATA

Responsável Técnico

Área: Área terreno _____ m²
Área construída _____ m²

Obra: Residência unifamiliar.

Local:

Assunto: DETALHAMENTO ESCADA

Folha: 01/01

Escala: 1:25

Data:

Calculista Estrutural:

Proprietário:

Estrutural