



PLANTA DE FÔRMA - 1º ANDAR

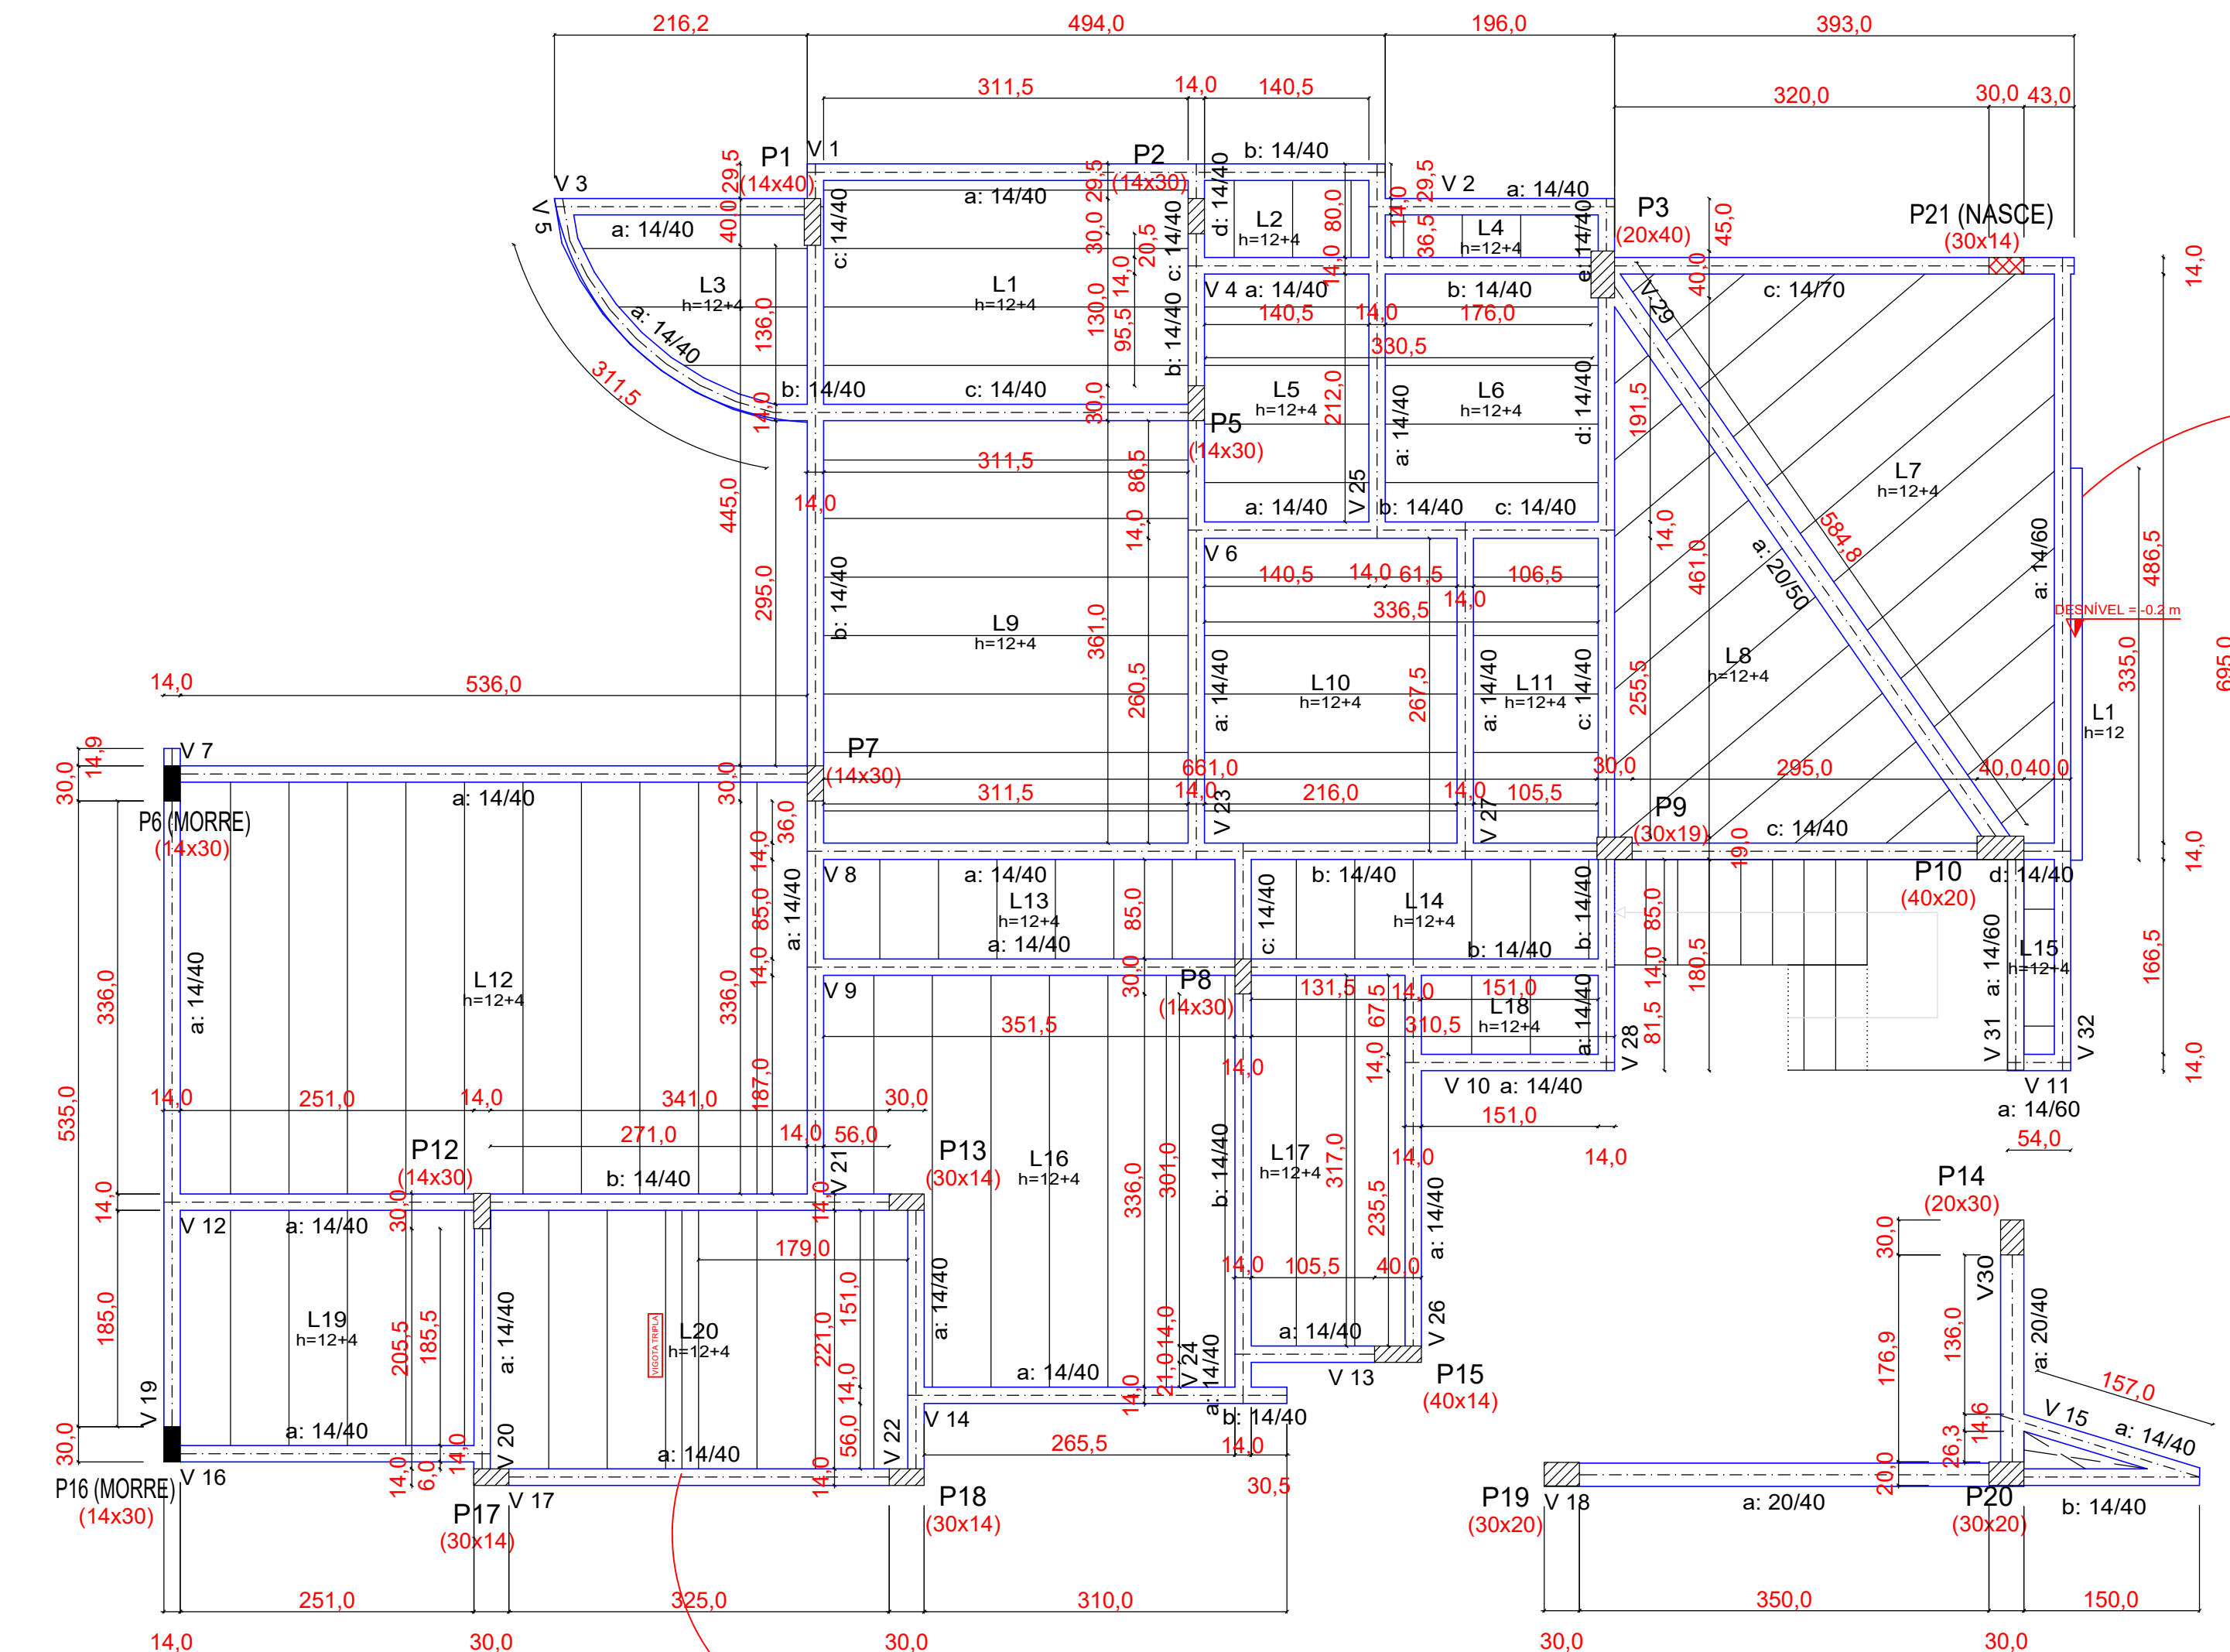


PLANTA DE FÔRMA - 1º ANDAR (+3,45)
esc 1:50

VIGOTA TRIPLA


PERSPECTIVA 1

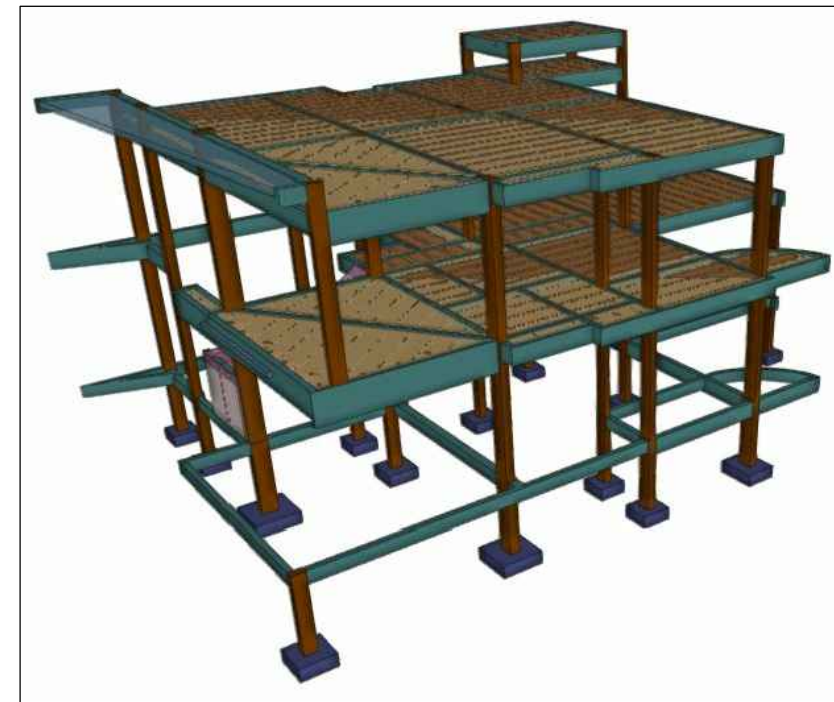



PERSPECTIVA 2

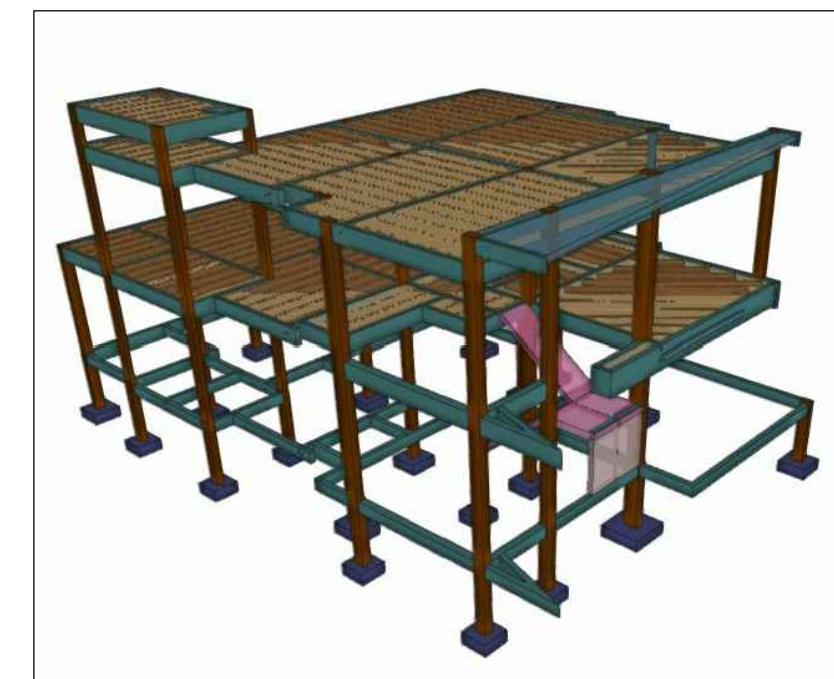

PERSPECTIVA 3

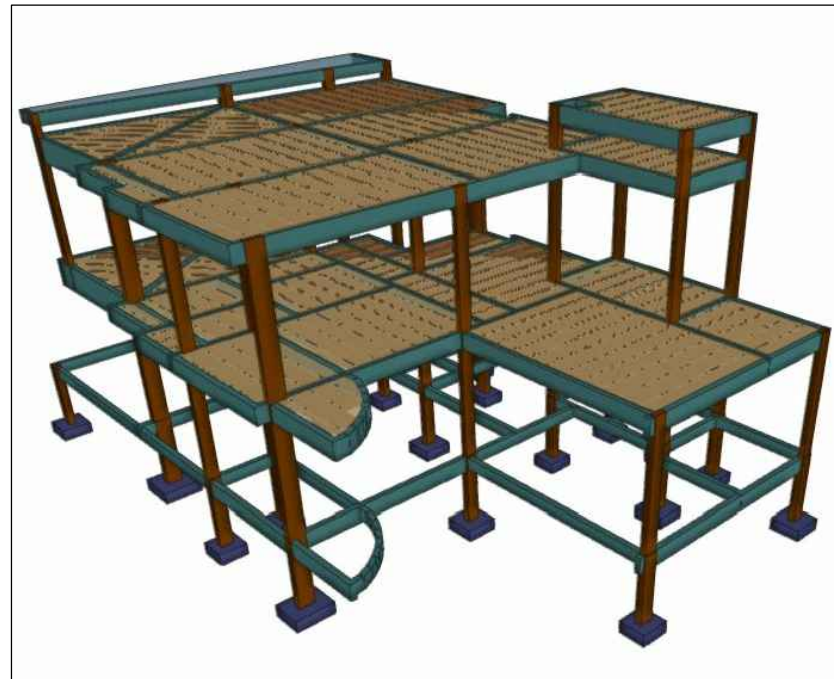

PERSPECTIVA 4

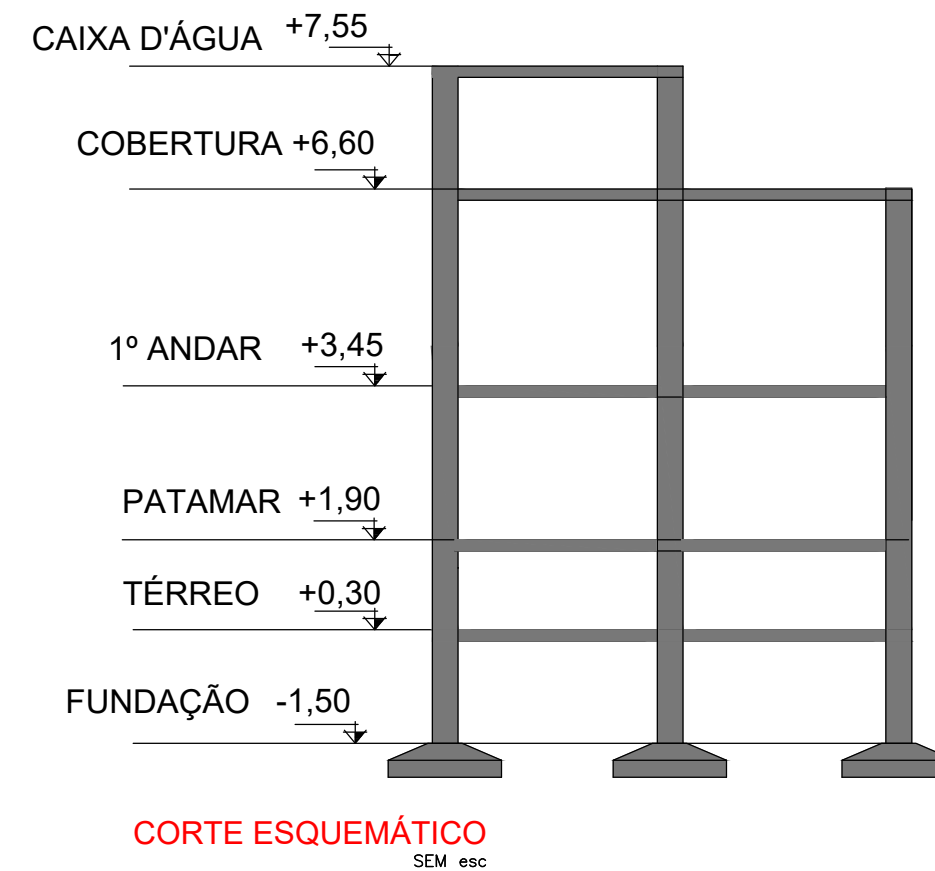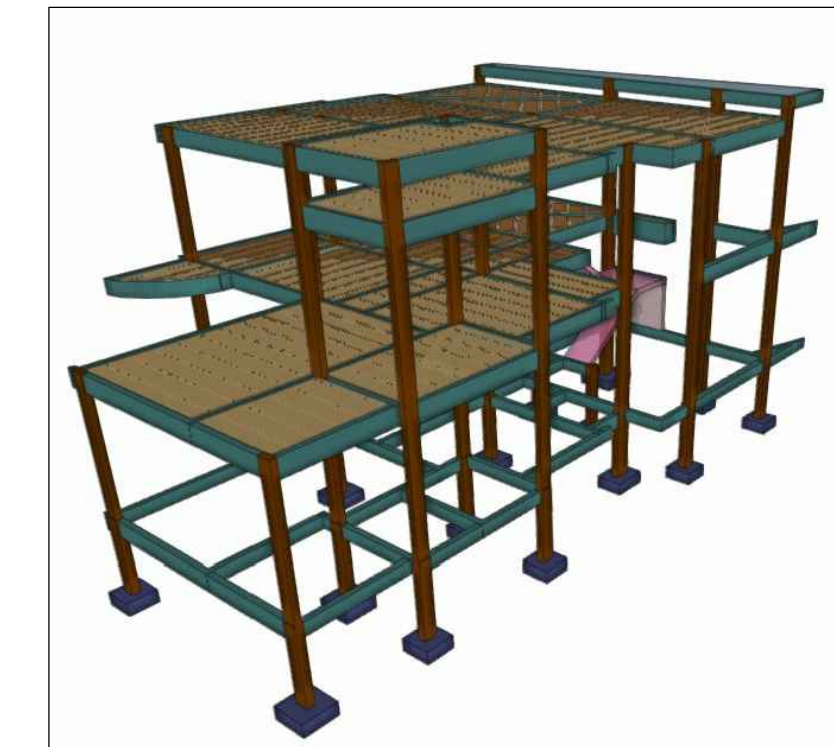

CORTE ESQUEMÁTICO
SEM esc

NOTAS

- 1- POSICIONAR SAPATAS SOBRE CONCRETO MAGRO DE 5cm DE ESPESSURA;
- 2- A EXECUÇÃO DO ESCORAMENTO DEVE RESPEITAR A NBR 15696
- 3- RETIRAR ESCORAMENTO APÓS 28 DIAS DA CONCRETAGEM
- 4 - QUALQUER MODIFICAÇÃO OU DÚVIDA NO PROJETO DEVERÁ SER IMEDIATAMENTE INFORMADA AO PROJETISTA ESTRUTURAL

PROJETO ESTRUTURAL

COBRIMENTOS MÍNIMOS

LAJE E ESCADA: 2,5cm
PILAR: 2,5cm
PILAR (CONTATO COM O SOLO): 2,5cm

SAPATA: 4cm
VIGA: 2,5cm

CONCRETO
fck = **25** MPa
AÇO: CA-50 E CA-60

LEGENDA

- | | |
|--------------------|------------------|
| ▣ PILAR NASCE | ▣ VAZADO |
| ▣ MUDANÇA DE SEÇÃO | L LAJE |
| ▣ PILAR SOBE | H ALTURA DA LAJE |
| ▣ PILAR MORRE | V VIGA |
| | P PILAR |
| | S SAPATA |

Responsável Técnico

Área: Área terreno _____ m²
Área construída _____ m²

Obra: Residência unifamiliar.

Local:

Assunto: PLANTA DE FÔRMA - 1º ANDAR

Folha: 01/01

Escala: 1:50

Data:

Calculista Estrutural:

Proprietário:

Estrutural