



DETALHAMENTO SAPATAS


S1
Esc. 1:50

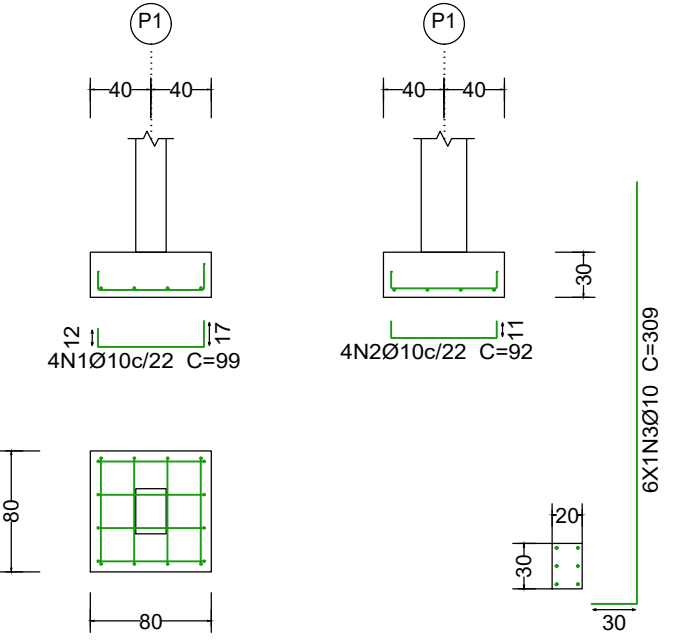


S2
Esc. 1:50

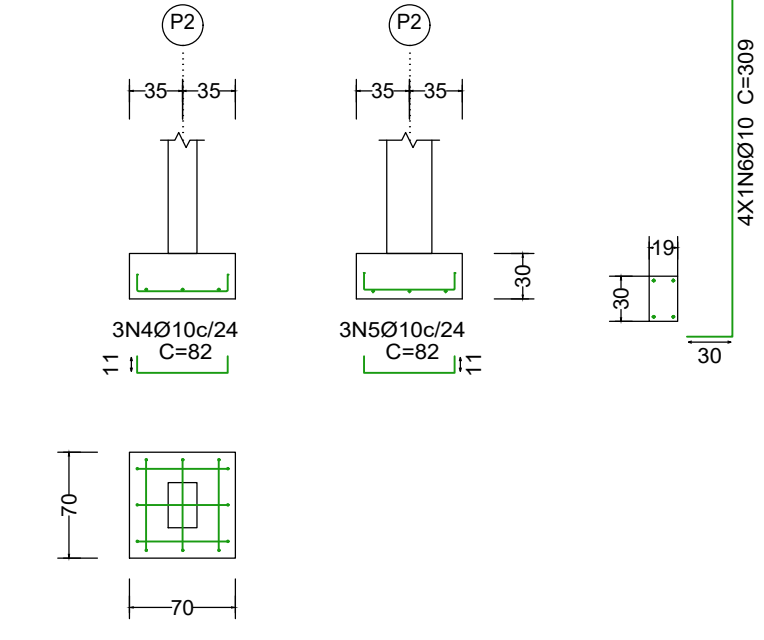


S3
Esc. 1:50

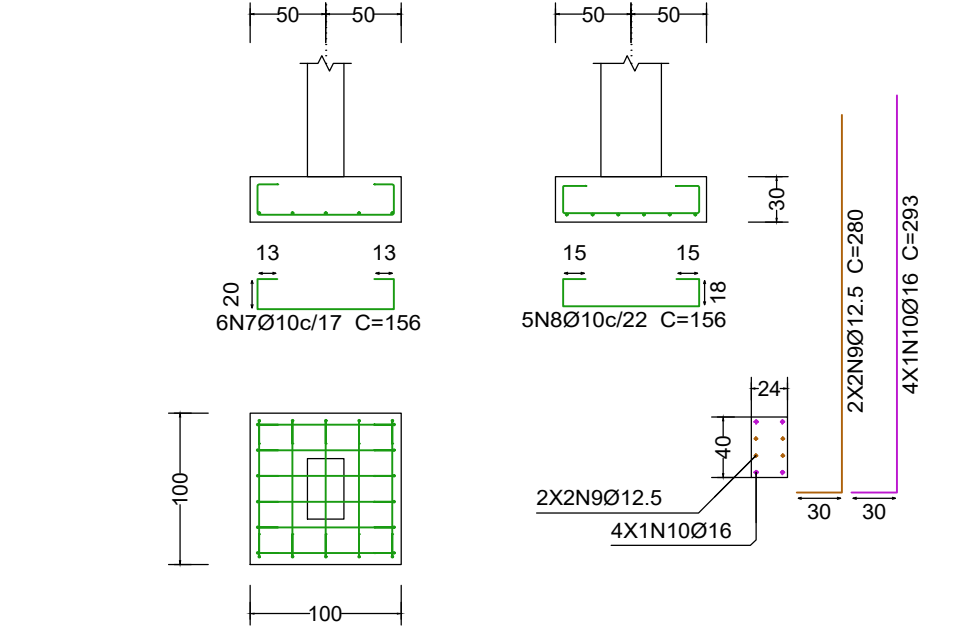


S4
Esc. 1:50

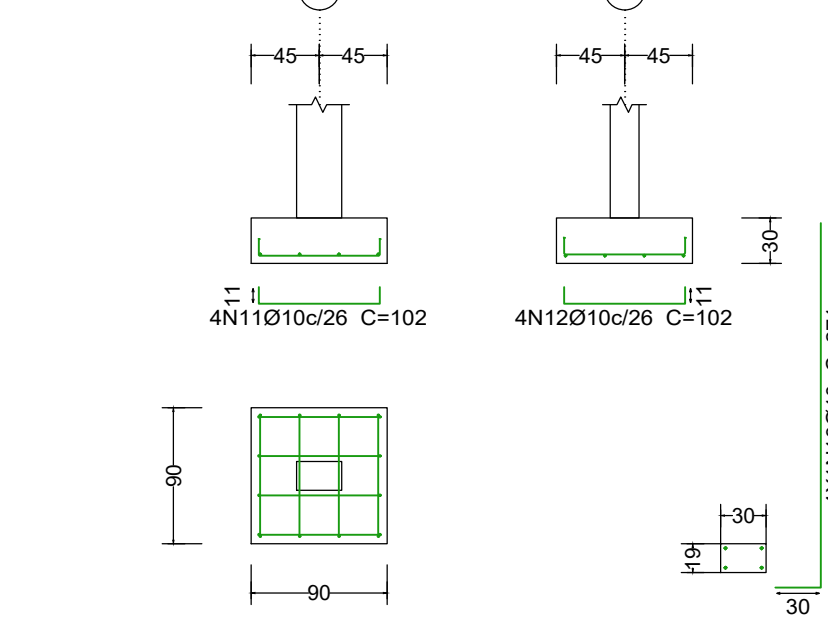


S5
Esc. 1:50

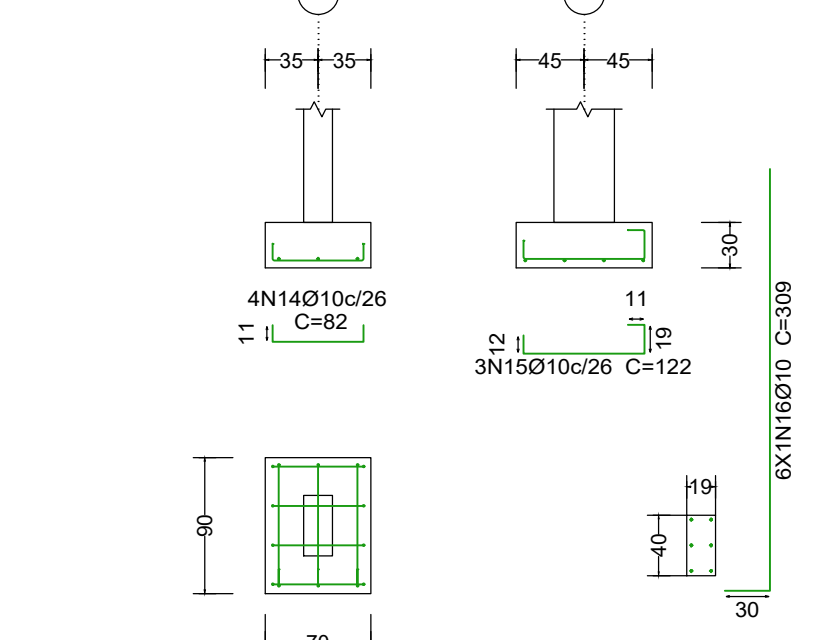


S6
Esc. 1:50

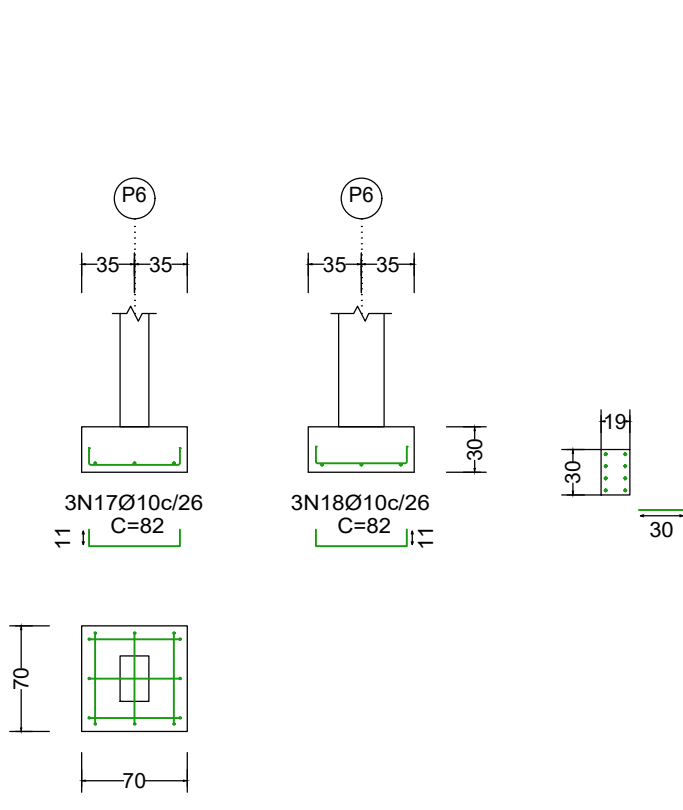


S7
Esc. 1:50

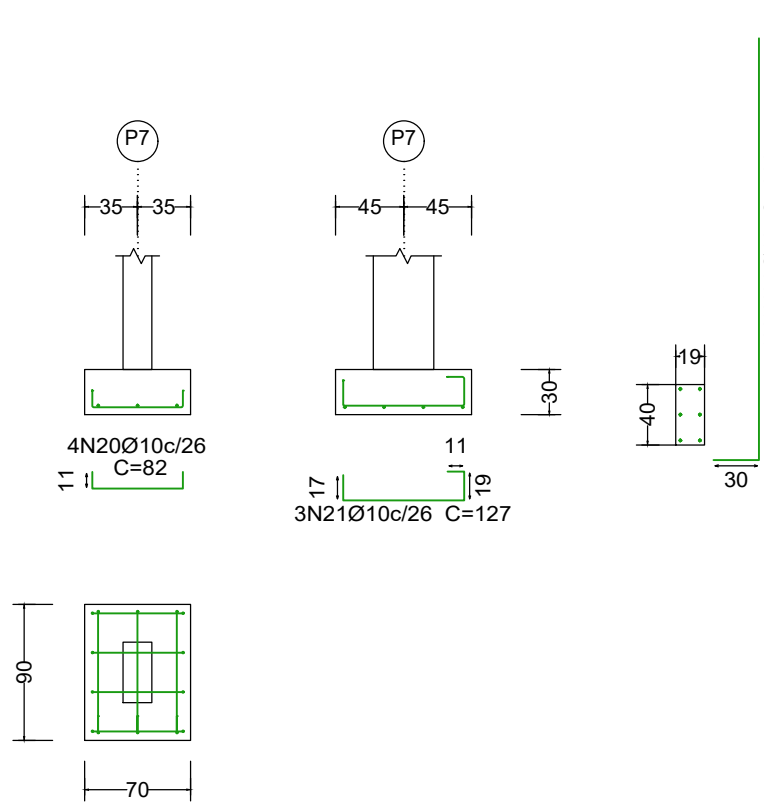


S8
Esc. 1:50

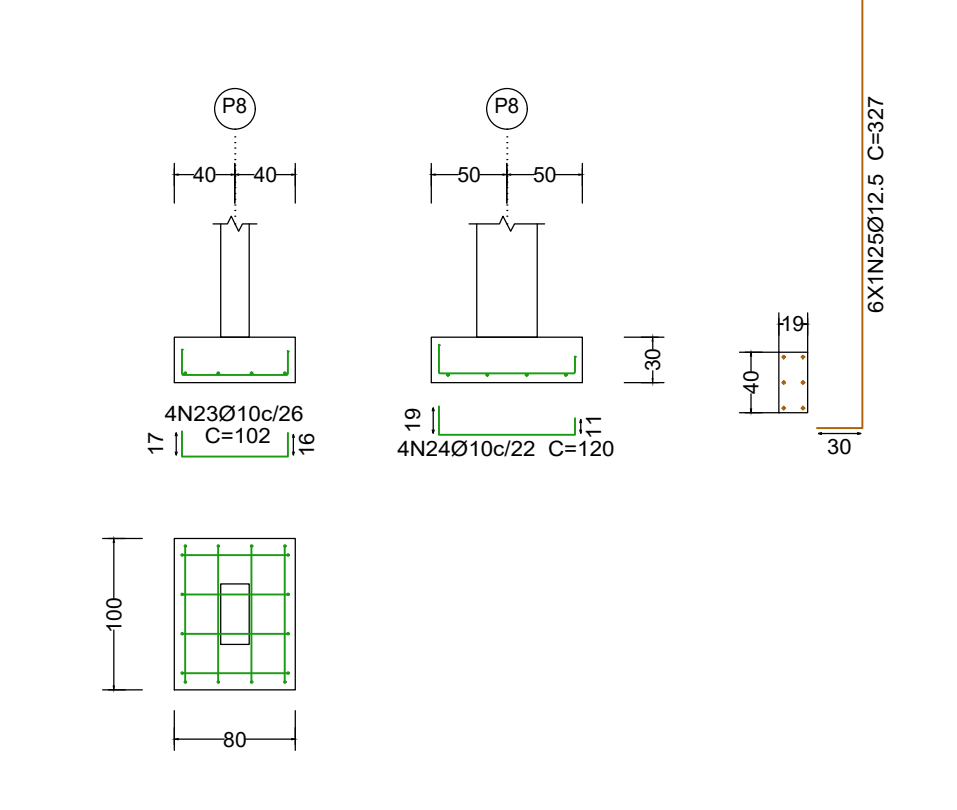


S9
Esc. 1:50

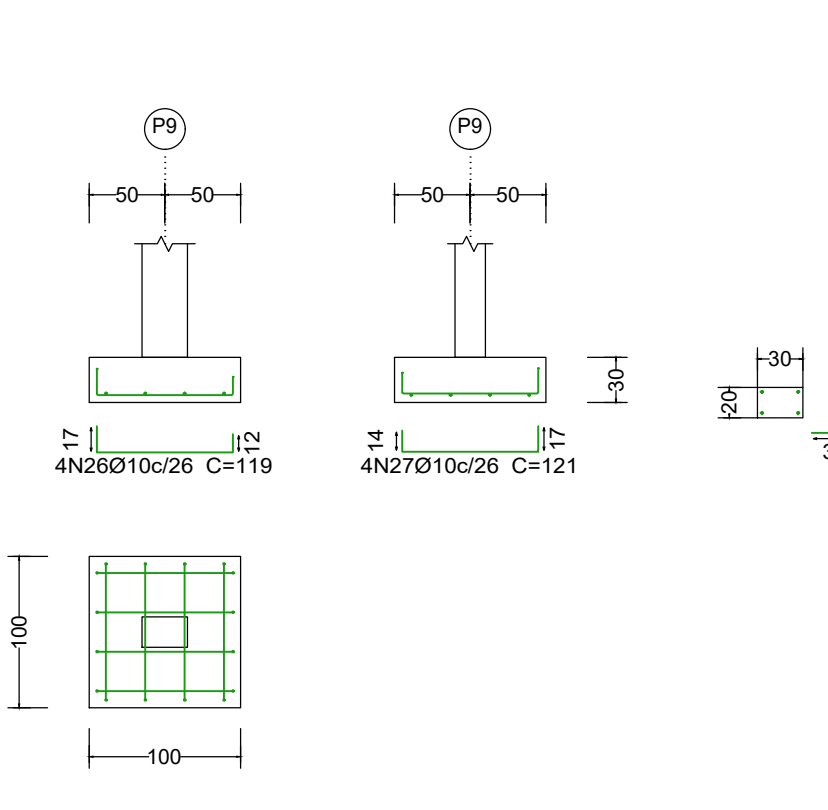


S10
Esc. 1:50

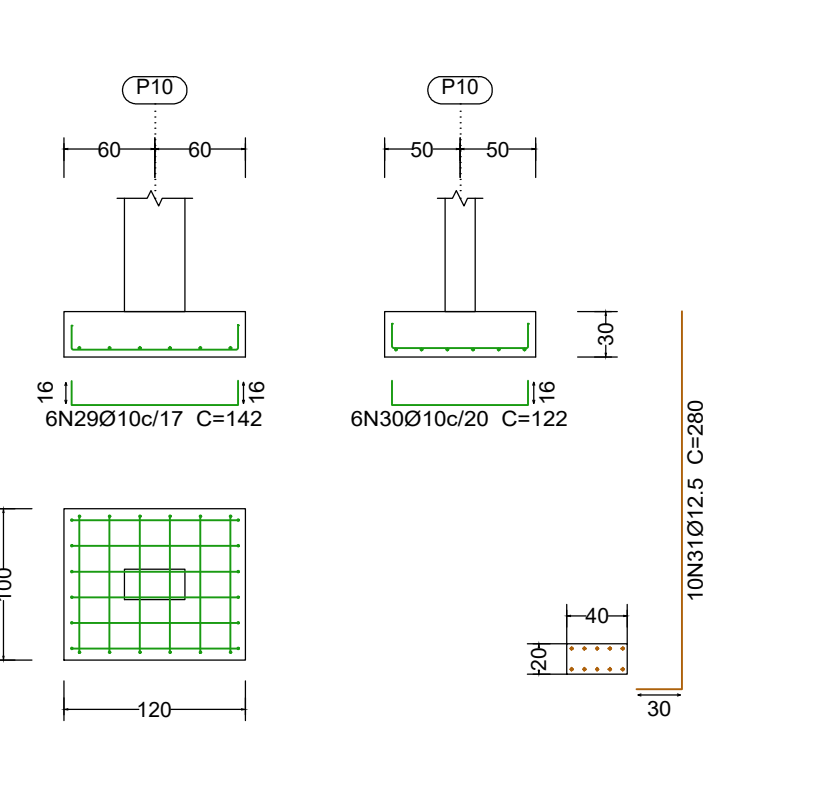


S11
Esc. 1:50

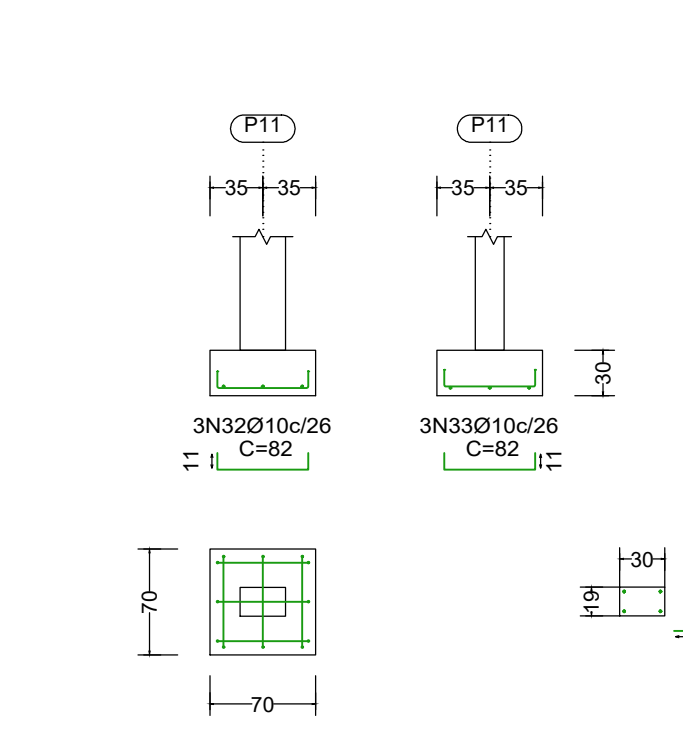


S12
Esc. 1:50

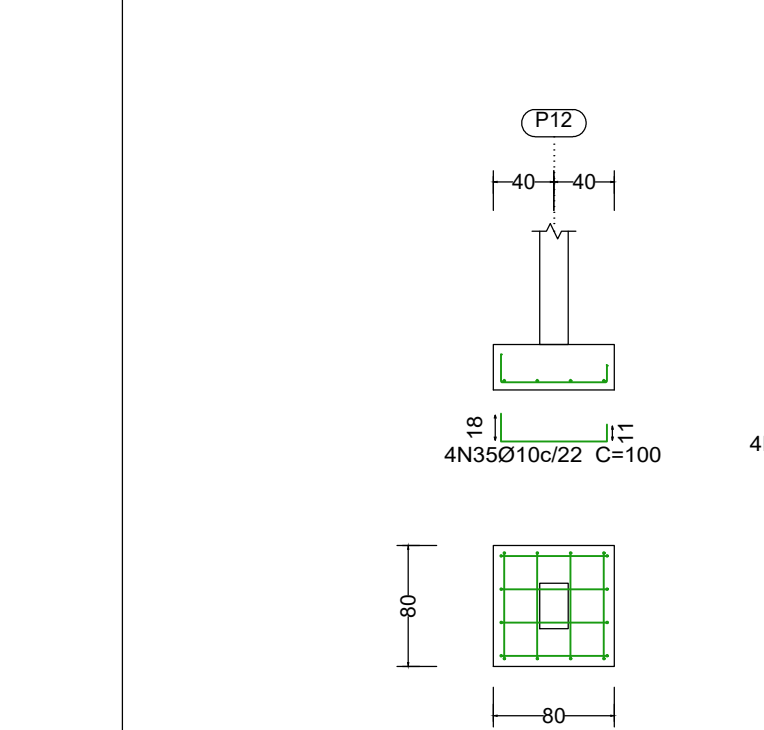


S13, S16, S17
Esc. 1:50

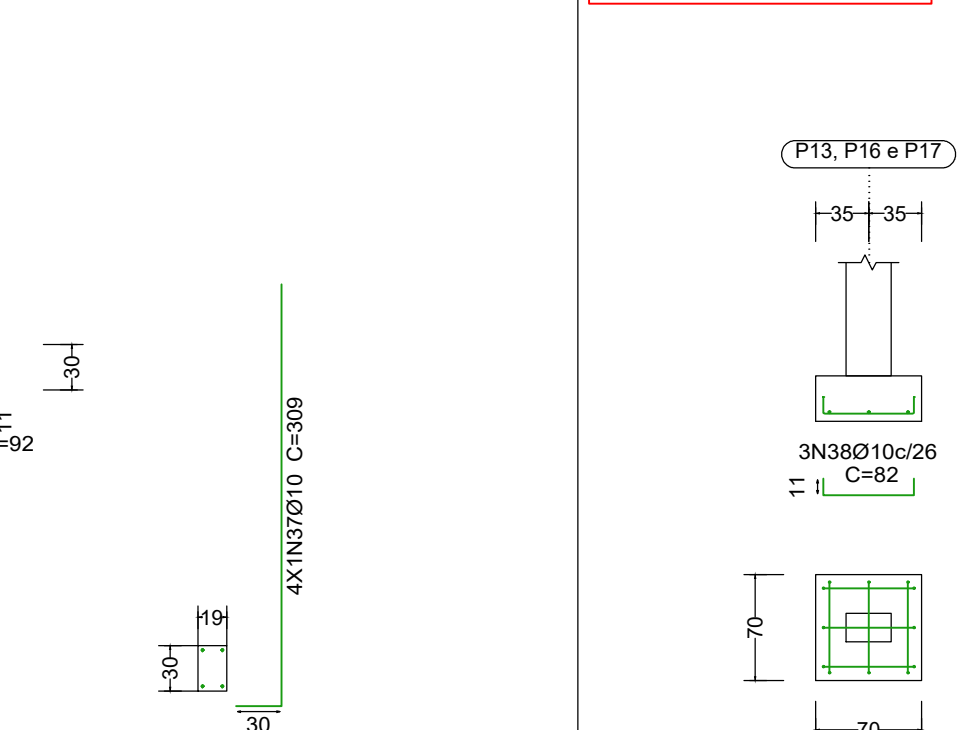


S14
Esc. 1:50

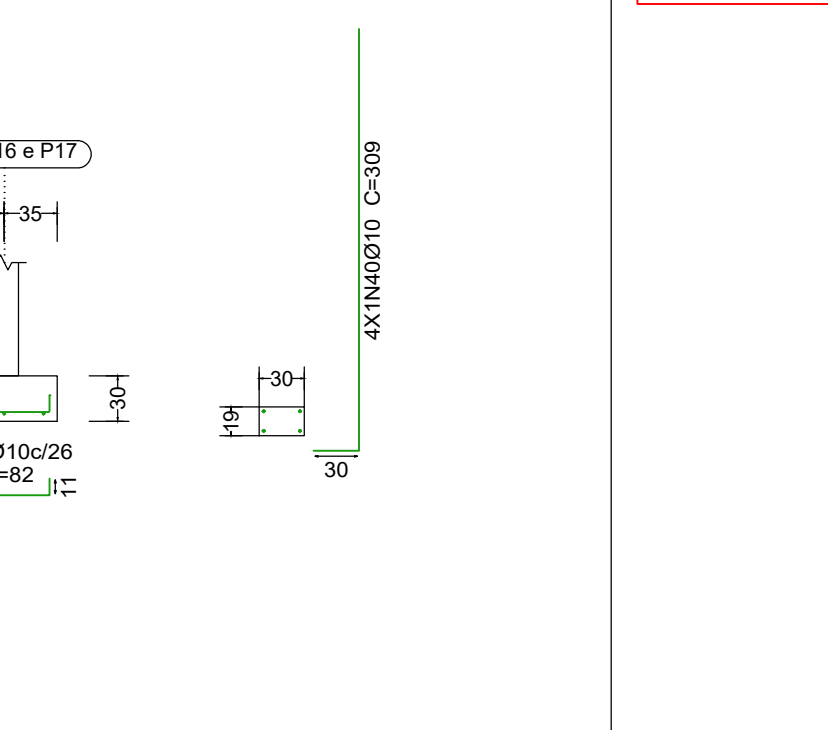


S15
Esc. 1:50

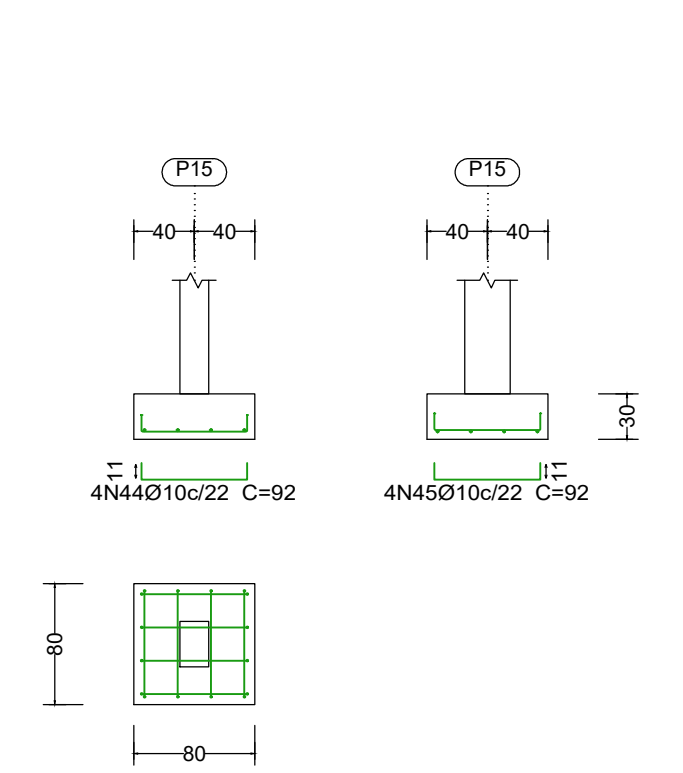


S18
Esc. 1:50

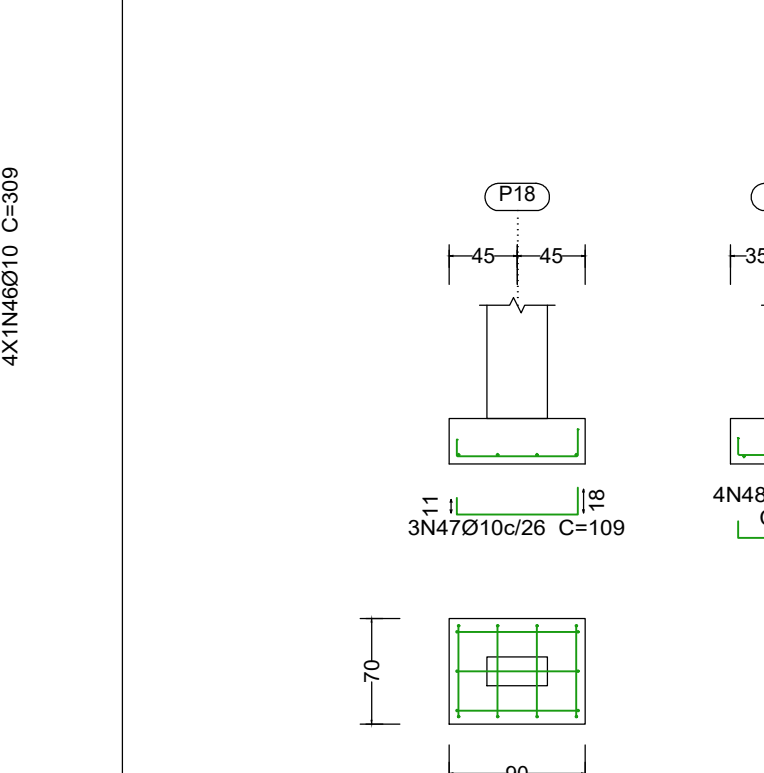


S19
Esc. 1:50

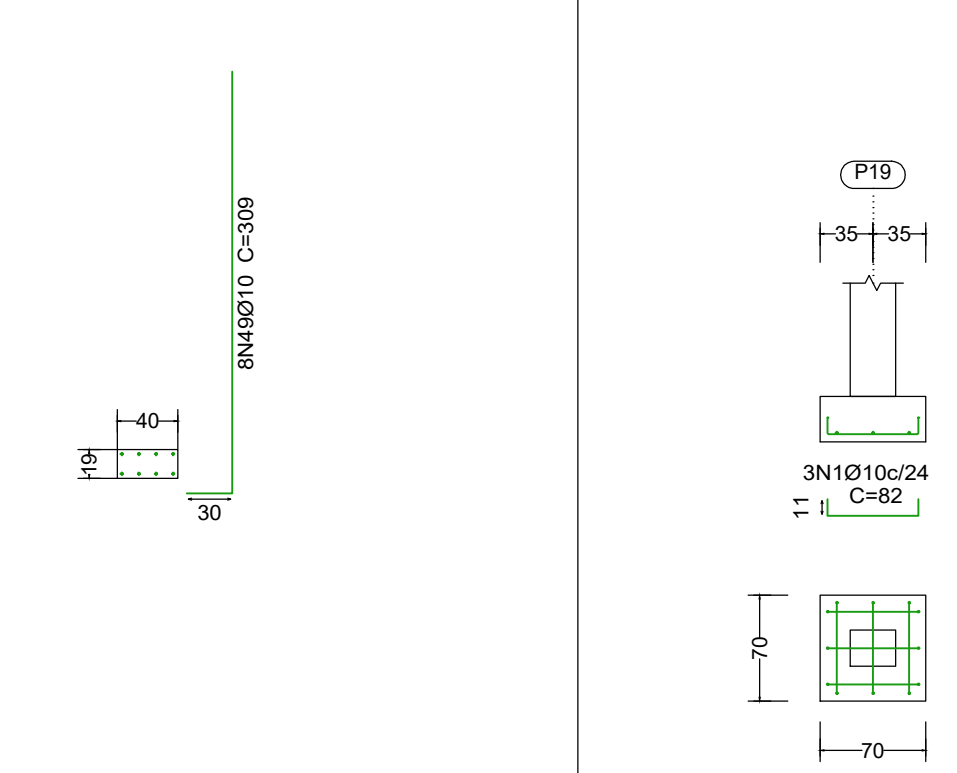

S20
Esc. 1:50

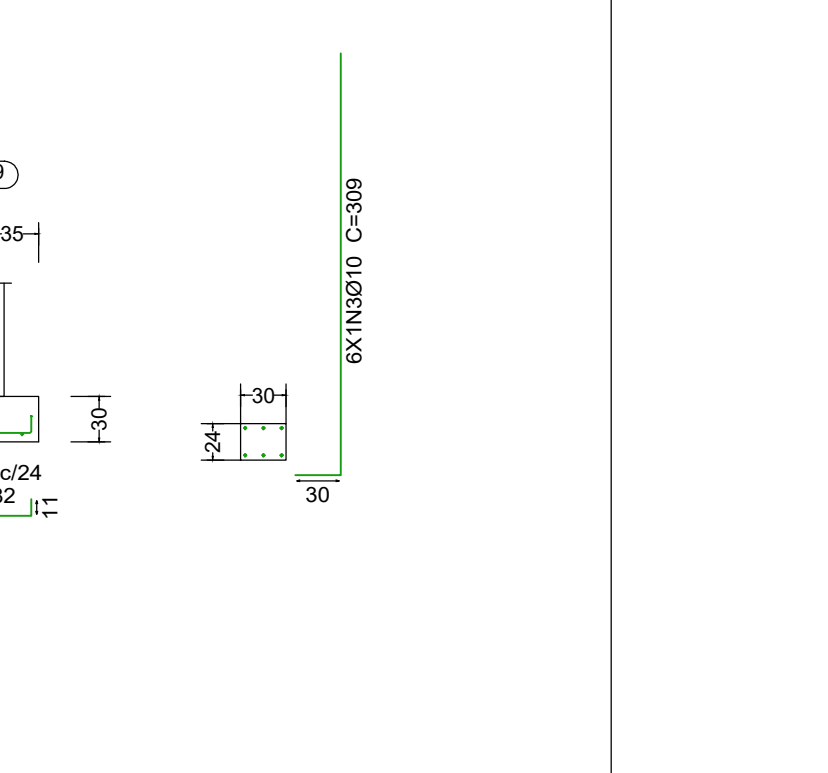

LEGENDA

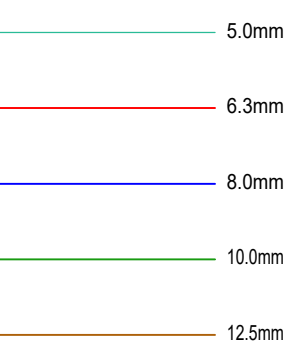

Resumo Aço Fundação	Comp. total (m)	Peso+10% (kg)	Total
CA-50	Ø10	391.3	265
	Ø12.5	75.6	80
	Ø16	11.7	20
			365

QUADRO DE ELEMENTOS DE FUNDAÇÃO				
Referências	Dimensões (cm)	Altura (cm)	Armadura inf. X	Armadura inf. Y
S1	80x80	30	4Ø10c/22	4Ø10c/22
S2 e S19	70x70	30	3Ø10c/24	3Ø10c/24
S3	100x100	30	6Ø10c/17	6Ø10c/22
S4	90x90	30	4Ø10c/26	4Ø10c/26
S5	70x90	30	4Ø10c/26	3Ø10c/26
S6, S11, S13, S14, S16, S17 e S20	70x70	30	3Ø10c/26	3Ø10c/26
S7	70x90	30	4Ø10c/26	3Ø10c/26
S8	80x100	30	4Ø10c/26	4Ø10c/22
S9	100x100	30	4Ø10c/26	4Ø10c/26
S10	120x100	30	6Ø10c/17	6Ø10c/20
S12	80x80	30	4Ø10c/22	4Ø10c/22
S15	80x80	30	4Ø10c/22	4Ø10c/22
S18	90x70	30	3Ø10c/26	4Ø10c/26

NOTAS

- 1- POSICIONAR SAPATAS SOBRE CONCRETO MAGRO DE 5cm DE ESPESSURA;
- 2- A EXECUÇÃO DO ESCORAMENTO DEVE RESPEITAR A NBR 15696
- 3- RETIRAR ESCORAMENTO APÓS 28 DIAS DA CONCRETAGEM
- 4 - QUALQUER MODIFICAÇÃO OU DÚVIDA NO PROJETO DEVERÁ SER IMEDIATAMENTE INFORMADA AO PROJETISTA ESTRUTURAL

PROJETO ESTRUTURAL

COBRIMENTOS MÍNIMOS

LAJE E ESCADA: 2,5cm
PILAR: 2,5cm
PILAR (CONTATO COM O SOLO): 2,5cm

SAPATA: 4cm
VIGA: 2,5cm

CONCRETO
fck = 25 MPa
AÇO: CA-50 E CA-60

LEGENDA

- ▣ PILAR NASCE
- ▣ MUDANÇA DE SEÇÃO
- ▣ PILAR SOBE
- ▣ PILAR MORRE
- ▣ VAZADO
- L LAJE
- H ALTURA DA LAJE
- V VIGA
- P PILAR
- S SAPATA

Responsável Técnico

Obra: Residência unifamiliar.
Local:

Assunto: DETALHAMENTO SAPATAS:
S1, S2, S3, S4, S5, S6, S7, S8, S9, S10, S11, S12, S13, S14, S15, S16, S17, S18, S19, S20

Folha: 01/01

Escala: 1:50

Proprietário:

Estrutural